




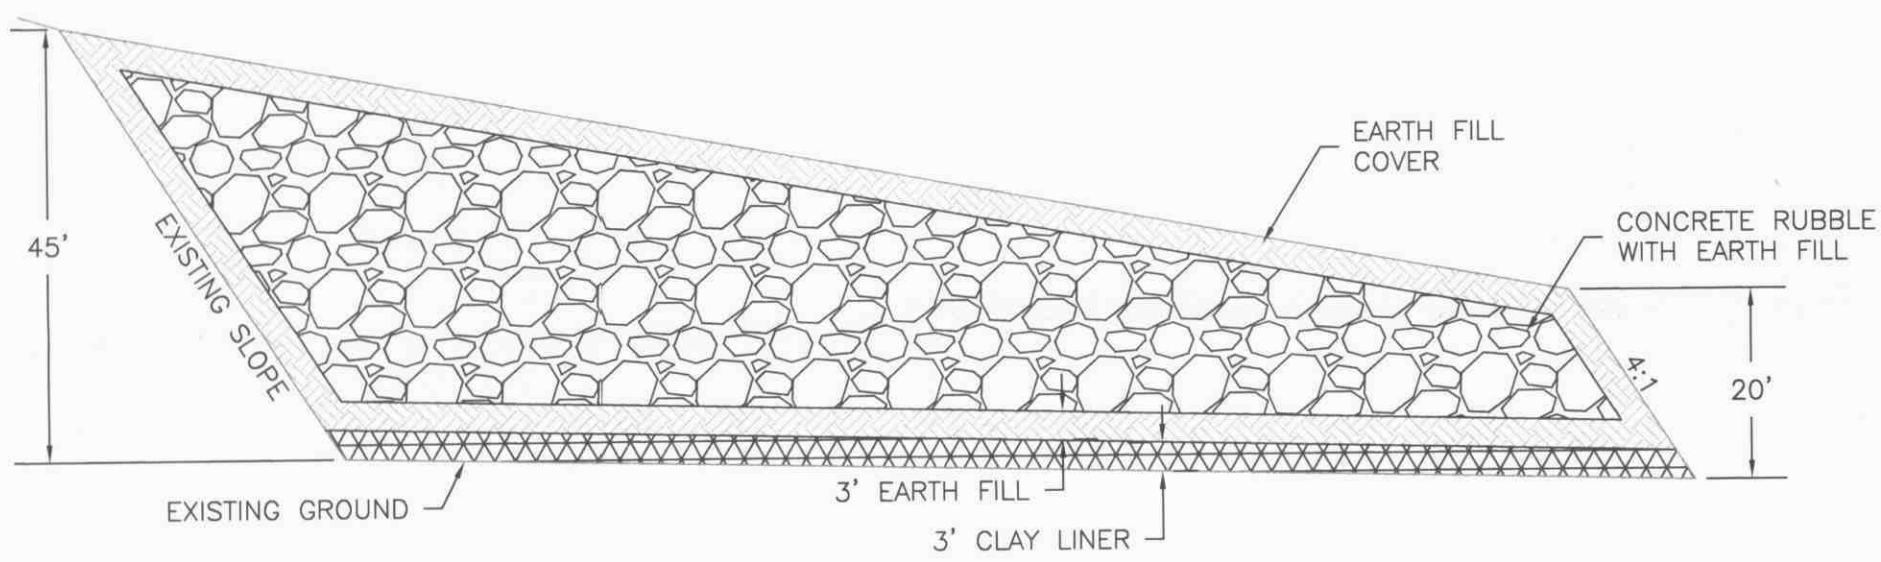

TYPICAL CROSS SECTION A-A'
NTS

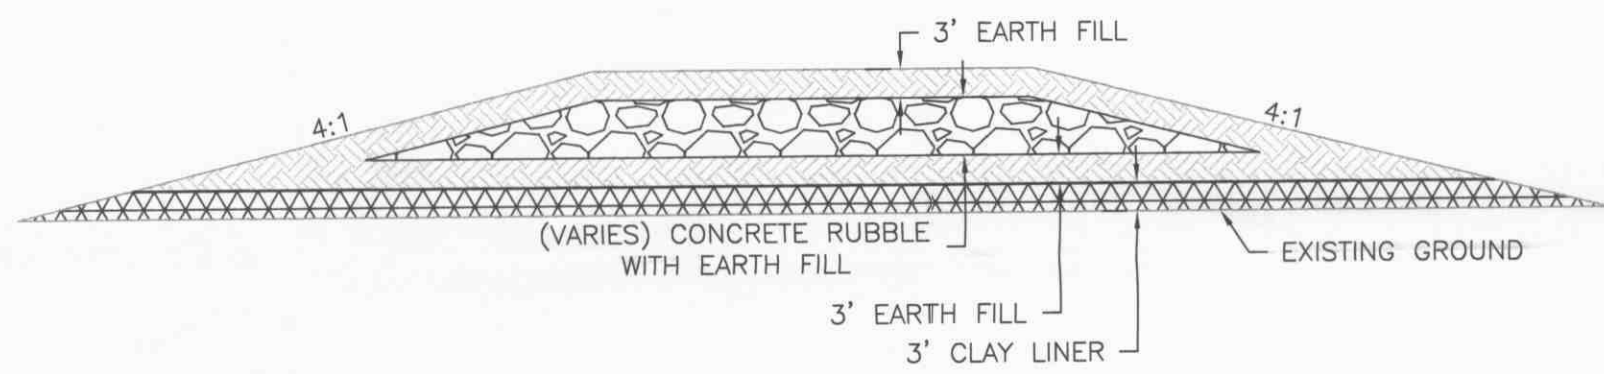

TYPICAL CROSS SECTION B-B'
NTS

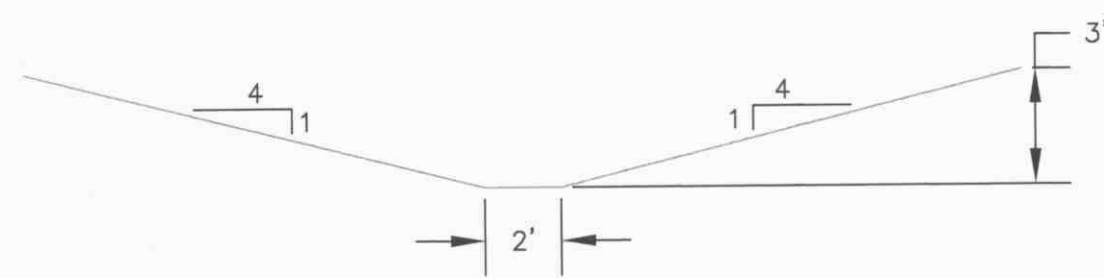


TYPICAL DITCH CROSS SECTION
NTS



Permit #: M-1977-208 Confidential?: N
Class: REVISOR Type-Seq.: TR-2
From: CEMEX, Inc. To: DMG
Doc. Name: On-Site Disposal Cell Map
Doc. Date (if no date stamp): 5/13/03
First Copy Received Second Copy 6/6/03

RECEIVED
MAY 29 2003
Division of Minerals and Geology

LEGEND	
	PAVED ROAD
	UN-PAVED ROAD
	DITCH/WATERWAY
	EXISTING INDEX CONTOUR
	EXISTING INTERMEDIATE CONTOUR
	EXISTING INTERMEDIATE CONTOUR
	PROPOSED DISPOSAL AREA
	DIVERSION DITCH

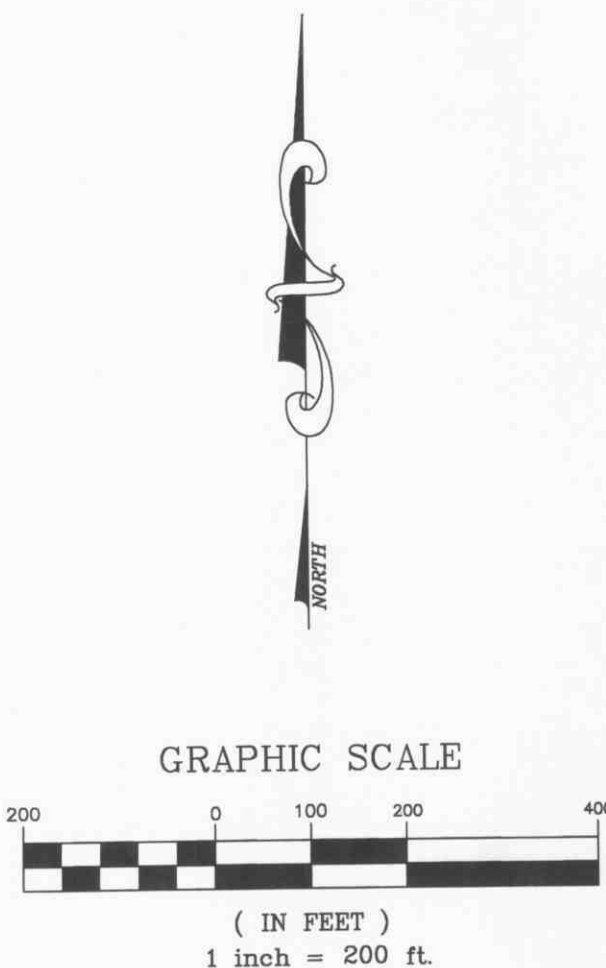

SEED MIX SCHEDULE	
MIX	SPECIFICATION
NATIVE GRASSES	NATIVE GRASSES WILL BE USED TO RESEED ALL DISTURBED AREAS AND SERVE AS GROUND COVER FOR ALL LANDSCAPED OPEN SPACE. SHORTER GRASSES WILL BE USED TO EMPHASIZE SAFETY AND MAINTENANCE CONCERNS. NATIVE GRASS SEED MIXTURE MAY INCLUDE BUFFALO GRASS (BUCHLOE DACTYLOIDES, 20lb./ac.), SIDE OATS GRAMA (BOUTELOUA CURTIPENDULA, 10lb./ac.), BLUE GRAMA (BOUTELOUA GRACILIS, 20lb./ac.), AND LITTLE BLUESTEM (SCHIZACHYRIUM SCOPARIUM, 15lb./ac.). LISTED SEEDING RATES ARE FOR SINGLE SPECIES STANDS AND SHALL BE ADJUSTED PROPORTIONALLY FOR MIXTURES.

ON-SITE DISPOSAL CELL MAP

BANKS AND GESSO, LLC.
720 KIPLING ST., SUITE 117
LAKEWOOD, COLORADO 80215
(303) 274-4277

CEMEX, INC.
LYONS CEMENT PLANT
5134 UTE HWY.
P.O. BOX 529
LYONS, CO 80540

DMG 112 TECHNICAL REVISION
M-77-208

JOB NO	DATE	SCALE	DRAWN BY	DESIGNED BY	APPROVAL	REV	SHEET
03005	5/13/03	1"=200'	DRF				1 of 1