DATE RECEIVED • OFFICE USE ONLY
RECEIVED
SEP 28 2004
BOULDER COUNTY BUILDING DIV.

Boulder County

BUILDING PERMIT APPLICATION

LAND USE DEPARTMENT• BUILDING SAFETY & INSPECTION SERVICES DIVISION
2045 13th Street• 13th & Spruce Streets• P.O. Box 471• Boulder, Colorado 80306
(303) 441-3925

BUILDING PERMIT NUMBER • OFFICE USE ONLY
BP-04- 1670

EXPIRED

PROJECT LOCATION

PROJECT STREET ADDRESS	LOT	BLOCK	SUBDIVISION
5134 UTE HIGHWAY			
CITY/ZIP CODE	SECTION	TOWNSHIP	RANGE
LYONS COLORADO 80540			

OWNERSHIP

OWNER'S NAME	DAY PHONE NUMBER
CEMEX	823-2100
ADDRESS	NIGHT PHONE NUMBER
5134 UTE HWY	
CITY / STATE / ZIP CODE	FAX NUMBER
LYONS / CO / 80540	823-2104

CONTRACTOR

CONTRACTOR'S NAME	DAY PHONE NUMBER
KRIEGER CONSTRUCTION	776-7613
ADDRESS	NIGHT PHONE NUMBER
111 KIMBARK	
CITY / STATE / ZIP CODE	FAX NUMBER
LONGMONT / CO / 80501	776-9598

DESCRIBE THE PROJECT

STOREROOM MODIFICATIONS
TEMP OFFICE TRAILER - SUPPLIED BY OWNER (CEMEX)
ADDITION TO PERMIT BP-04-1389
ELECTRICAL - INSULATING
PLUMBING - RAMPS

ESTIMATED COST
$ 26,000.00

TYPE OF PROJECT (✓ One)

(01) ☐ New Structure
(02) ☐ Addition To:
(03) ☐ Remodel
(04) ☐ Electrical
(07) ☐ Demolition of Structure
(08) ☐ Change of Use
(09) ☑ Moved-In Structure

TYPE OF STRUCTURE (✓ One)

(01) ☐ One Family Dwelling
(02) ☐ Two Family or Attached Dwelling (Including Townhouse)
(03) ☐ Three & Four Family Dwelling
(04) ☐ Hotel or Motel
(06) ☐ Amusement & Recreation Building
(07) ☐ Church & Other Religious Building
(08) ☑ Industrial Building, Manufacturing Plant, Factory
(09) ☐ Service Station & Repair Garage
(10) ☐ Detached Garage
(12) ☐ Office, Bank, and Professional Building
(13) ☐ School
(14) ☐ Store, Customer Service
(15) ☐ Barn, Storage Shed, Outbuilding
(16) ☐ Mobile/Manufactured Home
(22) ☐ Public Works, Utility Building
(23) ☐ Pool, Hot Tub, Fence, Retaining Wall, Pump (Non-Structure)
☐ Other: _____

	EXISTING	TO BE CONSTRUCTED
HEIGHT OF STRUCTURE	FT.	FT.
NUMBER OF BEDROOMS		
NUMBER OF BATHROOMS		
PROPERTY SIZE:		

COMPLETE ONLY FOR NEW PROJECT

STRUCTURE SIZE	FINISHED	UNFINISHED
BASEMENT	SQ. FT.	SQ. FT.
1ST STORY	SQ. FT.	SQ. FT.
2ND STORY	SQ. FT.	SQ. FT.
3RD STORY	SQ. FT.	SQ. FT.
OTHER STORIES	SQ. FT.	SQ. FT.
GARAGE	SQ. FT.	SQ. FT.
DECK	SQ. FT.	COVERED DECK SQ. FT.

SETBACKS (Distance of Project to Property Lines)

FRONT SETBACK EXISTING	SIDE SETACK EXISTING	SIDE SETACK EXISTING	REAR SETBACK EXISTING
FT.	FT.	FT.	FT.
FRONT SETBACK PROPOSED	SIDE SETBACK PROPOSED	SIDE SETBACK PROPOSED	REAR SETBACK PROPOSED
FT.	FT.	FT.	FT.

WATER SERVICE (✓ One)

☐ INDIVIDUAL WELL
☐ COMMUNITY WELL
☐ N/A
☑ PUBLIC: _____

SEWER SERVICE (✓ One)

☐ SEPTIC TANK
☐ VAULT
☐ N/A
☐ PUBLIC: _____

ELECTRICAL SERVICE (✓ One)

☐ PUBLIC SERVICE COMPANY
☐ UNITED POWER
☐ ESTES PARK
☐ POUDRE VALLEY REA
☐ LONGMONT
☑ N/A

GAS SERVICE (✓ One)

☑ PUBLIC SERVICE COMPANY
☐ PROPANE
☐ N/A
☐ OTHER: _____

ACCESS (✓ One)

☑ EXISTING DRIVEWAY
☐ NEW DRIVEWAY
☐ N/A
☐ OTHER: _____

CERTIFICATION

I hereby certify that the above information is correct and agree to construct this building in accordance with the plot, building plans and specifications submitted herewith, and in strict compliance with all the provisions of the Zoning Ordinance, Building Code. Electrical Code, and Health and Plumbing Regulations of the County of Boulder.

OWNER/AGENT'S SIGNATURE	DATE	TITLE
X [signature]	9-28-04	P. MANAGER

BPA6-99/REV. 12-27-99/CD/BB/WC

This parcel at 005134 UTE HY
is owned by
CEMEX INC
ATT: TAX DEPT
PO BOX 1500
HOUSTON, TX 77251

Its Legal Description is
21-3N-70, 28-3N-70, 29-3N-70 SE 1/4
SE 1/4 20-3N-70 & PT W 1/2 27-3N-70
& E 500 FT OF LESS .19 ACS M/L TO
BOCO & LESS PTS TO US LESS PT TO
HWY DEPT TOTAL 757.85 ACS SPLITS
128969 & 142930 TO HWY DEPT
PROPERTY ADDRESS: 005134 UTE HY
LONGMONT□

EXPIRED

Its GIS Land Area is 37737798 square feet, 866.3406 acres.

It is Parcel Number 120328000001 and this owner has Account Number R0053049.

These owners are taxed in the following:
BOULDER COUNTY GENERAL OPERATING
ST VRAIN RE1J GENERAL OPERATING
NORTHERN COLO WATER CONTRACT OBLIG
ST VRAIN LEFT HAND WATER GENERAL OPER
HYGIENE FIRE DIST GENERAL OPERATING
LONGMONT CONSERVATION DIST GEN OPER
RTD GENERAL OPERATING

Recent deeds for this parcel:
SW at Reception Number 613148 from to for $42000000 on 4/5/1984
QD at Reception Number 1284471 from to for $0 on 4/21/1993
QD at Reception Number 1284471 from to for $0 on 4/21/1993
SW at Reception Number 1432787 from to for $818000 on 6/1/1994
SW at Reception Number 1432787 from to for $818000 on 6/1/1994
SW at Reception Number 1477357 from to for $0 on 11/7/1994
SW at Reception Number 1477357 from to for $0 on 11/7/1994
SW at Reception Number 1756839 from to for $0 on 12/19/1997

NOTE: Because of small inconsistencies in the locations of lines in the map layers, GIS searches may return data from adjacent polygons even though no overlap is visible on the screen. Display the layers in question to resolve any uncertainty.

Permits for this Parcel:
BP-00-872 ELEC FOR WATER PUMP MAIN PLANT

BP-00-1207 CELLULAR ANTENNA SITES

BP-01-494 SIGN REPLACEMENT

BP-01-2179 INSTALL PCS EQUIP & ANTENNAS ON CEMENT PLANT - FINAL INSPECTION COMPLETED ON 2/11/02 BY J.H.

BP-65-8040 EARTHWORK & FOUNDATIONS FOR CEMENT PLANT

BP-66-9358 NEW RES

BP-67-10137 SUPERSTRUCTURE FOR CEMENT PLANT

BP-70-13156 SIGN FOR CEMENT PLANT

BP-73-18153 COAL STORAGE SILO

EXPIRED

BP-75-19820 SHOP

BP-78-22476 REPAIR OVERHEAD DOOR

BP-78-23408 ELEC FOR NEW PUMP

BP-79-324 ENLARGE STORAGE BLDG

BP-79-463 COMBUSTION CHANGE/KILN

BP-79-513 5 CONSTRUCTION MOHOS

BP-80-619 ELEC FOR MOBILE HOME

BP-81-71 elec for traffic light

BP-84-182 FOUNDATION FOR CLINKER COOLER

BP-90-230 REPAIR GAS LEAK/NEW WATERLINE

BP-94-2403 DEMO-DWELLING,BARN,GAR,SHED,SILO

BP-94-2566 OFFICE TRAILER

BP-97-1785 TELECOM SITE/WALL MOUNTED

Dockets for this Parcel:
PAC-03-032 CEMEX INC.

SPR-97-160 SOUTHDOWN INC / US WEST NEWVECTOR G

SU-01-08 QWEST WIRELESS (Cemex Cement Plant)

SU-88-21 LYONS RUBBER RECYCLING CENTER

SU-96-18 WESTERN MOBILE BOULDER, INC.

EXPIRED

Assessor land and structure listing for this parcel: XFOB = Extra Feature or Building

ACCOUNTNO	MODEL	OCCURANCE	ATRIBTYPE	ATRIBDESC
R0053049	COMML	1.0	ABSTRACT_CODE	MANUFCTRNG/PROCESN(IMPS
R0053049	COMML	1.0	CONST	TEES/TILT
R0053049	COMML	1.0	DESIGN	MASONRY
R0053049	COMML	1.0	HEIGHT	42 - HEIGHT
R0053049	COMML	1.0	STORIES	1 - STORIES
R0053049	LAND_COMML	1.0	ABSTRACT_CODE	REFINING/MILLING-LANI
R0053049	LAND_COMML	100.0	ABSTRACT_CODE	MANUFCTNG/PROCESNG- LAND
R0053049	LAND_COMML	101.0	ABSTRACT_CODE	VACANT IND LOTS
R0053049	LAND_MT	3.0	ABSTRACT_CODE	SINGLE FAM.RES.-LAND
R0053049	RESMT	3.0	ABSTRACT_CODE	SINGLE FAM RES IMPROVEMENTS
R0053049	RESMT	3.0	BATH_F	1 - BATH_FULL
R0053049	RESMT	3.0	CONST	FRAME
R0053049	RESMT	3.0	DESIGN	1 STORY - RANCH
R0053049	RESMT	3.0	YEAR	1960 - YEAR
R0053049	XFOB	301.0	ABSTRACT_CODE	SINGLE FAM RES IMPROVEMENTS
R0053049	XFOB	301.0	XFOB_CODE	BARN-D,LOW 15 YRS
R0053049	XFOB	301.0	YEAR	1960 - YEAR

Assessor land and structure areas or counts for this parcel: Correlate with land and structures by Model+Occurance for each Account.

ACCOUNTNO	MODEL	OCCURANCE	SUB_CODE	AREA_ACT
R0053049	COMML	1.0	4940	181928.0
R0053049	LAND_COMML	1.0	SQFT	1829520.0
R0053049	LAND_COMML	100.0	SQFT	1873080.0
R0053049	LAND_COMML	101.0	ACRES	232.0
R0053049	LAND_MT	3.0	ACRES	440.85
R0053049	RESMT	3.0	AREA_FIRST	1508.0
R0053049	RESMT	3.0	B_SUB_UNF	1508.0
R0053049	RESMT	3.0	POR_PORCH	260.0
R0053049	XFOB	301.0	XFOB_UNITS	840.0

BUILDING PERMIT APPLICATION REVIEW FORM

FILE NUMBER
04-1670

PROJECT LOCATION

PROJECT ADDRESS			UNIT	CITY	ZIP CODE
5134 Ute Hwy				LY	80540
LOT	**BLOCK**	**SUBDIVISION NAME**	**SECTION**	**TOWNSHIP**	**RANGE**
			28	3N	70

OWNER'S NAME: Cemex Inc

OCCUPANCY GROUP	TYPE OF CONSTRUCTION	VALUATION
		$


EXPIRED

STRUCTURE DATA	EXISTING	TO BE CONSTRUCTED
Height of Structure	FT	FT
Number of Stories		
Number of Dwellings		
Number of Bedrooms		
Number of Bathrooms		

Water	
Electric	
Sewer	
Gas	
Access	

STRUCTURE SIZE (For new construction & additions only)	FINISHED	UNFINISHED
Basement	SQ. FT.	SQ. FT.
1st Floor		
2nd Floor		
All other Floors		
Deck		
Covered Roof		
Garage		
Totals		
Snowload		
Windload		

Tax I.D.#	
Parcel #	
Deed #	
Tax Area	
Service Area	
School District	
Fire District	
Property Size	ACRE(S)
Zoning (1)	ACRE(S)
Zoning (2)	ACRE(S)

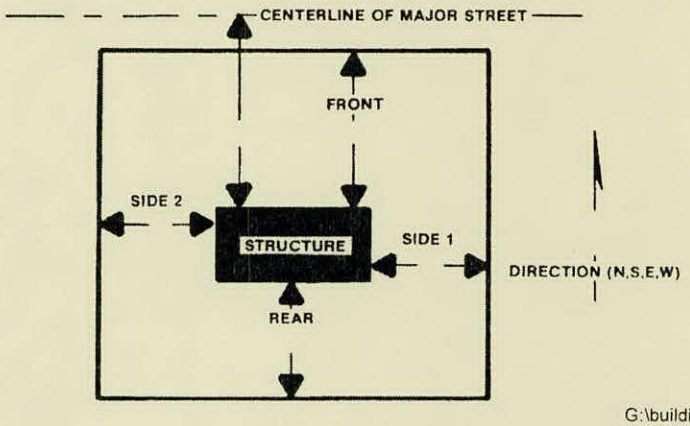

Building Permit Routing Form

BP-04- 1670

Permit tech D

RECEIVED 2004 BOULDER COUNTY BUILDING DIV.

RECEIVED SEP 28 2004 BOULDER COUNTY BUILDING DIV.

Owner Name Cemex

Project Description Store room modifications

Fees:

Application Deposit	$25.000 Ck# 12095	*Subtotal*	$
Building Division Fees	$	*Less deposit*	- $
Investigation Fee	$	***BALANCE DUE:***	***$***
Access Fee	$		
Escrow	$	*Escrow* $	
Floodplain Fee	$		

EXPIRED

Permit tech comments:

Zoning Approval

end

SPR req'd____ zoning affidavit____ height survey req'd____ setback survey req'd____

Comments:

approvedby/date

Historic Approval

Comments:


approvedby/date

Site Plan Review


Site Plan Review #_____ notified owner/date:_____ notified contractor/date:_____

Comments:

approvedby/date

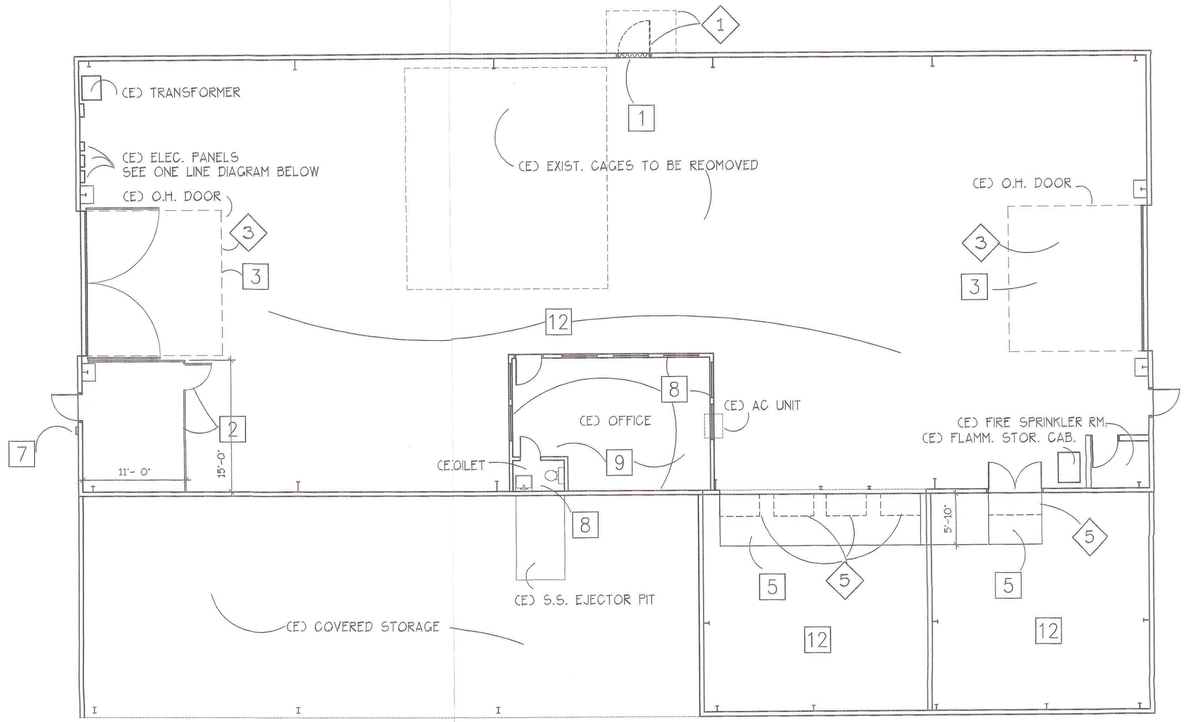


1 FLOOR PLAN
SCALE: 1/8" = 1'-0"

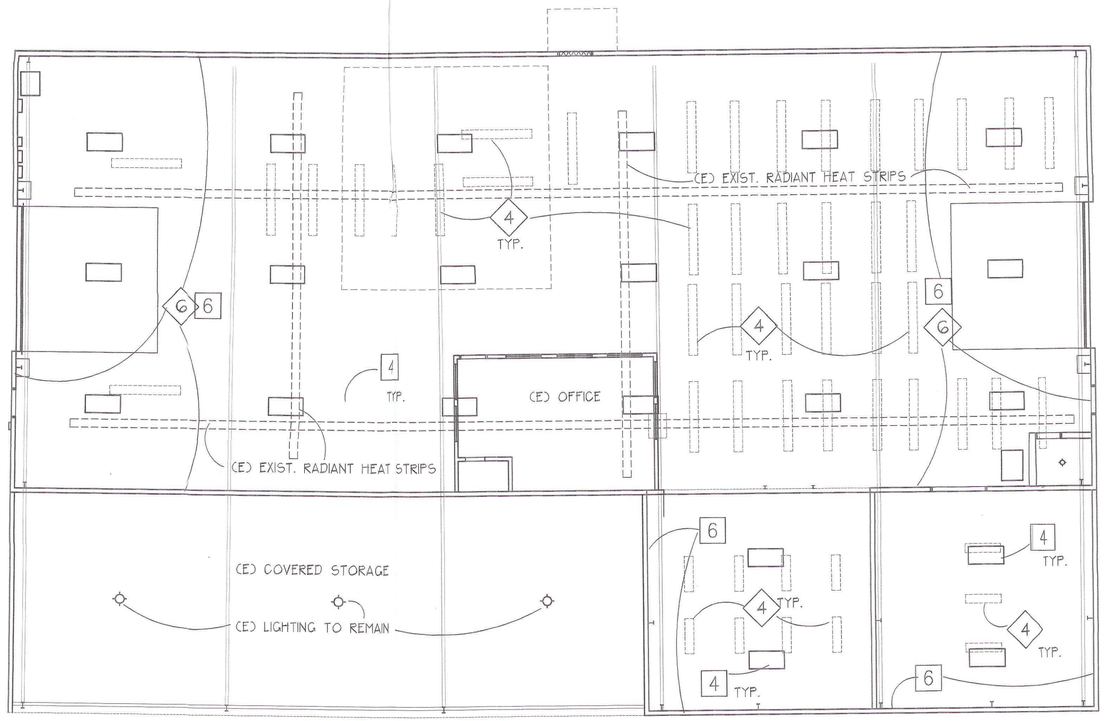

2 REFLECTED CEILING PLAN
SCALE: 1/8" = 1'-0"

SITE PLAN NOTES

1. RUN NEW POWER FROM EXIST. PANEL INSIDE STORE ROOM. SEEONE-LINE DIAGRAM BELOW.
2. RELOCATE EXISTING FENCE AND GATE.
3. RUN 4 IN. S.S. DRAIN LINE FROM NEW SERVICE TO EXIST. PRESSURIZED EJECTOR PIT. CHANG ON SIDE OF BLDG UNDER OVERHANG).
4. RUN 3/4 IN. TYPE K WATER SERVICE FROM EXISTING TOILET RM. TO NEW SERVICE. HANG FROM STRUCTURE ABOVE.
5. SAWCUT EXIST. CONCRETE DRIVE AND BURY 3/4 IN. WATER + SEWER LINES AT 4'-0" DEPTH. FOUR 4" CONC. SLAB BACK FLUSH.
6. PROVIDE HEAT TAPE AT WATER LINE IN TRAILER CRAWLSPACE.

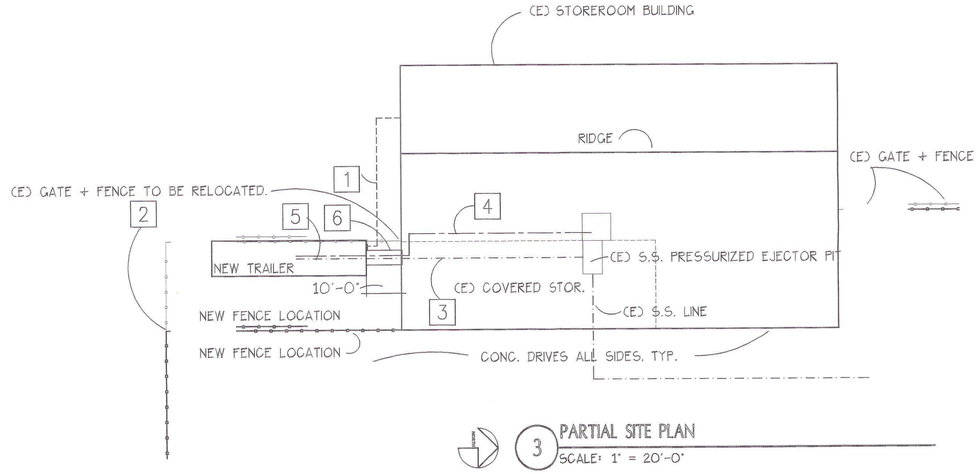


3 PARTIAL SITE PLAN
SCALE: 1" = 20'-0"

PLAN DEMOLITION NOTES

1. REMOVE DOOR. DOOR FRAME AND EXTERIOR CANOPY
2. NOT USED.
3. REMOVE EXIST. OVERHEAD DOORS.
4. REMOVE ALL EXISTING OVERHEAD FLUOR. LIGHTING
5. REMOVE EXISTING RAMPS
6. REMOVE EXISTING INTERIOR SPRAY INSULATION ON EXIST. EXTERIOR PURLINS.

PLAN NEW CONSTRUCTION NOTES

1. FILL DOOR OPENING WITH NEW MTL. STUD WALL + EXT. WALL PANEL TO MATCH EXISTING.
2. INSTALL NEW 1 1 /2 INCH GUARDRAIL AT 42 IN. AFF + GATE AS SHOWN.
   PROVIDE HORIZ. INTERMIEDIATE RAILS AT 12 IN. O.C. FROM TOP + VERTICALS AT 6'-0 O.C..
3. INSTALL NEW OVERHEAD DOORS.
4. INSTALL NEW OVERHEAD LIGHTING - WESTINGHOUSE HIGH EFF. HIGH BAY FLUORESCENTS.
5. PROVIDE NEW CONCRETE ACCESS RAMPS AT A SLOPE OF 1 IN 10
   SAWCUT EXIST. SLAB AS REQ'D TO PROVIDE A MIN. OF A 4 IN. CONC. POUR.
6. REINSULATE ALL EXTERIOR WALLS AND ROOF SURFACES. PROVIDE R-19 BATTS AT WALLS + R-30 BATTS AT ROOF.
   PROVIDE INTERIOR MOISTURE BARRIER SHEATHING AT INNER FACE. MAIN STOREROOM ROOF INSULATION TO REMAIN.
7. INSTALLSECURITY SYSTEM WITH CARD READER AT SOUTH MAN DOOR.
8. REPAINT INSIDE OF OFFICE + TOILET. FILL AND TEXTURE AS REQ'D PROR TO PAINT. OWNER TO SELECT PAINT COLOR.
9. INSTALL NEW CARPET INSIDE OF OFFICE. COORD. COLOR + STYLE W/ OWNER.
10. NOT USED
11. ASSIST OWNER IN RELOCATION OF ALL PARTS. SHELVING + HARDWARE TO NEW LOCATIONS AS DIRECTED BY OWNER.
12. POWER WASH. REPAIR AND PAINT CONCRETE FLOORS.

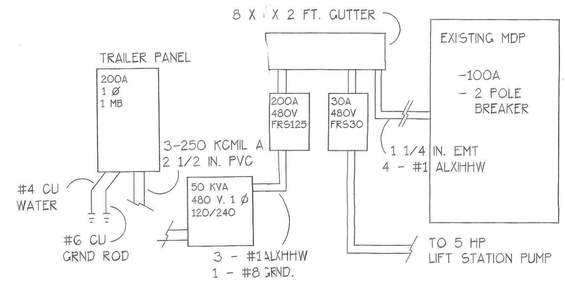

4 ONE-INE DIAGRAM
SCALE NO SCALE

CMEX

LYONS PLANT STOREROOM MODIFICATIONS

5134 UTE HIGHWAY
LYONS, COLORADO
80540

PROJECT NO. P2004-14

HSA ARCHITECTS, INC
Architects & Planners
2055 Eagle Avenue
Superior, Co. 80027
Tel 303.554.9587
Fax 303.554.9587
jmsalisbury@msn.com
www.hsarchitects.net

STATE OF COLORADO
JAMES M. SALISBURY
202191
LICENSED ARCHITECT

ISSUE RECORD
FINAL REVIEW 24SEP04
PERMIT/CONST. 27SEP04

DRAWING TITLE
SITE & FLOOR PLANS
REFLECTED CEILING PLAN
ELECTRICAL ONE-LINE DIAGRAI

CADD FILE
\A101-001.DWG

SCALE
AS NOTED

DRAWING No.
A1.01

DATE
27 SEP 2004

EXPIRED

COUNTY COPY

OU-1670
Comp

RECEIVED
SEP 28 2004
BOULDER COUNTY
BUILDING DIV

RECEIVED
SEP 28 2004
BOULDER COUNTY
BUILDING DIV

COUNTY COPY