SHEET 2 OF 2

DOWE FLATS ESTATES SUBDIVISION EXEMPTION PLAT

A SUBDIVISON EXEMPTION LOCATED IN THE S1/2 OF SECTION 16 AND IN THE N1/2 OF SECTION 21, ALL IN T3N, R70W OF THE 6TH P.M., COUNTY OF BOULDER, STATE OF COLORADO

TOTAL AREA = 153.150 ACRES

NOTE: DITCH COMPANIES RETAIN THE RIGHT TO ENTER THE PROPERTY AND MAINTAIN ALL DITCHES.

LEGEND

- ....DITCH FLOWLINE
- ....FENCE
- ....ALIQUOT LINE
- ....EASEMENT LINE
- ....CENTERLINE
- ....ALIQUOT CORNER
- ....PROPOSED CENTERLINE EASEMENT CORNER
- ....SET #5 REBAR WITH ALUMINUM CAP MARKED "D.B. & CO PLS 23529"
- ....WITNESS CORNER
- ....BOX CULVERT

COLORADO REGISTERED PROFESSIONAL LAND SURVEYOR
WILLIAM K. WRIGHT
23529

William K. Wright

S:\55143-8\51438p101.dwg, 03/26/2004 02:35:07 PM, Drexel, Barrell & Co.sds

P-60 F-3 #17 (2 of 2)

B59-100A

SHEET 1 OF 2

DOWE FLATS ESTATES SUBDIVISION EXEMPTION PLAT

A SUBDIVISON EXEMPTION LOCATED IN THE S1/2 OF SECTION 16 AND IN THE N1/2 OF SECTION 21, ALL IN T3N, R70W OF THE 6TH P.M., COUNTY OF BOULDER, STATE OF COLORADO

TOTAL AREA = 153.150 ACRES

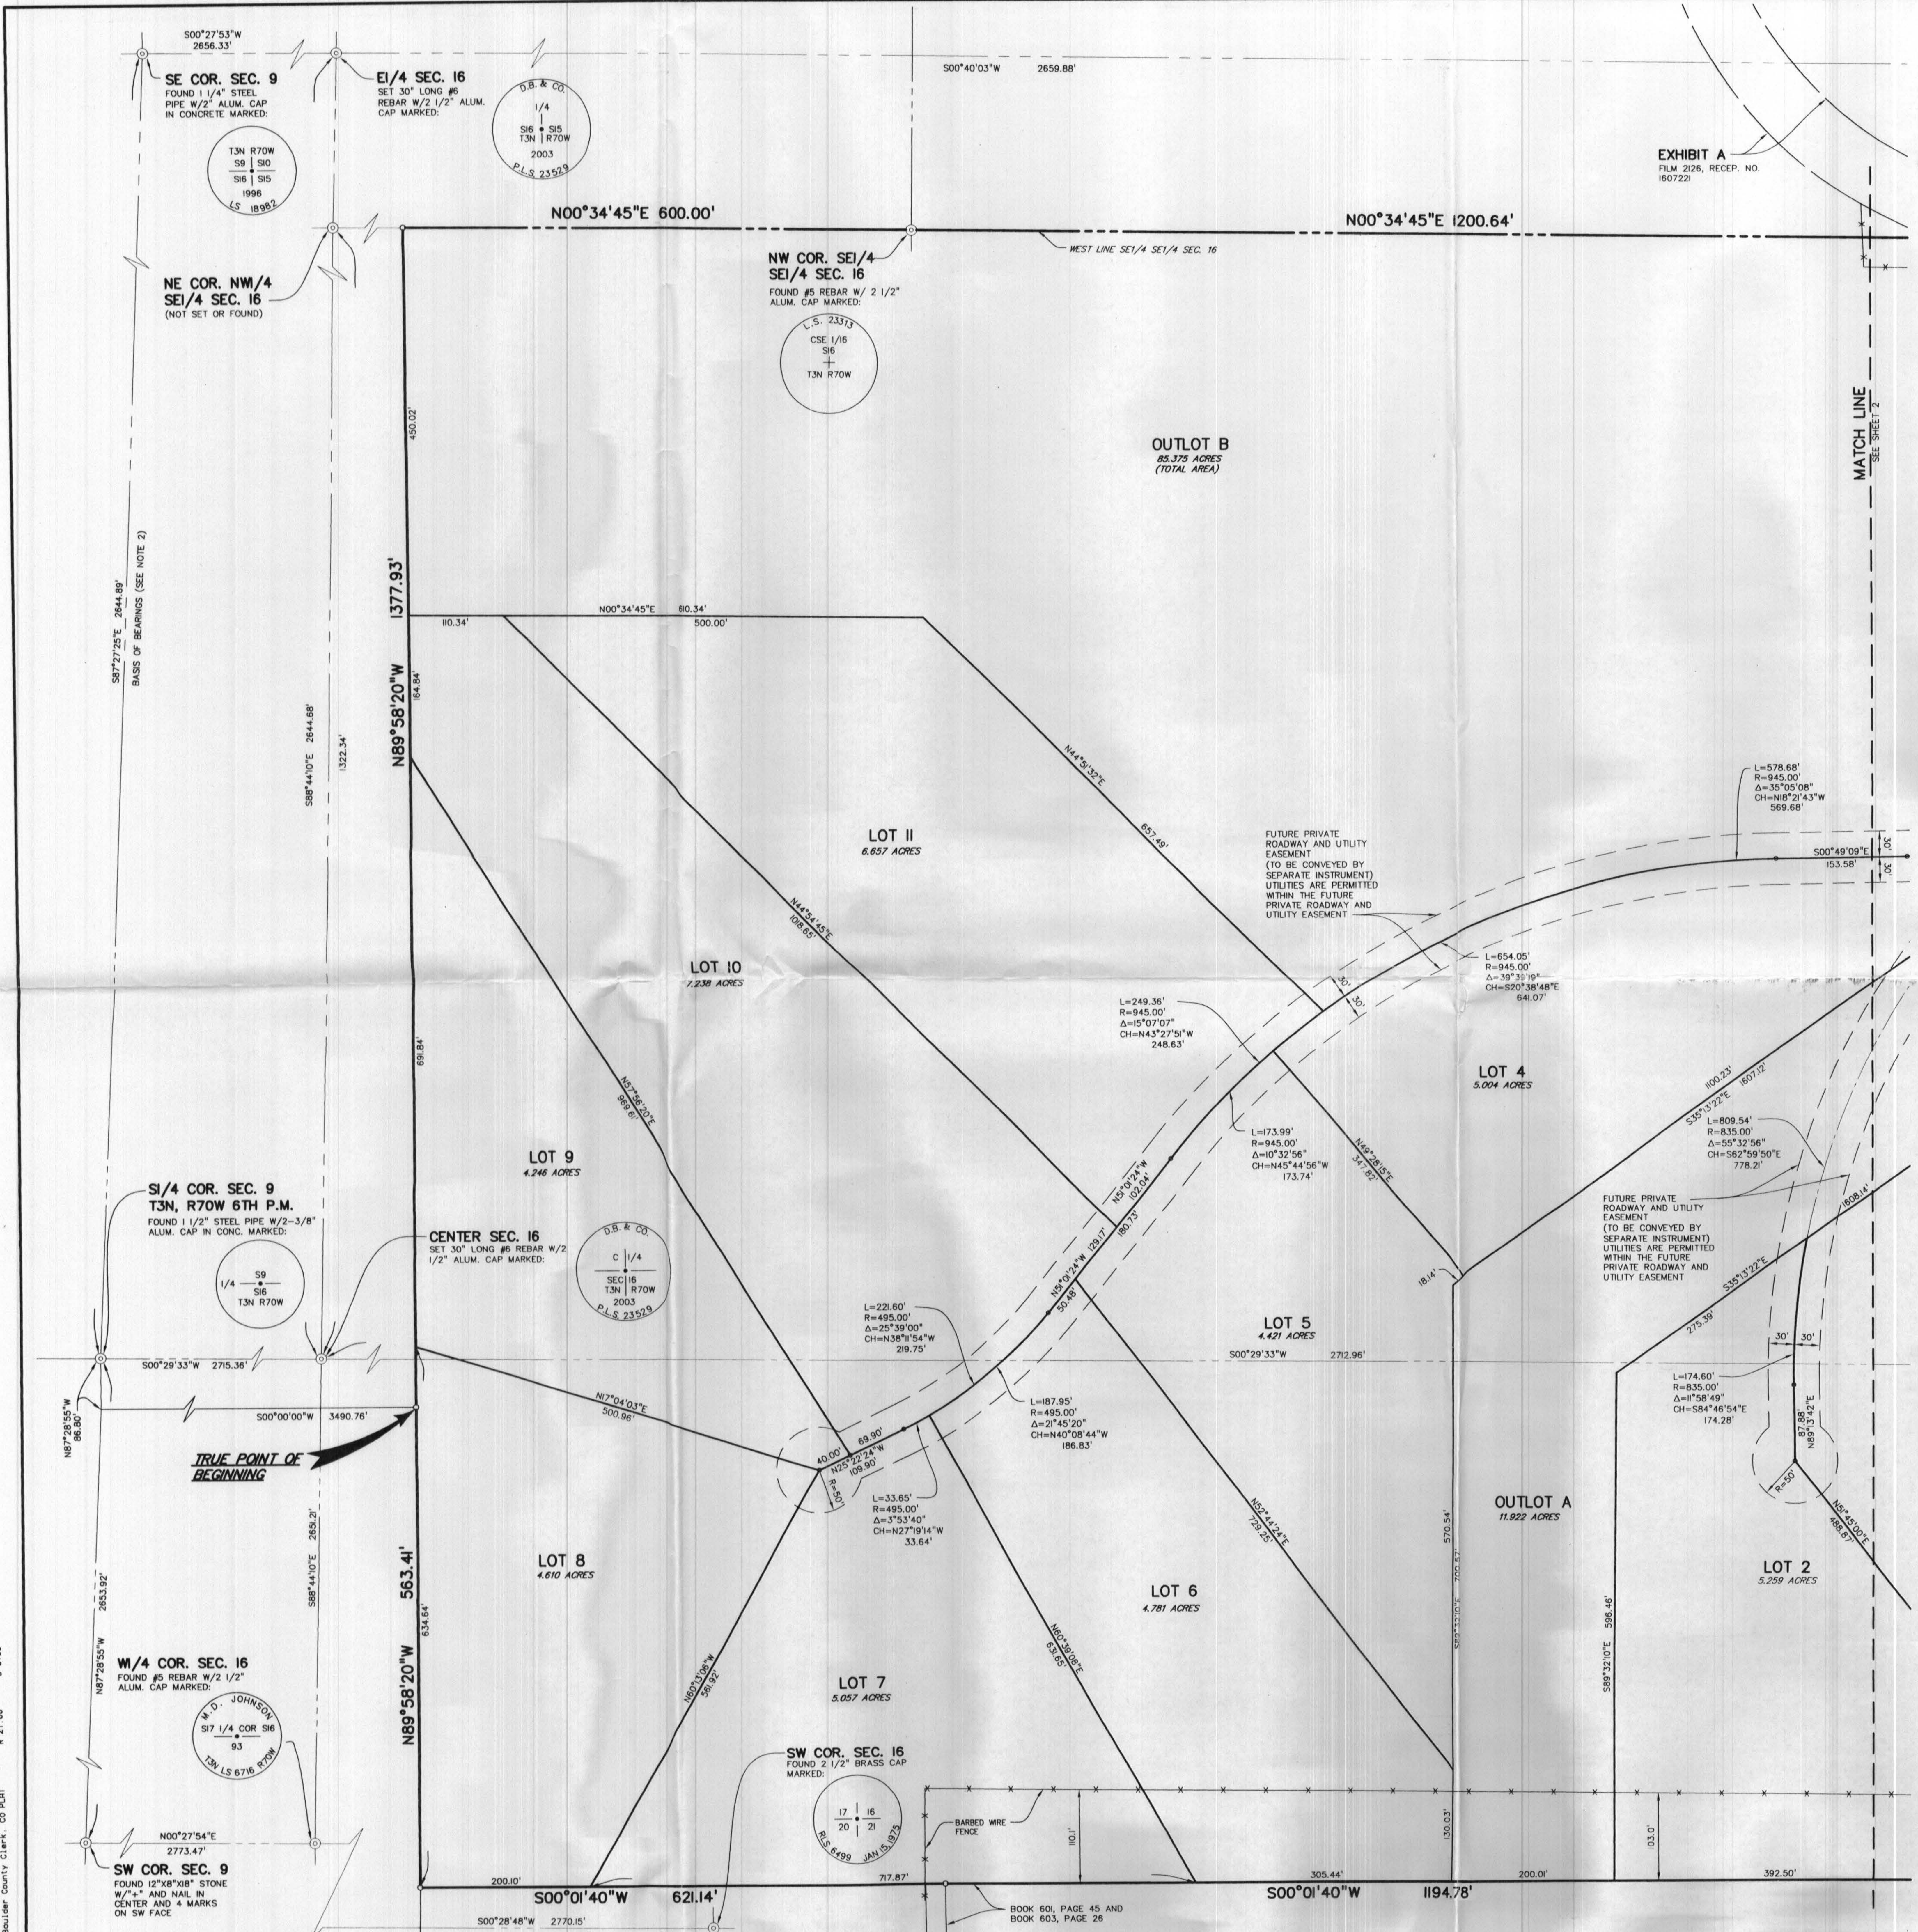
S00°27'53"W
2656.33'
SE COR. SEC. 9
FOUND 1 1/4" STEEL PIPE W/2" ALUM. CAP IN CONCRETE MARKED:
T3N R70W S9 S10 S16 S15 1996 LS 18982
E1/4 SEC. 16
SET 30" LONG #6 REBAR W/2 1/2" ALUM. CAP MARKED:
D.B. & CO. 1/4 S16 S15 T3N R70W 2003 P.L.S. 23529
S00°40'03"W 2659.88'
EXHIBIT A
FILM 2126, RECEP. NO. 1607221
N00°34'45"E 600.00'
N00°34'45"E 1200.64'
WEST LINE SE1/4 SE1/4 SEC. 16
NE COR. NW1/4 SE1/4 SEC. 16
(NOT SET OR FOUND)
NW COR. SE1/4 SE1/4 SEC. 16
FOUND #5 REBAR W/ 2 1/2" ALUM. CAP MARKED:
L.S. 23313 CSE 1/16 S16 T3N R70W
450.02'
OUTLOT B
85.375 ACRES
(TOTAL AREA)
MATCH LINE
SEE SHEET 2
S87°27'25"E 2644.89'
BASIS OF BEARINGS (SEE NOTE 2)
S88°44'10"E 2644.68'
1322.34'
N89°58'20"W 1377.93'
N00°34'45"E 610.34'
110.34'
500.00'
164.84'
N44°54'45"E
1018.65'
N44°51'32"E
657.49'
LOT 11
6.657 ACRES
LOT 10
7.238 ACRES
N57°56'20"E
969.61'
691.84'
LOT 9
4.246 ACRES
FUTURE PRIVATE ROADWAY AND UTILITY EASEMENT (TO BE CONVEYED BY SEPARATE INSTRUMENT) UTILITIES ARE PERMITTED WITHIN THE FUTURE PRIVATE ROADWAY AND UTILITY EASEMENT
L=578.68' R=945.00' Δ=35°05'08" CH=N18°21'43"W 569.68'
S00°49'09"E 153.58'
30'
L=654.05' R=945.00' Δ=39°39'19" CH=S20°38'48"E 641.07'
L=249.36' R=945.00' Δ=15°07'07" CH=N43°27'51"W 248.63'
L=173.99' R=945.00' Δ=10°32'56" CH=N45°44'56"W 173.74'
N49°28'15"E 347.82'
N51°01'24"W 102.04'
180.73'
N51°01'24"W 129.17'
50.48'
LOT 4
5.004 ACRES
S35°13'22"E 1100.23' 1607.12'
L=809.54' R=835.00' Δ=55°32'56" CH=S62°59'50"E 778.21'
1608.14'
S35°13'22"E
275.39'
18.14'
LOT 5
4.421 ACRES
S00°29'33"W 2712.96'
SI/4 COR. SEC. 9
T3N, R70W 6TH P.M.
FOUND 1 1/2" STEEL PIPE W/2-3/8" ALUM. CAP IN CONC. MARKED:
S9 1/4 S16 T3N R70W
CENTER SEC. 16
SET 30" LONG #6 REBAR W/2 1/2" ALUM. CAP MARKED:
D.B. & CO. C 1/4 SEC 16 T3N R70W 2003 P.L.S. 23529
S00°29'33"W 2715.36'
N87°28'55"W 86.80'
S00°00'00"W 3490.76'
TRUE POINT OF BEGINNING
N17°04'03"E 500.96'
L=221.60' R=495.00' Δ=25°39'00" CH=N38°11'54"W 219.75'
40.00'
69.90'
N25°22'24"W 109.90'
R=50'
L=33.65' R=495.00' Δ=3°53'40" CH=N27°19'14"W 33.64'
L=187.95' R=495.00' Δ=21°45'20" CH=N40°08'44"W 186.83'
LOT 8
4.610 ACRES
N89°58'20"W 563.41'
634.64'
S88°44'10"E 2651.21'
N87°28'55"W 2653.92'
W1/4 COR. SEC. 16
FOUND #5 REBAR W/2 1/2" ALUM. CAP MARKED:
M.D. JOHNSON S17 1/4 COR S16 93 T3N LS 6716 R70W
N60°13'06"W 561.92'
LOT 7
5.057 ACRES
N52°44'24"E 729.25'
LOT 6
4.781 ACRES
N60°39'08"E 631.65'
570.54'
S89°32'10"E 700.57'
OUTLOT A
11.922 ACRES
S89°32'10"E 596.46'
L=174.60' R=835.00' Δ=11°58'49" CH=S84°46'54"E 174.28'
87.88'
N89°13'42"E
N51°45'00"E 488.87'
LOT 2
5.259 ACRES
N00°27'54"E 2773.47'
SW COR. SEC. 9
FOUND 12"X8"X18" STONE W/"+" AND NAIL IN CENTER AND 4 MARKS ON SW FACE
SW COR. SEC. 16
FOUND 2 1/2" BRASS CAP MARKED:
17 16 20 21 RLS 6499 JAN 15, 1975
BARBED WIRE FENCE
110.1'
130.03'
103.0'
200.10'
717.87'
S00°01'40"W 621.14'
305.44'
S00°01'40"W 1194.78'
200.01'
392.50'
S00°28'48"W 2770.15'
BOOK 601, PAGE 45 AND BOOK 603, PAGE 26

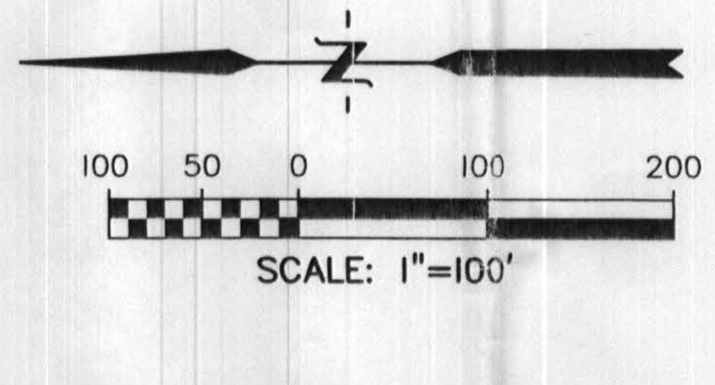

LEGAL DESCRIPTION

A TRACT OF LAND LOCATED IN THE S1/2 OF SECTION 16 AND IN THE N1/2 OF SECTION 21, ALL IN T3N, R70W OF THE 6TH P.M., BOULDER COUNTY, COLORADO, DESCRIBED AS FOLLOWS:

COMMENCING AT THE S1/4 CORNER OF SECTION 9, T3N, R70W OF THE 6TH P.M., FROM WHICH THE SOUTHEAST CORNER OF SAID SECTION 9 BEARS S87°27'25"E, 2644.89 FEET, THENCE N87°28'55"W, 86.80 FEET ALONG THE SOUTH LINE OF THE SW1/4 OF SAID SECTION 9; THENCE S00°00'00"W, 3490.76 FEET TO THE TRUE POINT OF BEGINNING;

THENCE N89°58'20"W, 563.41 FEET TO THE EAST LINE EXTENDED NORTHERLY OF THAT TRACT OF LAND AS DESCRIBED IN WARRANTY DEED RECORDED IN BOOK 601 AT PAGE 45 OF THE RECORDS OF BOULDER COUNTY, COLORADO AND AS DESCRIBED IN QUIT CLAIM DEED RECORDED IN BOOK 603 AT PAGE 26 OF THE RECORDS OF BOULDER COUNTY, COLORADO;

THENCE S00°01'40"W, 621.14 FEET ALONG THE EAST LINE EXTENDED NORTHERLY OF THAT TRACT OF LAND AS DESCRIBED IN SAID BOOK 601 AT PAGE 45 AND IN SAID BOOK 603 AT PAGE 26 TO THE NORTHEAST CORNER THEREOF;

THENCE S00°01'40"W, 1194.78 FEET ALONG THE EAST LINE OF THAT TRACT OF LAND AS DESCRIBED IN SAID BOOK 601 AT PAGE 45 AND IN SAID BOOK 603 AT PAGE 26 TO THE APPROXIMATE SOUTHERLY BANK OF THE SUPPLY DITCH AND THE NORTHERLY LINE OF THAT TRACT OF LAND AS DESCRIBED IN WARRANTY DEED RECORDED IN BOOK 584 AT PAGE 231 OF THE RECORDS OF BOULDER COUNTY, COLORADO;

THENCE S34°07'46"E, 151.34 FEET ALONG THE APPROXIMATE SOUTHERLY BANK OF SAID SUPPLY DITCH AND ALONG THE NORTHERLY LINE OF THAT TRACT OF LAND AS DESCRIBED IN SAID BOOK 584 AT PAGE 231 TO THE SOUTH LINE OF THE SW1/4 OF SAID SECTION 16;

THENCE S89°58'20"E, 25.21 FEET ALONG THE SOUTH LINE OF THE SW1/4 OF SAID SECTION 16 TO THE WEST LINE OF THE EAST 30 ACRES OF THE NW1/4 OF SAID SECTION 21;

THENCE S00°29'15"W, 2101.82 FEET ALONG THE WEST LINE OF THE EAST 30 ACRES OF THE NW1/4 OF SAID SECTION 21 TO THE NORTHEASTERLY RIGHT-OF-WAY LINE OF COLORADO STATE HIGHWAY NO. 66;

THENCE S63°32'37"E, 497.37 FEET ALONG THE NORTHEASTERLY RIGHT-OF-WAY LINE OF SAID COLORADO STATE HIGHWAY NO. 66 TO THE NORTHWESTERLY LINE OF THAT TRACT OF LAND AS DESCRIBED IN WARRANTY DEED RECORDED IN BOOK 70 AT PAGE 162 OF THE RECORDS OF BOULDER COUNTY, COLORADO;

THENCE N27°55'26"E, 102.24 FEET ALONG THE NORTHWESTERLY LINE OF THAT TRACT OF LAND AS DESCRIBED IN SAID BOOK 70 AT PAGE 162 TO THE NORTH-SOUTH CENTERLINE OF SAID SECTION 21;

THENCE N00°29'15"E, 645.17 FEET ALONG THE NORTH-SOUTH CENTERLINE OF SAID SECTION 21 TO THE SOUTH LINE OF THE NORTH 265.00 FEET OF THE NW1/4 OF THE SW1/4 OF THE NE1/4 OF SAID SECTION 21;

THENCE S89°46'29"E, 330.00 FEET ALONG THE SOUTH LINE OF THE NORTH 265.00 FEET OF THE NW1/4 OF THE SW1/4 OF THE NE1/4 OF SAID SECTION 21 TO THE EAST LINE OF THE WEST 330.00 FEET OF THE NW1/4 OF THE SW1/4 OF THE NE1/4 OF SAID SECTION 21;

THENCE N00°29'15"E, 265.00 FEET ALONG THE EAST LINE OF THE WEST 330.00 FEET OF THE NW1/4 OF THE SW1/4 OF THE NE1/4 OF SAID SECTION 21 TO THE SOUTH LINE OF THE NW1/4 OF THE NE1/4 OF SAID SECTION 21;

THENCE S89°46'29"E, 328.81 FEET ALONG THE SOUTH LINE OF THE NW1/4 OF THE NE1/4 OF SAID SECTION 21 TO THE SOUTHEAST CORNER OF THE W1/2 OF THE NW1/4 OF THE NE1/4 OF SAID SECTION 21;

THENCE S89°46'29"E, 658.81 FEET ALONG THE SOUTH LINE OF THE NW1/4 OF THE NE1/4 OF SAID SECTION 21 TO THE SOUTHEAST CORNER THEREOF;

THENCE N00°30'40"E, 1314.15 FEET ALONG THE EAST LINE OF THE NW1/4 OF THE NE1/4 OF SAID SECTION 21 TO THE SOUTH LINE OF BOULDER COUNTY ROAD NO. 47 AS DESCRIBED IN EXHIBIT A IN SPECIAL WARRANTY DEED RECORDED ON FILM 2126 AS RECEPTION NO. 1607221 OF THE RECORDS OF BOULDER COUNTY, COLORADO;

THENCE N89°37'04"W, 45.93 FEET ALONG THE SOUTHERLY LINE OF SAID BOULDER COUNTY ROAD NO. 47 TO THE SOUTHWEST CORNER THEREOF;

THENCE NORTHEASTERLY, 160.80 FEET ALONG THE WESTERLY LINE OF SAID BOULDER COUNTY ROAD NO. 47 AND ALONG THE ARC OF A CURVE CONCAVE TO THE SOUTHEAST TO THE WEST LINE OF THE SE1/4 OF THE SE1/4 OF SAID SECTION 16, SAID ARC HAVING A RADIUS OF 815.00 FEET, A CENTRAL ANGLE OF 11°18'16" AND BEING SUBTENDED BY A CHORD THAT BEARS N17°11'48"E, 160.54 FEET;

THENCE N00°34'45"E, 1200.64 FEET ALONG THE WEST LINE OF THE SE1/4 OF THE SE1/4 OF SAID SECTION 16 TO THE NORTHWEST CORNER THEREOF;

THENCE N00°34'45"E, 600.00 FEET ALONG THE WEST LINE EXTENDED NORTHERLY OF THE SE1/4 OF THE SE1/4 OF SAID SECTION 16 TO A POINT FROM WHICH THE TRUE POINT OF BEGINNING BEARS N89°58'20"W;

THENCE N89°58'20"W, 1377.93 FEET TO THE TRUE POINT OF BEGINNING.

SUBJECT TO A RIGHT-OF-WAY FOR BOULDER COUNTY ROAD NO. 47 (NORTH 53RD STREET).

EXCEPTIONS

ALL THAT PORTION OF THE HIGHLAND DITCH LOCATED IN THE W1/2 OF THE NW1/4 OF THE NE1/4 OF SAID SECTION 21.

AREA = 153.150 ACRES, MORE OR LESS (INCLUDING THE HIGHLAND DITCH).

BOULDER COUNTY NOTES AND CONDITIONS

I. BEFORE THE COUNTY ISSUES ANY CONSTRUCTION PERMITS OR BUILDING PERMITS FOR DEVELOPMENT ASSOCIATED WITH THE SUBJECT ELEVEN LOTS, THE COUNTY STAFF MUST REVIEW AND APPROVE THE FOLLOWING:

1. COMPLIANCE WITH APPLICABLE REQUIREMENTS AS NOTED IN ARTICLE 7 OF THE LAND USE CODE INCLUDING BUT NOT LIMITED TO: SUFFICIENT WATER SUPPLIES AND SEWAGE DISPOSAL SYSTEMS, SUFFICIENT FIRE PROTECTION, CURRENT ACCESS PERMITS, AND THE LIKE.
2. GRADING CALCULATIONS AND PLAN, PROFILE AND CROSS SECTIONS OF ALL PROPOSED ROADWAYS, INCLUDING A FINAL SOILS AND DRAINAGE REPORT, AND SURFACING AND DRAINAGE DESIGN RECOMMENDATIONS;
3. SPECIFIC LOCATIONS AND DETAILS FOR ALL PROPOSED UTILITY LINES TO SERVICE THE ELEVEN BUILDING SITES;
4. SPECIFIC LOCATIONS AND DIMENSIONS OF ANY PROPOSED PEDESTRIAN PATHS;
5. A UTILITY PLAN PLACING ALL PROPOSED WATER LINES OUTSIDE OF ANY WETLAND AREAS;
6. COVENANTS AND DESIGN GUIDELINES WHICH SHALL BE SUBMITTED FOR REVIEW AND APPROVAL BY THE COUNTY, WITH ALL COVENANTS AND GUIDELINES BEING IN ACCORDANCE WITH THE LAND USE CODE AND INCLUDING REASONABLE INDUSTRY-RECOGNIZED XERISCAPE STANDARDS ON THE DESIGN AND WATERING OF PROPOSED LANDSCAPE AREAS, AND ADDRESSING USES FOR THE OUTLOTS, AND THE LIKE.

IN ADDITION, THE 30-FOOT HEIGHT LIMIT OF THE AGRICULTURAL ZONING DISTRICT APPLIES TO ALL RESIDENTIAL STRUCTURES ON ANY LOT RECOGNIZED BY THE DOCKET.

II. USES AND ACTIVITIES ASSOCIATED WITH THE OUTLOTS SHALL BE CONSISTENT WITH THOSE WHICH ARE *PERMITTED* BY THE TERMS OF ANY CONSERVATION EASEMENT ENCUMBERING THE OUTLOTS AND WHICH ARE PERMITTED BY RIGHT UNDER THE PROVISIONS OF THE LAND USE CODE AND THE AGRICULTURAL ZONING DISTRICT AND OTHERWISE AUTHORIZED BY THE COUNTY IN ACCORDANCE WITH THE PROVISIONS OF THE LAND USE CODE. FORMAL RECREATIONAL TRAILS OR OTHER FORMAL RECREATIONAL USES OF THE OUTLOTS SHALL BE REVIEWED AND APPROVED BY THE COUNTY PRIOR TO IMPLEMENTATION/CONSTRUCTION IN ACCORDANCE WITH PROVISIONS OF THE LAND USE CODE. PARTICULAR CARE AND CONSIDERATION SHALL BE GIVEN TO PRESERVE THE QUALITY AND INTEGRITY OF THE ENVIRONMENTAL RESOURCES AND WILDLIFE HABITAT THAT EXIST ALONG THE IRRIGATION CANALS AND OTHER ENVIRONMENTALLY SENSITIVE AREAS WITHIN THE OUTLOTS.

III. RE-VEGETATION/RECLAMATION OF THE MINING-RELATED OPERATION AND DISTURBANCES MUST BE COMPLETED IN ACCORDANCE WITH PREVIOUS APPROVALS AND APPLICABLE REQUIREMENTS. PRIOR TO THE ISSUANCE OF ANY PERMITS FOR RESIDENTIAL-RELATED CONSTRUCTION ON A PARTICULAR PARCEL, A SITE-SPECIFIC RESIDENTIAL CONSTRUCTION RE-VEGETATION/EROSION CONTROL PLAN MUST BE SUBMITTED TO THE LAND USE DEPARTMENT FOR REVIEW AND APPROVAL. THE PLAN MUST ILLUSTRATE AREAS OF CONSTRUCTION DISTURBANCE, AREAS PROPOSED FOR RE-VEGETATION, AND THE LOCATIONS OF EROSION AND SEDIMENT CONTROL DEVICES. THE APPROVED RE-VEGETATION/EROSION CONTROL PLAN MUST BE IMPLEMENTED AFTER APPROVAL OF CONSTRUCTION AND PRIOR TO OCCUPANCY OF ANY RESIDENCE OR BUILDING. THE PLAN SHALL DEPICT THE LOCATION, TYPE, AND QUANTITY OF SEED OR OTHER PLANTINGS AND EROSION CONTROL DEVICES SUFFICIENT TO STABILIZE DISTURBED AREAS AND AREAS OF CUT AND FILL.

IV. THE EXISTING SOUTHERN ACCESS ROAD TO HIGHWAY 66 (UTE HIGHWAY) MAY BE USED TO SERVE THE APPROVED ELEVEN LOT DEVELOPMENT, PROVIDED THAT THE APPLICANT FIRST SECURES APPROVAL FROM THE COLORADO DEPARTMENT OF TRANSPORTATION FOR USE OF THIS ROAD FOR PRIVATE RESIDENTIAL USE. THE ROAD CONNECTION TO CR 47 SHALL BE MAINTAINED FOR USE BY THE ELEVEN LOT DEVELOPMENT AND MAY ALSO BE USED AS INGRESS/EGRESS FOR EMERGENCY USE UPON APPROVAL OF THE HYGIENE FIRE PROTECTION DISTRICT. IT SHALL BE THE RESPONSIBILITY OF THE HOMEOWNERS' ASSOCIATION TO MAINTAIN THESE ACCESS ROADS AND ALL OF THEIR BRIDGE CROSSINGS: SUCH MAINTENANCE SHALL NOT BE THE RESPONSIBILITY OF THE COUNTY.

V. PRIVATE ACCESS DRIVEWAYS AND ROADWAYS SHALL BE REVIEWED AND APPROVED BY THE COUNTY TRANSPORTATION DEPARTMENT, IN ACCORDANCE WITH COUNTY'S REQUIREMENTS FOR PRIVATE ACCESS IN EFFECT AT THE TIME OF AUTHORIZED DEVELOPMENT AND PRIOR TO ISSUANCE OF ANY PERMITS.

VI. THE APPLICANT OR DEVELOPER SHALL NOTIFY THE COUNTY IMMEDIATELY IF ANY SIGNIFICANT ENVIRONMENTAL, HISTORIC, OR CULTURAL RESOURCES ARE ENCOUNTERED DURING ANY CONSTRUCTION ACTIVITY.

VII. THE DEVELOPMENT SHALL BE SUBJECT TO THE TERMS, CONDITIONS, AND COMMITMENTS OF RECORD AND IN THE FILE FOR THE DOCKET AS APPROVED BY THE BOARD, AND TO THE TERMS OF ANY PREVIOUS DOCKET APPROVALS RELATED TO THE CURRENTLY EXISTING USE.

VIII. THE APPLICANT OR PROPERTY OWNER SHALL *OBTAIN* ALL APPLICABLE FEDERAL, STATE, AND LEGALLY REQUIRED LOCAL PERMITS AS REQUIRED AT TIME OF AUTHORIZED RESIDENTIAL DEVELOPMENT.

IX. THIS PERMANENT VESTING APPROVAL EXTENDS TO AND ASSURES THE RIGHT TO DEVELOP THE SUBJECT ELEVEN LOTS, IN THEIR APPROVED NUMBER AND SIZE, FOR SINGLE-FAMILY RESIDENTIAL USE. THE LOTS SHALL BE SUBJECT TO ALL OTHER COUNTY ZONING AND BUILDING PERMIT REQUIREMENTS IN EFFECT AT THE TIME OF DEVELOPMENT WHICH ARE PREREQUISITE TO THE ISSUANCE OF A BUILDING PERMIT FOR RESIDENTIAL DEVELOPMENT OF EACH LOT, INCLUDING, BUT NOT NECESSARILY LIMITED TO, APPLICABLE SITE PLAN REVIEW, ACCESS REVIEW, AND BUILDING PERMIT REVIEW.

NOTES

1. THIS EXEMPTION SURVEY IS GIVEN TO IMPLEMENT THE TERMS AND CONDITIONS OF DOCKET SE-03-01: CEMEX, AS APPROVED BY THE BOARD OF COUNTY COMMISSIONERS ON MAY 22, 2003 PURSUANT TO RESOLUTION 2003-63.
2. BEARINGS ARE BASED ON THE SOUTH LINE OF THE SE1/4 OF SECTION 9, T3N, R70W OF THE 6TH P.M. AS BEARING S87°27'25"E (ASSUMED MERIDIAN).
3. RECORDED EASEMENTS, RIGHTS-OF-WAY AND LEGAL DESCRIPTION ARE SHOWN, AS APPLICABLE TO THE SUBJECT PROPERTY, PER SPECIAL WARRANTY DEED, RECEPTION NO. 2308601, DATED JULY 17, 2002; ACCESS EASEMENT, RECEPTION NO. 01524420, DATED JUNE 19, 1995; AND REVOCABLE LICENSE, RECEPTION NO. 01524421, DATED JUNE 19, 1995.
4. SET #5 REBARS W/ ALUMINUM CAPS MARKED "D. B. & CO. PLS 23529" AT ALL EXTERIOR BOUNDARY CORNERS UNLESS OTHERWISE NOTED.

STATE OF COLORADO)
) SS
COUNTY OF BOULDER)

THIS PLAT WAS FILED IN THE OFFICE OF THE CLERK AND RECORDER AT 11:19 O'CLOCK A.M., THIS 16th DAY OF April, 2004, AND IS DULY RECORDED IN PLAN FILE P-60 F-3 #16, 17 RECEPTION NO. 2577189.

Fee: $21.00

Linda N. Salas
RECORDER

BY: Brenda
DEPUTY

PREPARED BY:
DREXEL, BARRELL & CO.
4840 PEARL EAST CIRCLE #114
BOULDER, CO 80301-2475
303-442-4338

IN ACCORDANCE WITH C.R.S. 13-80-105:
NOTICE: ACCORDING TO COLORADO LAW YOU MUST COMMENCE ANY LEGAL ACTION BASED UPON ANY DEFECT IN THIS SURVEY WITHIN THREE YEARS AFTER YOU FIRST DISCOVER SUCH DEFECT. IN NO EVENT MAY ANY ACTION BASED UPON ANY DEFECT IN THIS SURVEY BE COMMENCED MORE THAN TEN YEARS FROM THE DATE OF THE CERTIFICATION SHOWN HEREON.

SURVEYOR'S CERTIFICATION

I, WILLIAM K. WRIGHT, A DULY REGISTERED PROFESSIONAL LAND SURVEYOR IN THE STATE OF COLORADO, DO HEREBY STATE THAT THIS LAND SURVEY PLAT OF DOWE FLATS ESTATES SUBDIVISION EXEMPTION PLAT REFLECTS THE RESULTS OF A SURVEY MADE UNDER MY DIRECT RESPONSIBILITY, SUPERVISION AND CHECKING IN ACCORDANCE WITH THE REQUIREMENTS OF SECTION 38-51-106, C.R.S., AS AMENDED, AND IS TRUE AND CORRECT TO THE BEST OF MY KNOWLEDGE, INFORMATION AND BELIEF.

23529
William K Wright

WILLIAM K. WRIGHT
COLORADO REGISTERED PROFESSIONAL
LAND SURVEYOR NO. 23529

P-60 F-3 #16 (1 of 2)

B59-100

S:\S5143-8\51438pl01.dwg, 03/26/2004 02:43:37 PM, Drexel, Barrell & Co,sds

2577189
Page: 1 of 2
04/16/2004 11:19A
Boulder County Clerk, CO PLAT
R 21.00 D 0.00

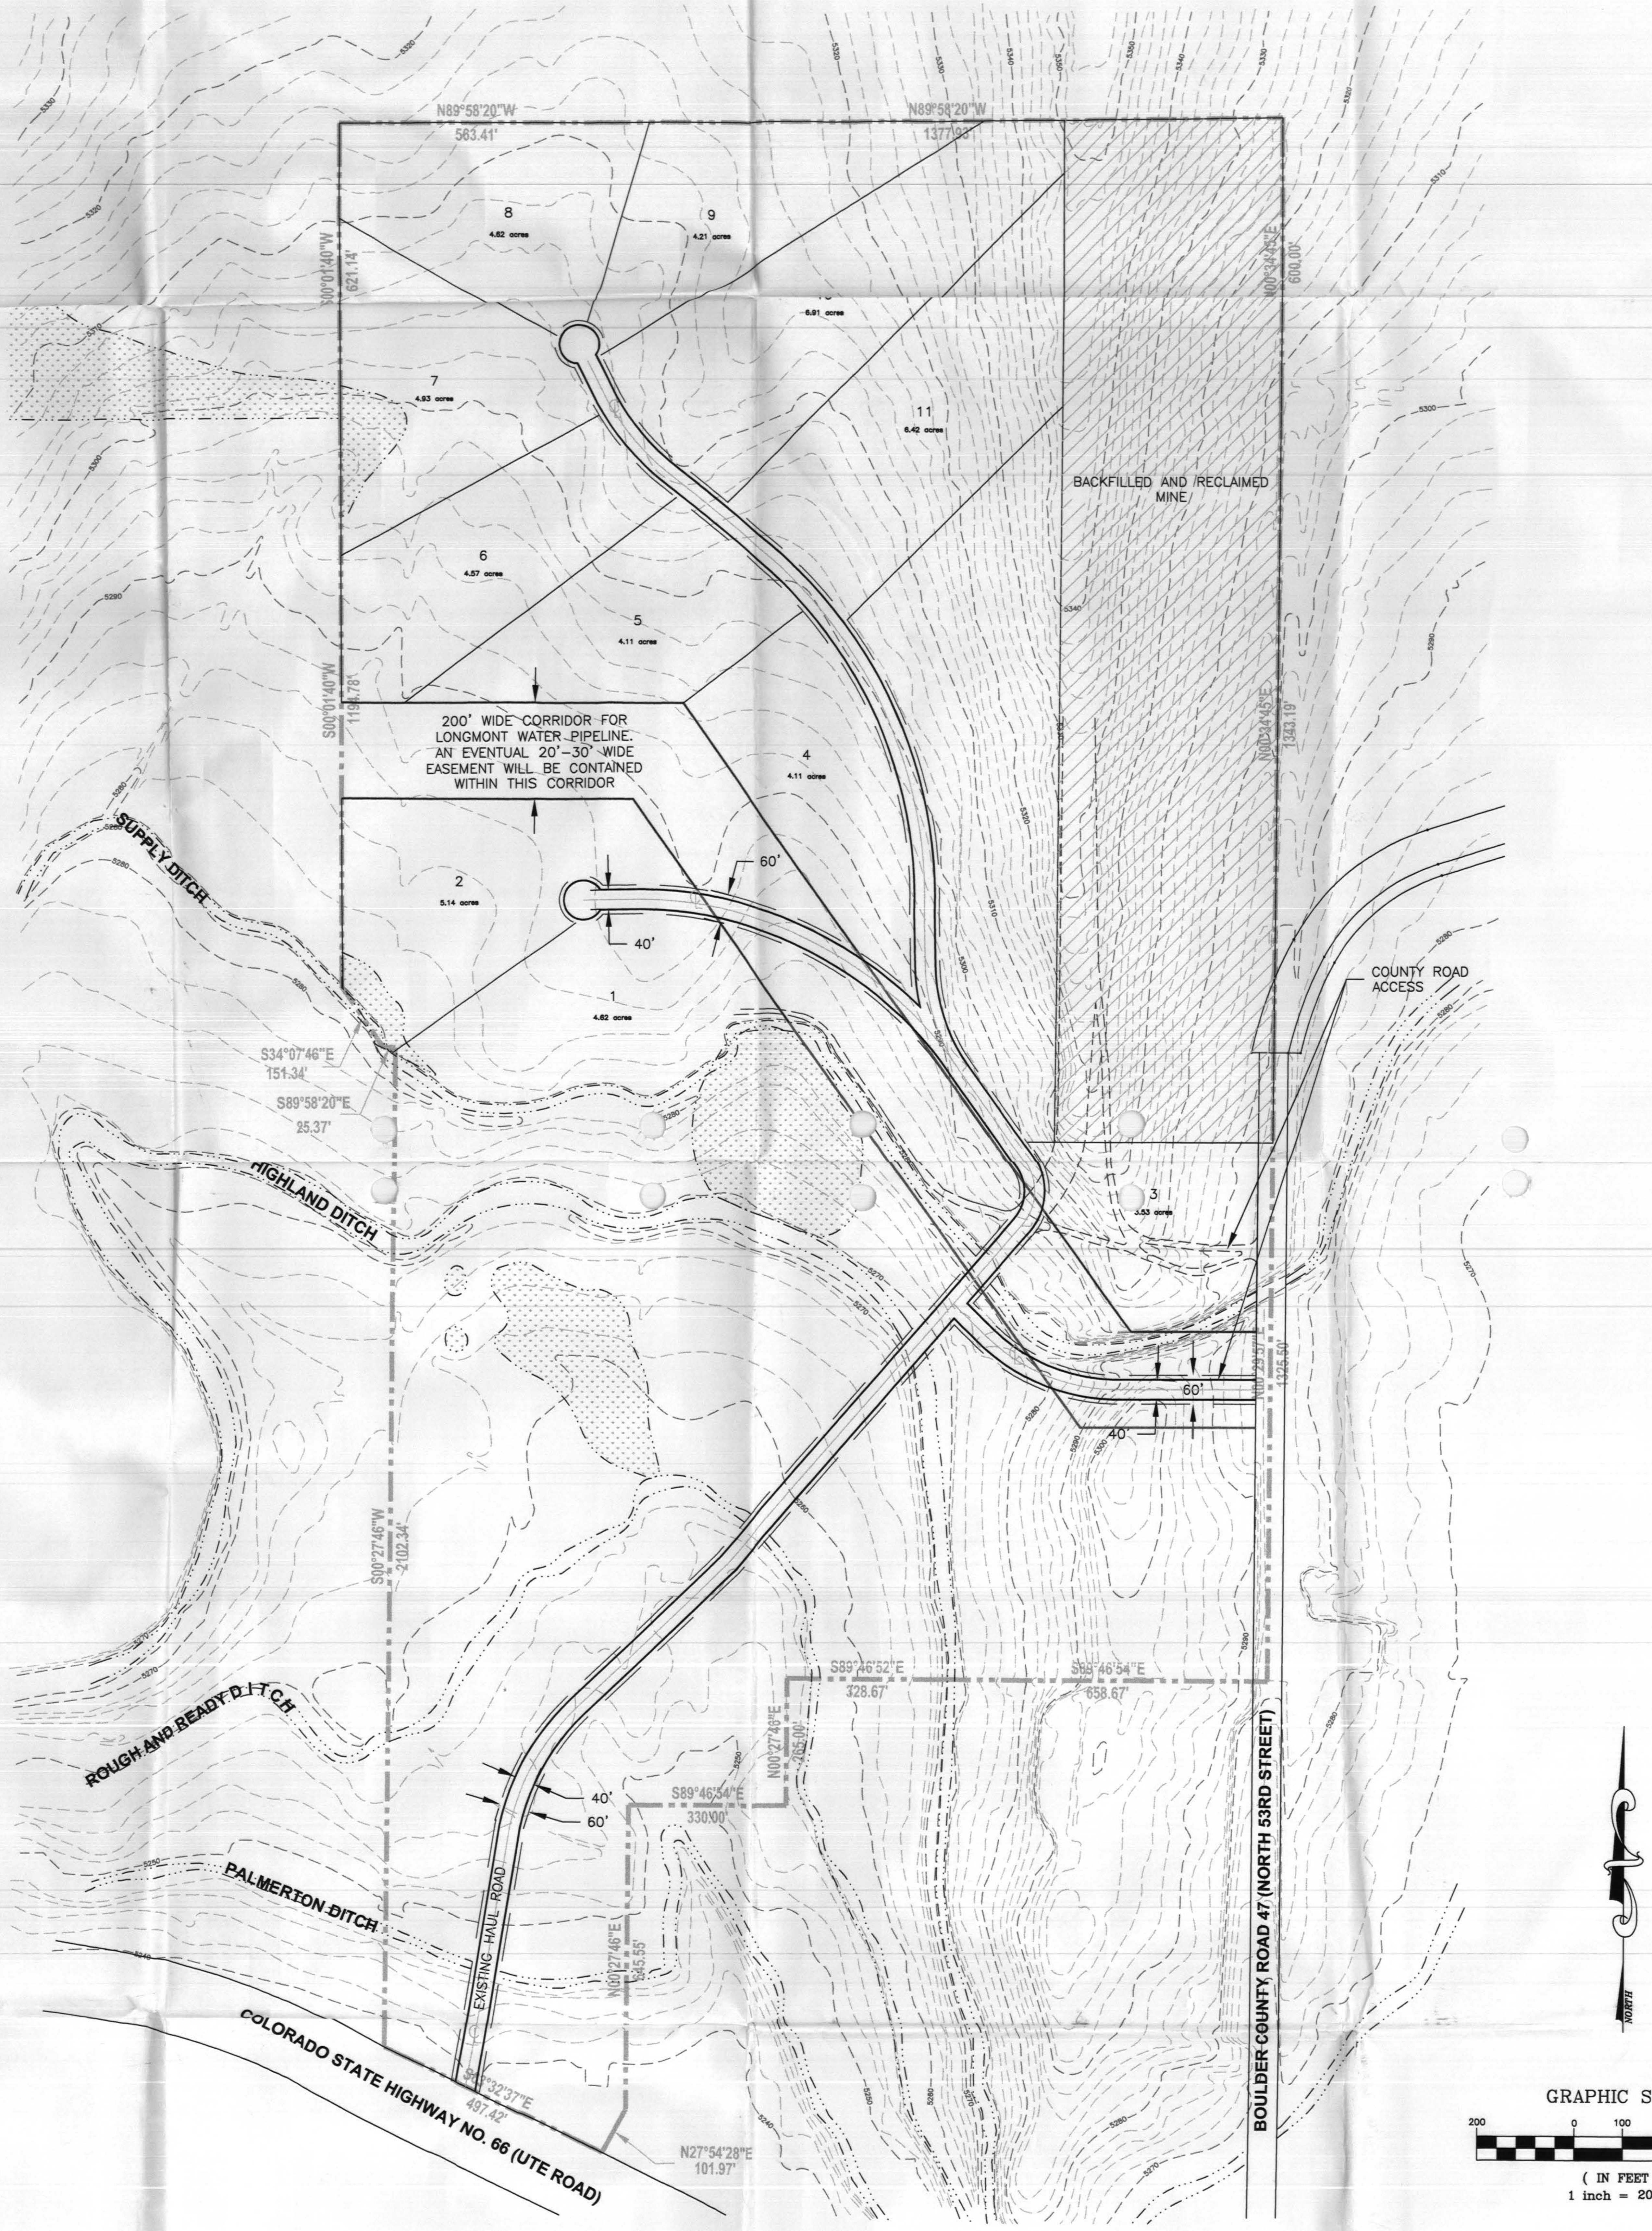

GRAPHIC SCALE

200 0 100 200 400

(IN FEET)
1 inch = 200 ft.

LEGEND

▬ ▪ ▪ ▬	PROPERTY LINE
—— ——	PROPOSED ROW/EASEMENT
═══	PAVED ROAD
═ ═ ═	UN-PAVED ROAD
—···—···—	DITCH
— — —	INDEX CONTOUR
- - -	INTERMEDIATE CONTOUR
░	WETLANDS

APPROVED
Lots 1-11 & Access (subject to conditions)
ONLY AS shown on this map.
This approval is not to be construed as to allow any violation of the Boulder County Building Code or the Boulder County Land Use Code.

Any field modifications must be approved by the Land Use Department prior to implementation.

Boulder County Land Use Department
BOCC
By Todd Tucker Date 5/22/03

RECEIVED
MAY 22 2003
BOULDER COUNTY
LAND USE DEPT.

SITE PLAN-COMPROMISE CONFIGURATION

BANKS AND GESSO, LLC.
720 KIPLING ST., SUITE 117
LAKEWOOD, COLORADO 80215
(303) 274-4277

CEMEX, INC
1200 SMITH ST. SUITE 2400
HOUSTON, TX 77002

DOWE FLATS DEVELOPMENT PARCEL
SUBDIVISION EXEMPTION SURVEY PLAT
BOULDER COUNTY
COLORADO

JOB NO	DATE	SCALE	DRAWN BY	DESIGNED BY	APPROVAL	REV	SHEET
02031	4/2/03	1"=200'	DRF				

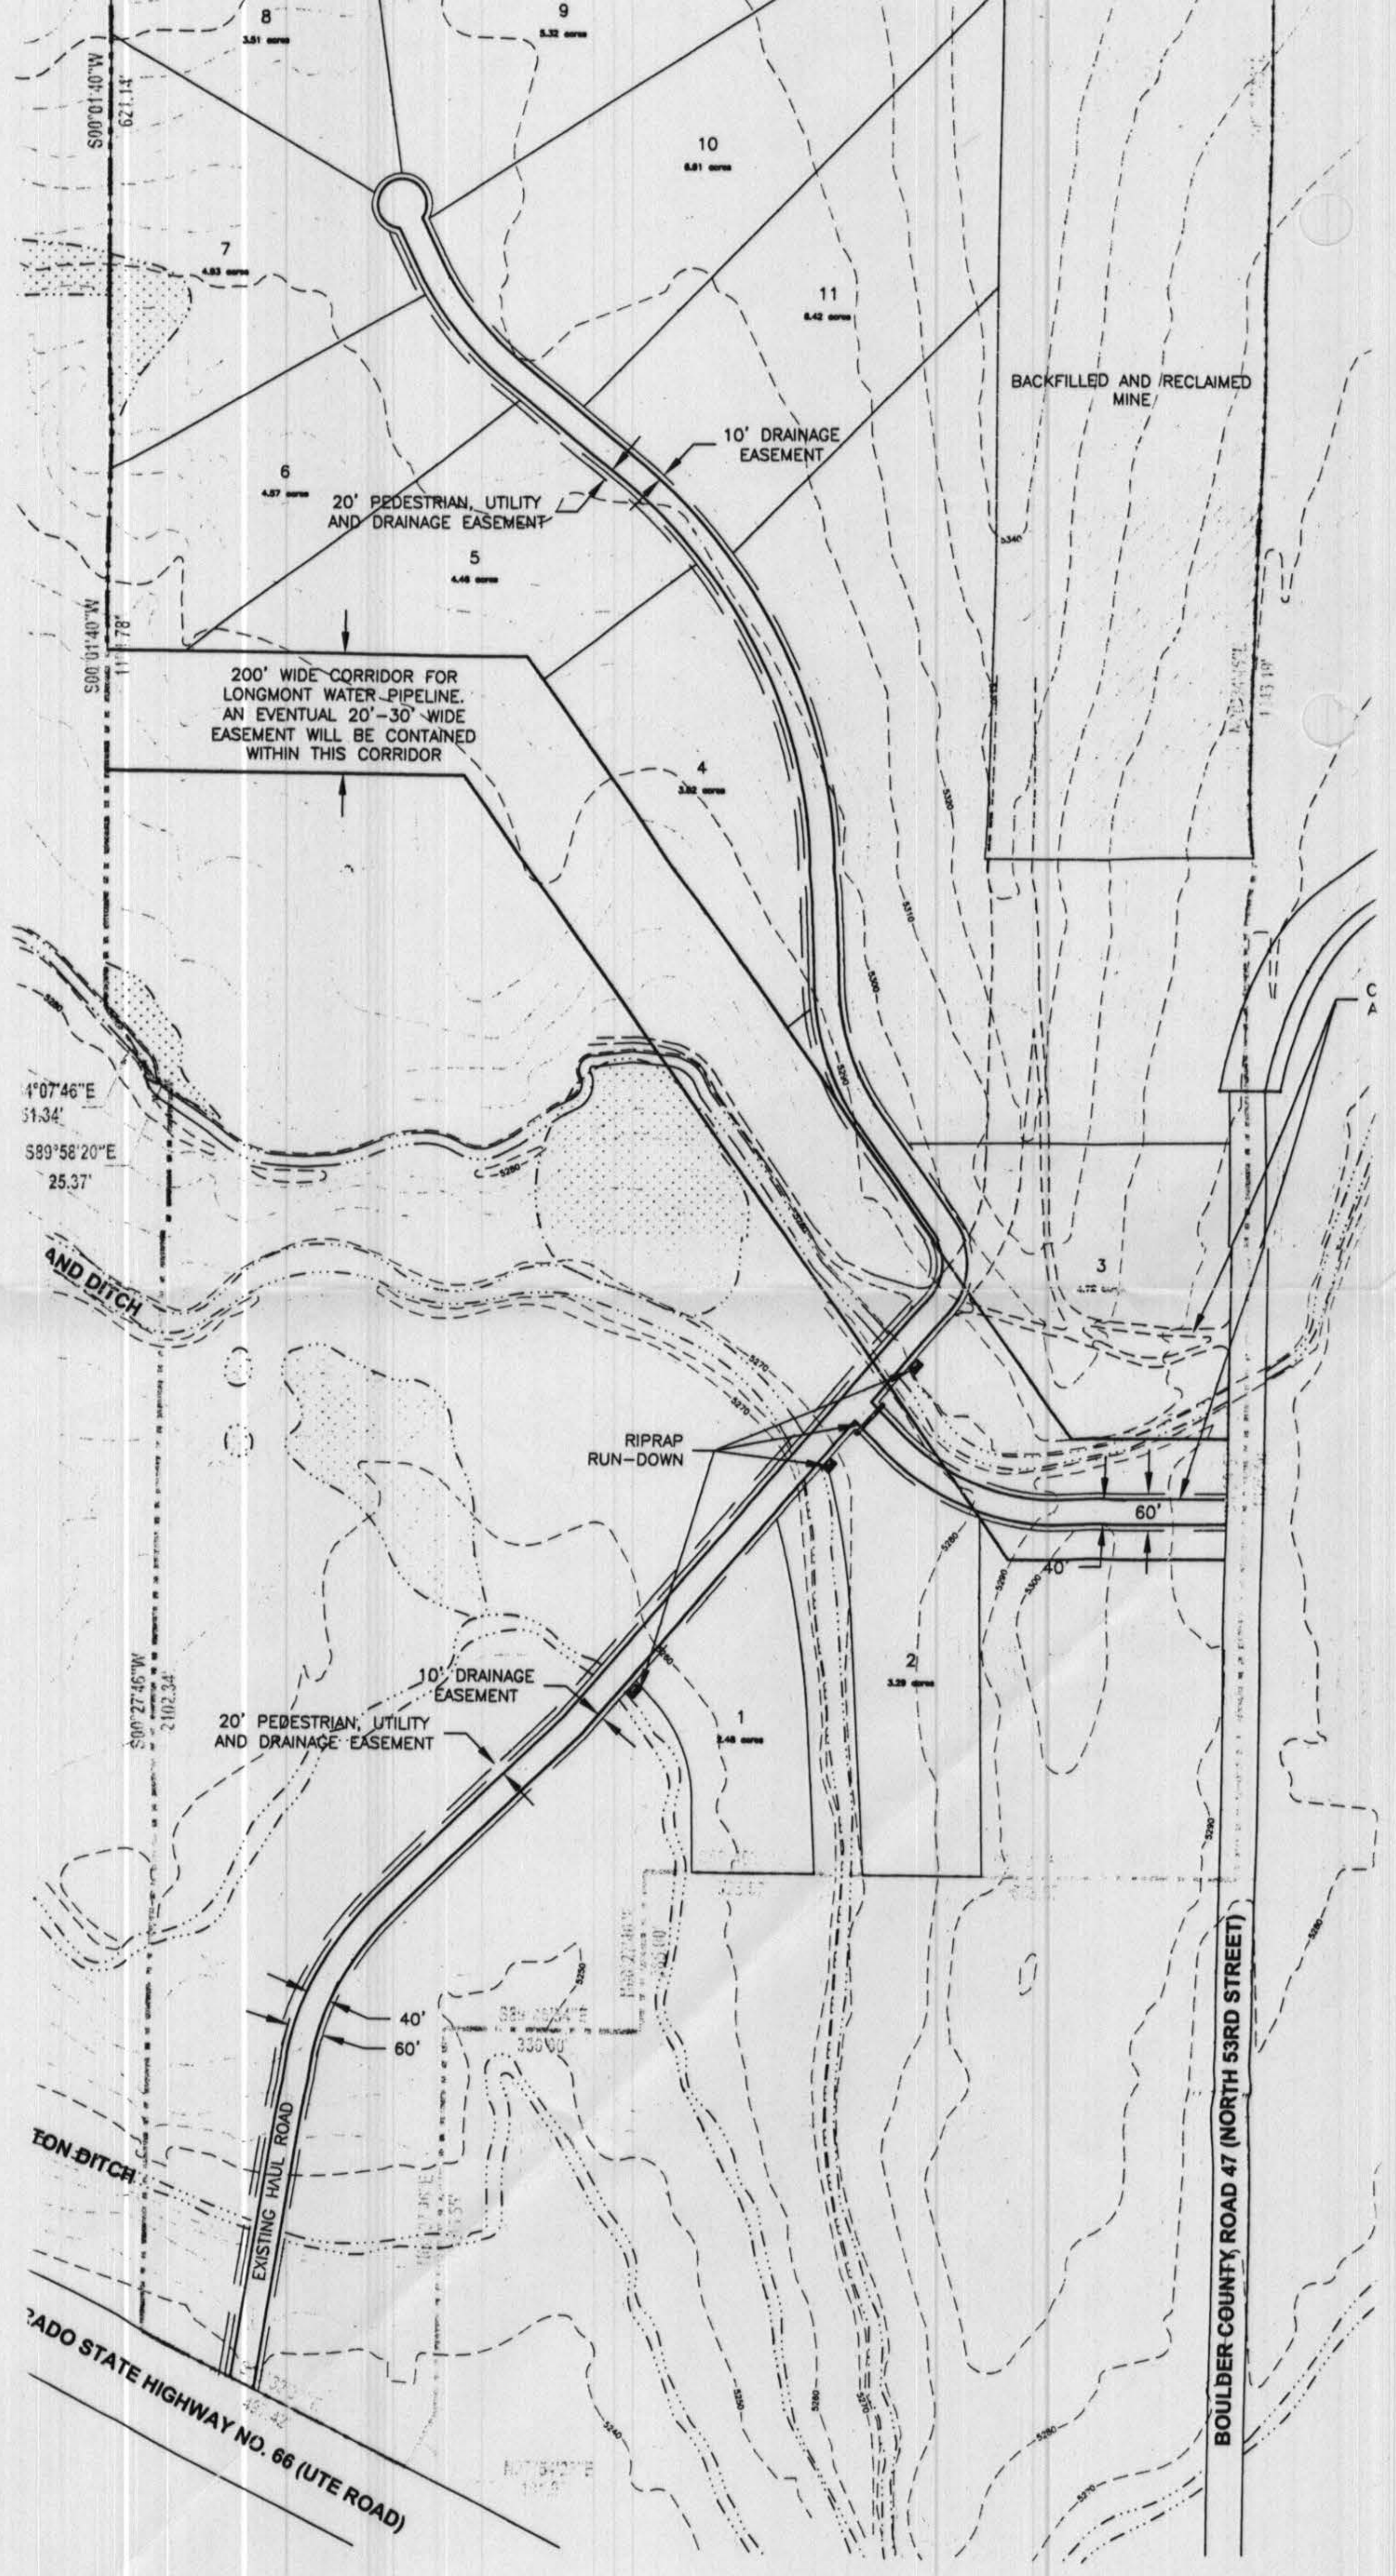
8
9
10
7
11
6
5
4
3
2
1
S00°01'40"W
BACKFILLED AND RECLAIMED MINE
10' DRAINAGE EASEMENT
20' PEDESTRIAN, UTILITY AND DRAINAGE EASEMENT
200' WIDE CORRIDOR FOR LONGMONT WATER PIPELINE. AN EVENTUAL 20'-30' WIDE EASEMENT WILL BE CONTAINED WITHIN THIS CORRIDOR
S89°58'20"E
25.37'
RIPRAP RUN-DOWN
60'
40'
10' DRAINAGE EASEMENT
20' PEDESTRIAN, UTILITY AND DRAINAGE EASEMENT
S00°27'46"W
2102.34'
40'
60'
EXISTING HAUL ROAD
TON DITCH
AND DITCH
RADO STATE HIGHWAY NO. 66 (UTE ROAD)
BOULDER COUNTY ROAD 47 (NORTH 53RD STREET)

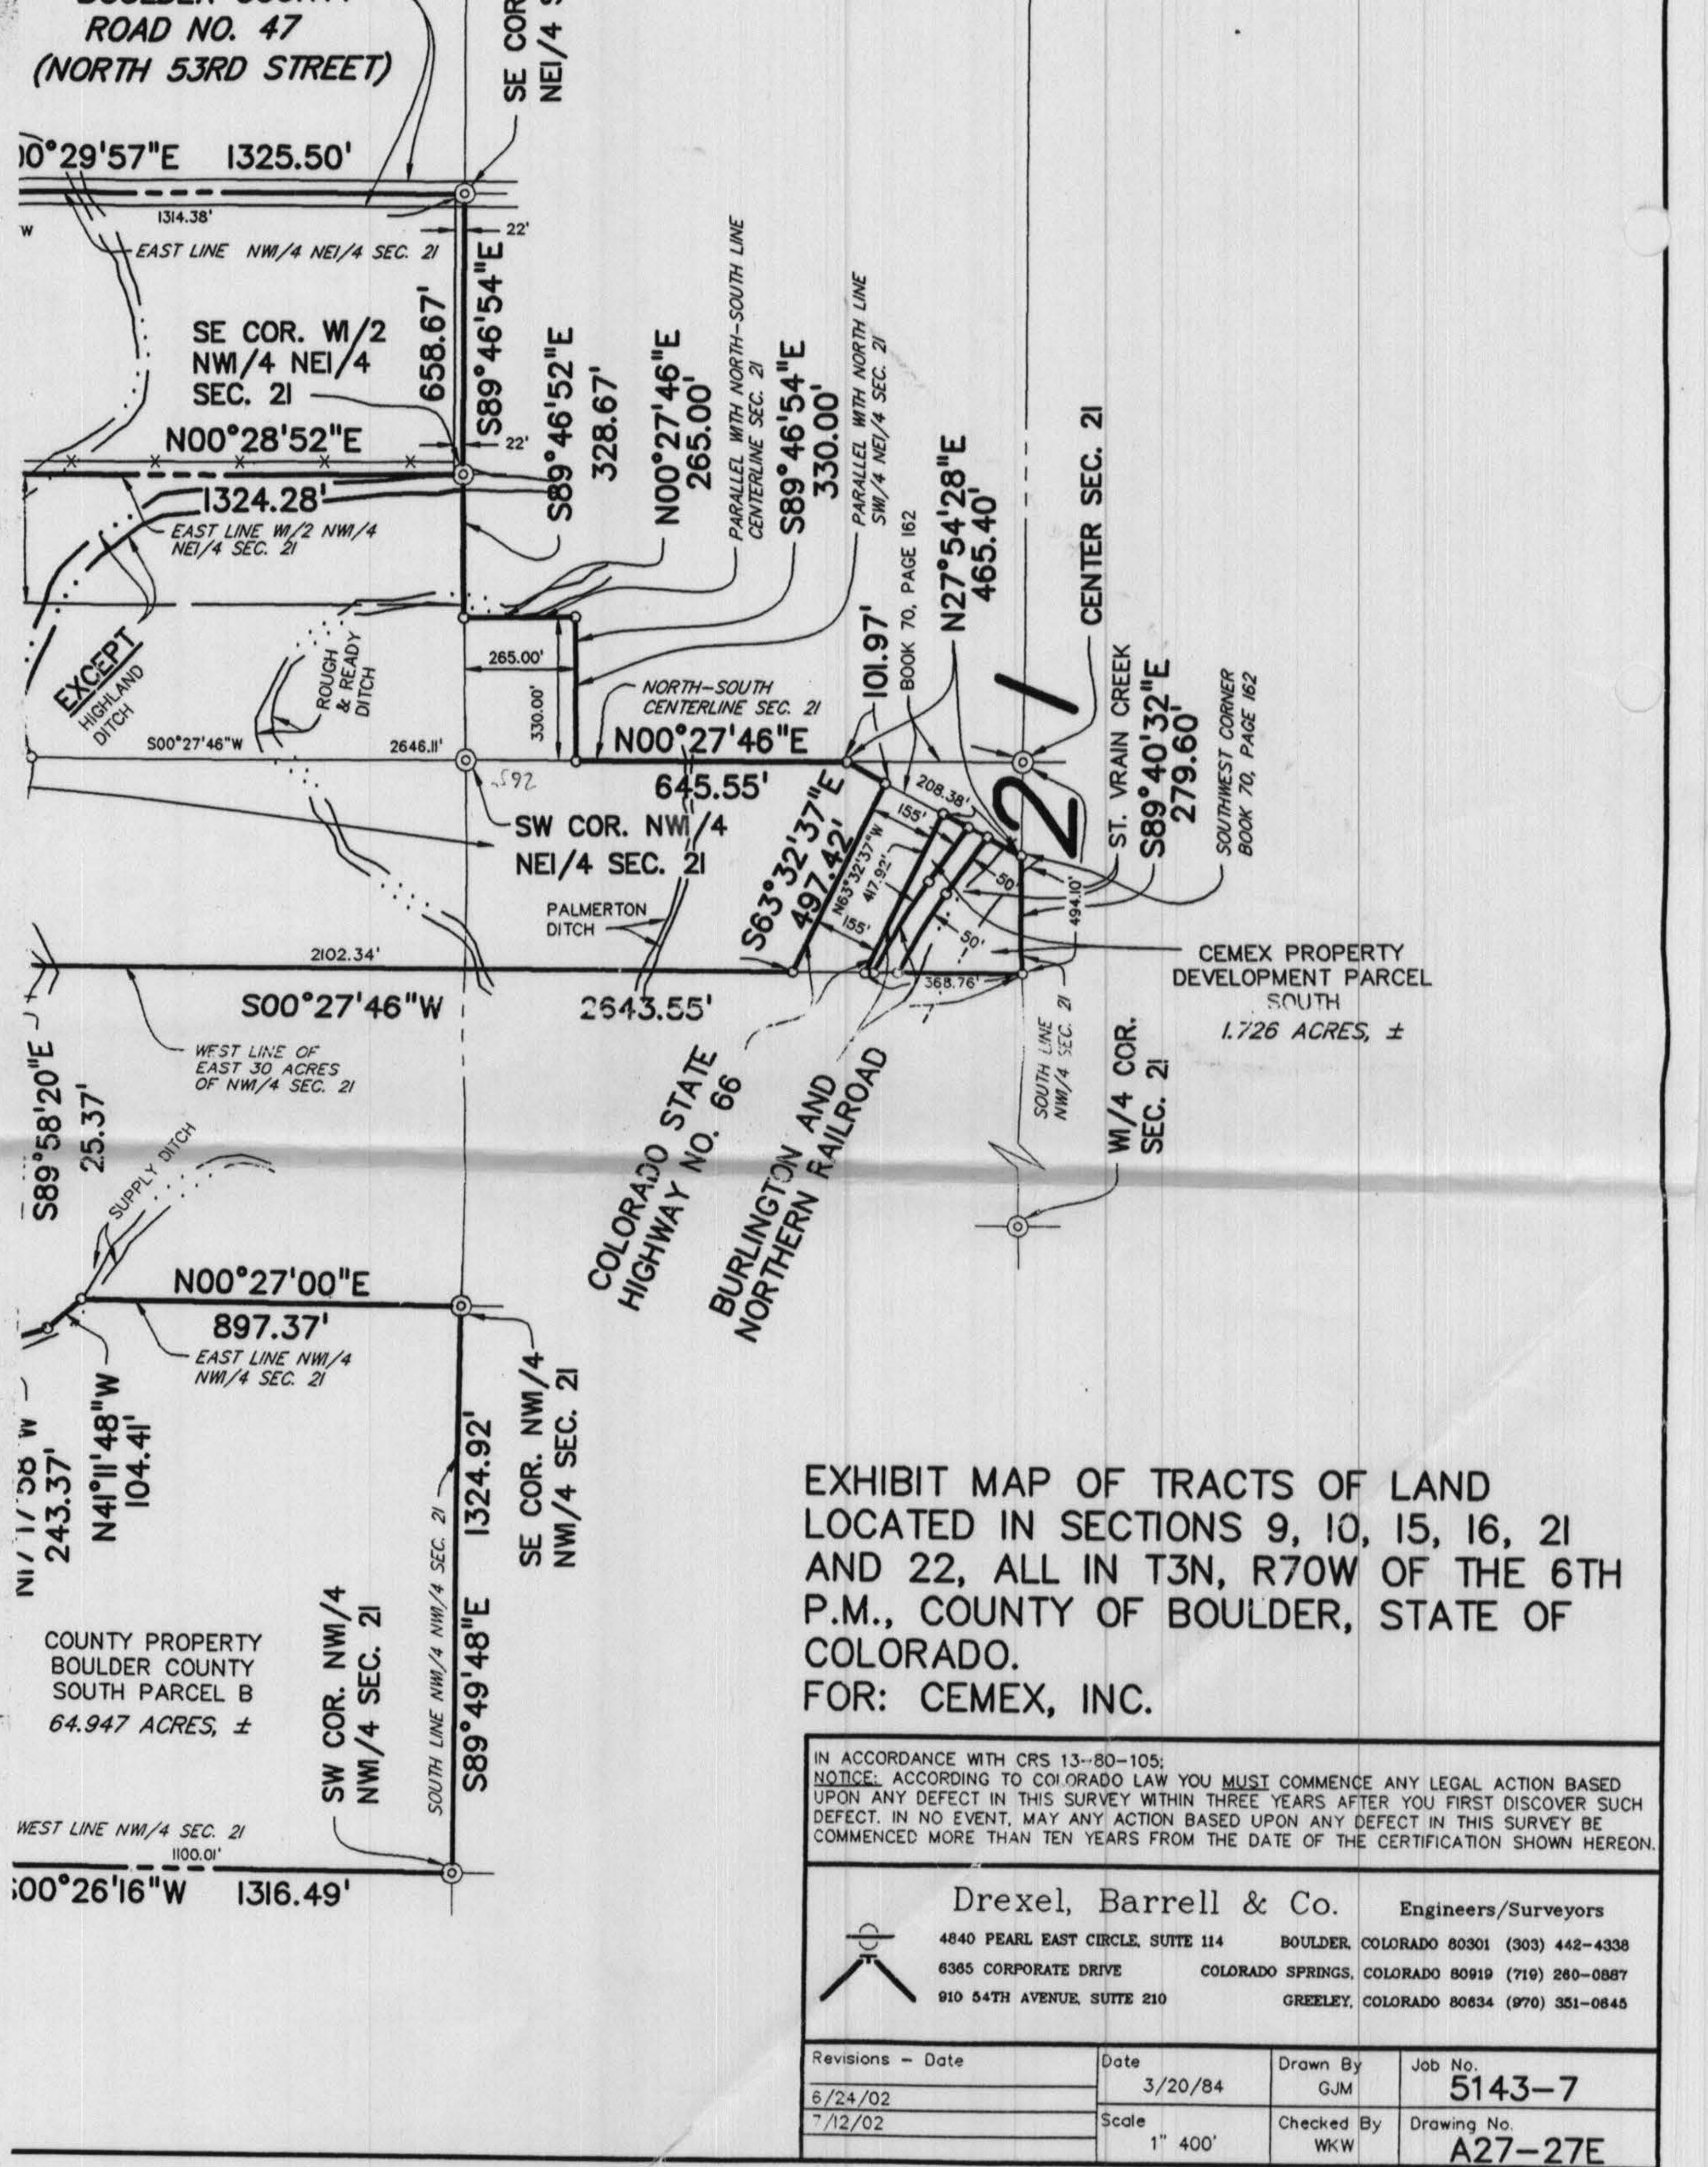

EXHIBIT MAP OF TRACTS OF LAND LOCATED IN SECTIONS 9, 10, 15, 16, 21 AND 22, ALL IN T3N, R70W OF THE 6TH P.M., COUNTY OF BOULDER, STATE OF COLORADO.
FOR: CEMEX, INC.

IN ACCORDANCE WITH CRS 13-80-105;
NOTICE: ACCORDING TO COLORADO LAW YOU MUST COMMENCE ANY LEGAL ACTION BASED UPON ANY DEFECT IN THIS SURVEY WITHIN THREE YEARS AFTER YOU FIRST DISCOVER SUCH DEFECT. IN NO EVENT, MAY ANY ACTION BASED UPON ANY DEFECT IN THIS SURVEY BE COMMENCED MORE THAN TEN YEARS FROM THE DATE OF THE CERTIFICATION SHOWN HEREON.

Drexel, Barrell & Co. Engineers/Surveyors
4840 PEARL EAST CIRCLE, SUITE 114 BOULDER, COLORADO 80301 (303) 442-4338
6365 CORPORATE DRIVE COLORADO SPRINGS, COLORADO 80919 (719) 260-0887
910 54TH AVENUE, SUITE 210 GREELEY, COLORADO 80634 (970) 351-0645

Revisions – Date	Date	Drawn By	Job No.
6/24/02	3/20/84	GJM	5143-7
7/12/02	Scale 1" 400'	Checked By WKW	Drawing No. A27-27E