

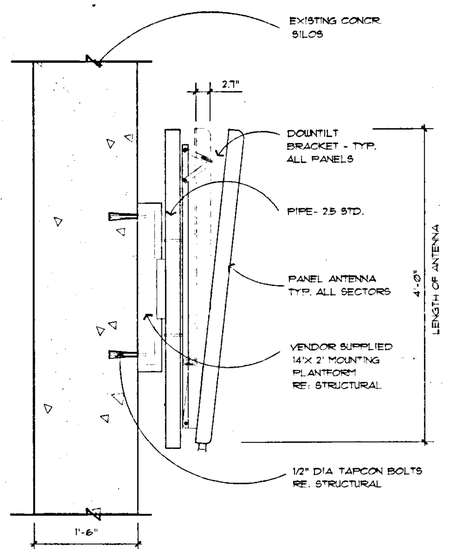


11/A2 **ANTENNA MOUNT - TYP.**
SCALE 1" = 1'- 0"

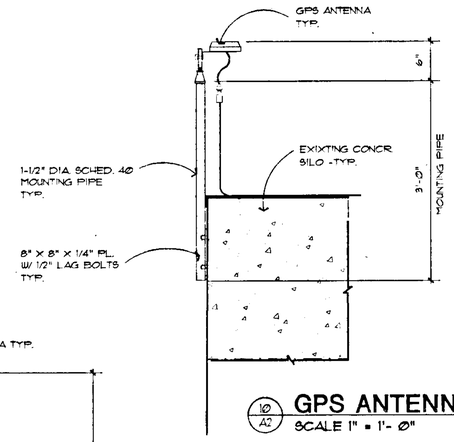


16/A2 **GPS ANTENNA - TYP**
SCALE 1" = 1'- 0"

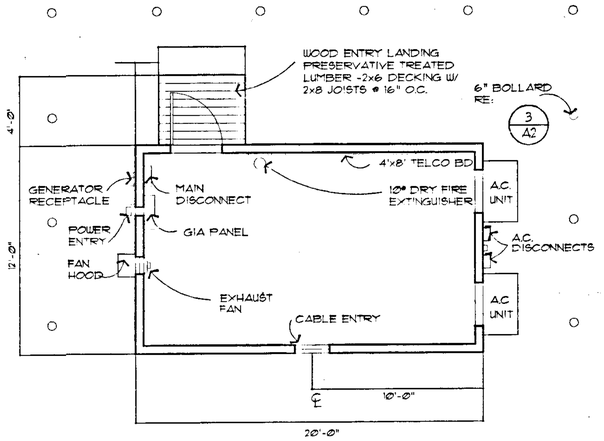


NORTH TRUE


10/A2 **FLOOR PLAN**
1/4" = 1'-0"

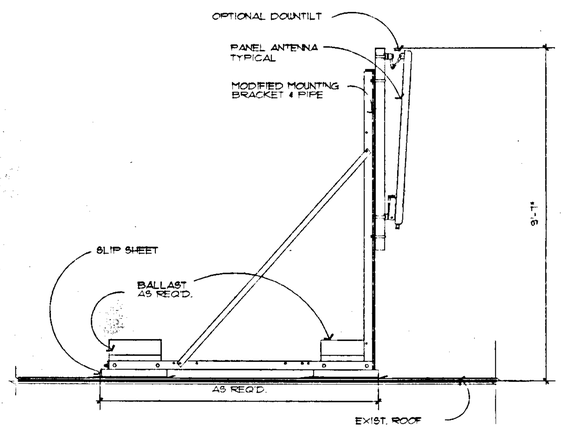


8/A2 **NON-PENETRATING ROOF TOP ANTENNA MOUNT - TYP.**
SCALE 1/2" = 1'- 0"

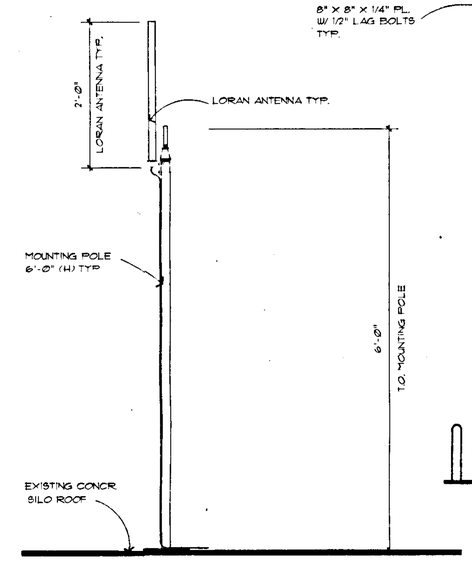


7/A2 **LORAN ANTENNA - TYP.**
SCALE 1" = 1'-0"

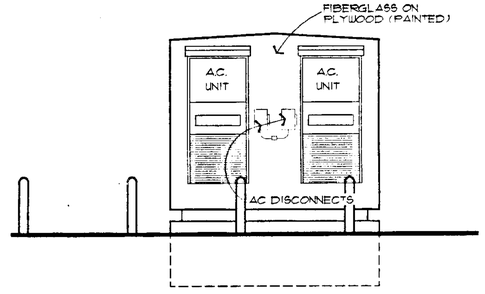


6/A2 **EAST ELEVATION**
1/4" = 1'-0"

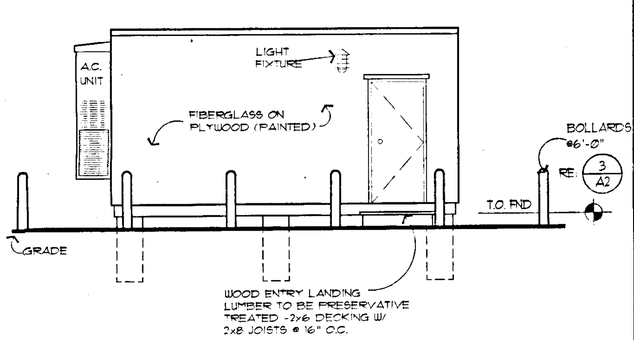


5/A2 **NORTH ELEVATION**
1/4" = 1'-0"

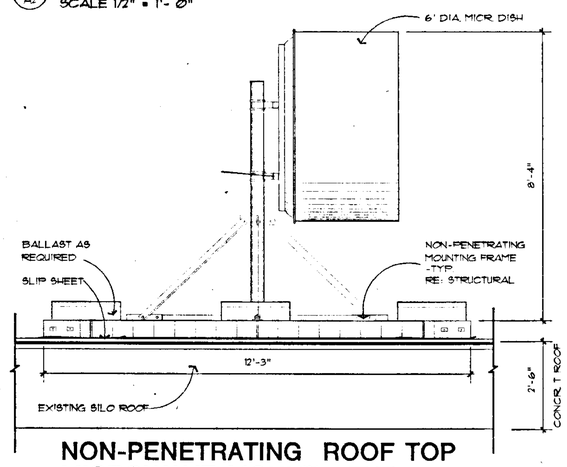


4/A2 **NON-PENETRATING ROOF TOP MICROWAVE MOUNT - TYP.**
SCALE 1/2" = 1'- 0"

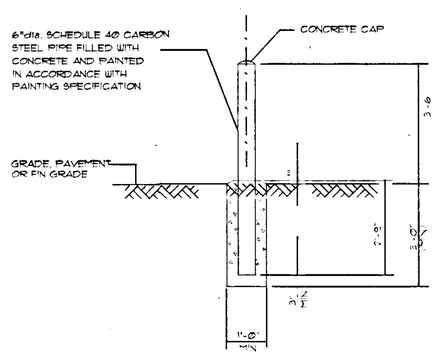

3/A2 **GUARD POST (BOLLARD)**
NTS.

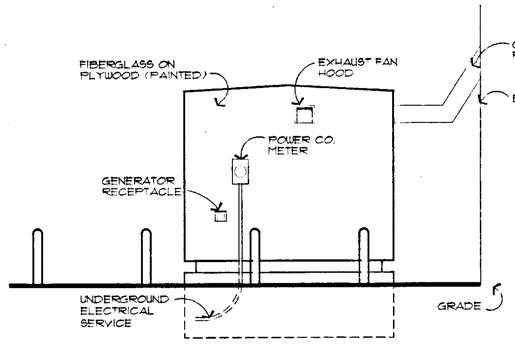

2/A2 **WEST ELEVATION**
1/4" = 1'-0"

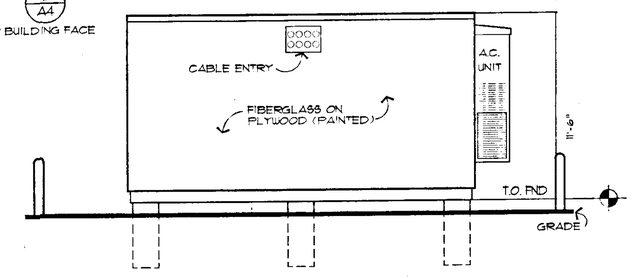

1/A2 **SOUTH ELEVATION**
1/4" = 1'-0"

Stamp

STATE OF COLORADO
REX ALAN CROOK
20154
LICENSED ARCHITECT

T•REX Architex
architecture
planning
interiors
295 Fillmore • Suite 260
Denver Colorado 80206-5023
303 399-2975 • fax 303 399-2936

Drawings

Drawings and Specifications as instruments of service are and shall remain the property of the Architect whether the Project for which they are made is executed or not. The Owner shall be permitted to retain copies, including reproducible copies, of Drawings and Specifications for information and reference in connection with the Owner's use and occupancy of the Project. The Drawings and Specifications shall not be used by the Owner on other projects, for additions to this Project or for the completion of this Project by others, provided the Architect is not in default under this Agreement, except by agreement in writing and with appropriate compensation to the Architect.

AIRTOUCH Cellular
3305 160th Avenue SE
Second Floor
Bellevue, WA 98008

DATE	ISSUED AS
08-28-97	preliminary
—	zoning-sukeall use permit application
—	construction permit application
—	issued for zoning / construction
—	issued for construction
—	issued zoning & construction permit
—	as built / record set
11-12-97	owner approval

Project Title

DEN-LYONS
ALT. 8
CELL SITE

Southdown Cement Plant
5134 Ute Highway
Thornton, Colorado 80503

Issue Date
11-12-97

Date Revisions

Sheet 2 of 4

A2


GENERAL NOTES

1. IT IS THE CONTRACTORS RESPONSIBILITY TO VISIT THE SITE AND NOTIFY THE ARCHITECT OF ANY DISCREPANCIES BETWEEN THE DOCUMENTS AND ACTUAL CONDITIONS.
2. MECHANICAL IS DESIGN/BUILD BY US WEST/ NEWVECTOR.
3. FOR INFORMATION REGARDING THIS SITE, CONTACT:
   AGENT: JOHN LORE SOUTHDOWN INC AT 823-2100 X 2109
   PM2: WAYNE GARRETT, AIRTOUCH CELLULAR, AT 754-6283
4. ALL INTERRUPTED SYSTEMS TO BE RESTORED TO ORIGINAL CONDITION AND OPERATION.
5. ALL DEMOLISHED ITEMS ARE TO BE REMOVED COMPLETELY FROM THE SITE. CONTACT JOHN LORE CONCERNING ANY SALVAGEABLE ITEMS.
6. PATCH AND REPAIR ANY DAMAGED ITEMS TO MATCH ORIGINAL CONDITIONS.
9. CONTRACTOR TO PROVIDE 2" DIA. CONDUIT FROM EQUIPMENT ROOM TO TELEPHONE ROOM FOR TELCO. COORDINATE LOCATION WITH JOHN LORE, US WEST COMMUNICATIONS, AND WAYNE GARRETT

DEN LYONS
CELLULAR TELEPHONE EXCHANGE

OWNER:

USWEST
NEWVECTOR GROUP, INC.
3350 161st Avenue SE
Bellevue, Washington 98009

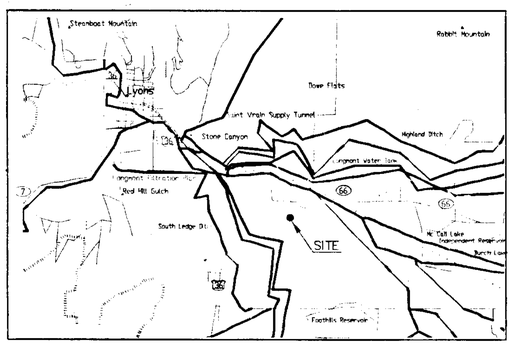

VICINITY MAP
NORTH NO SCALE

PROJECT DATA

ADDRESS
SOUTHDOWN CEMENT PLANT
5134 Ute Highway
Lyons, Colorado

JURISDICTION
BOULDER COUNTY

CODE ANALYSIS

CONSTRUCTION TYPE	V- NR
OCCUPANCY	B
HEIGHT	77'-0" T.O. ANT/MICR. FACE 148'-6" T.O. ANT. FACE
NO. STORIES	VARIES
GROSS BUILDING AREA	2000 SQ. FT. APPROX.
ALLOWABLE AREA	UL
OCCUPANT LOAD	2/ UNMANNED

INDEX OF DRAWINGS

T1	TITLE SHEET - PROJECT SUMMARY
A1	SITE MAP, DETAILS
A2	ORIENTATION PLANS, DETAILS
A3	BUILDING ELEVATIONS, DETAILS
A4	BUILDING ELEVATIONS, DETAILS
S1	STRUCTURAL DETAILS
E1	ELECTRICAL DRAWINGS

PROJECT SUMMARY

VERBAL SUMMARY: WITHOUT FORCE AND EFFECT ON REQUIREMENTS OF CONTRACT DOCUMENTS, THE DESCRIPTION OF THE WORK OF THE CONTRACT CAN BE SUMMARIZED AS FOLLOWS.

SITE IMPROVEMENTS FOR A CELLULAR TELEPHONE SITE FOR US WEST/ NewVector, INC, KNOWN AS "DEN LYONS." THE WORK CONSISTS OF INSTALLING A 12'X20' PREFAB EQUIPMENT BUILDING ON GRADE, THE INSTALLATION OF A 6'-0" MICROWAVE DISH, 2 SECTORS OF ANTENNA ARRAYS ON EXISTING CONCRETE SILO FACES, AND 1 SECTOR ON EXISTING ROOF. ALL EQUIPMENT TO BE PAINTED TO MATCH EXISTING CONDITIONS.

APPROVAL

THIS SPACE IS RESERVED FOR SIGNATURES OF INVOLVED PARTIES TO INDICATE THAT THEY HAVE REVIEWED THE ACCOMPANYING DOCUMENTS AND HAVE APPROVED THEM. CHANGES INITIATED AFTER APPROVALS HAVE BEEN GIVEN MAY RESULT IN ADDITIONAL DESIGN OR CONSTRUCTION COSTS.

John Lore, Southdown Concrete Plant - Owner	date
Frank Pratt - Engineer, US West NewVector Group, Inc.	date
Wayne Garett -PM2, US West NewVector, Inc.	date

Stamp

STATE OF COLORADO
REX ALAN CROOK
20154B
LICENSED ARCHITECT

T•REX Architex
architecture
planning
interiors
2336 Fillmore • Suite 2080
Denver Colorado 80206-5023
(303) 388-2918 • fax (303) 388-5888

Drawings

Drawings and Specifications as instruments of service are and shall remain the property of the Architect (whether the Project for which they are made is executed or not). The Owner shall be permitted to retain copies, including reproduction masters, of Drawings and Specifications for information and reference in connection with the Owner's use and occupancy of the Project. The Drawings and Specifications shall not be used by the Owner on other projects, for additions to this Project or for the completion of this Project by others (provided the Architect is not in default under this Agreement), except by agreement in writing and with appropriate compensation to the Architect.

AIRTOUCH Cellular
3305 160th Avenue SE
Second Floor
Bellevue, WA 98008

DATE	ISSUED AS
06-28-97	preliminary
—	zoning-special use permit application
—	construction permit application
—	issued for zoning / construction
—	issued for construction
—	issued zoning & construction permit
—	as built / record set
11-12-97	owner approval

Project Title

DEN-LYONS
ALT. 8
CELL SITE


Southdown Cement Plant
5134 Ute Highway
Lyons, Colorado 80503

Issue Date
11-12-97

Date Revisions


Sheet 1 of 1

T1

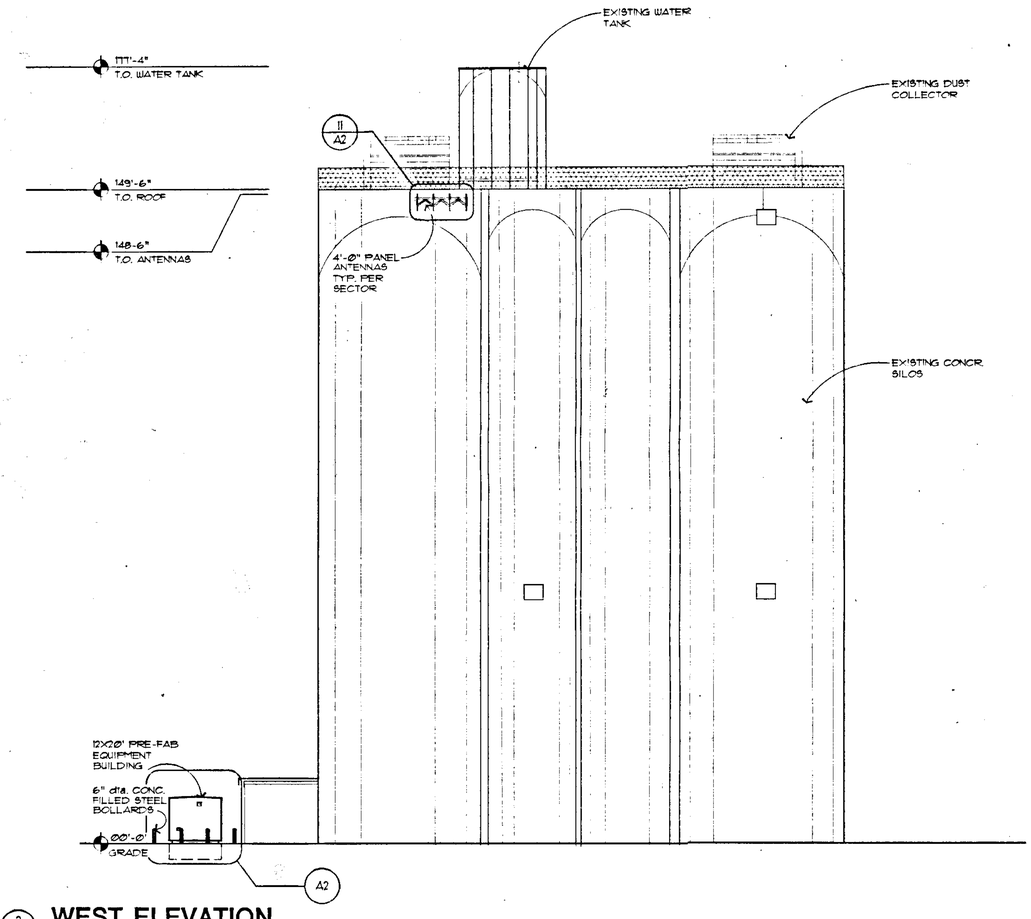

2/A3 WEST ELEVATION

SCALE 1/16" = 1'- 0"

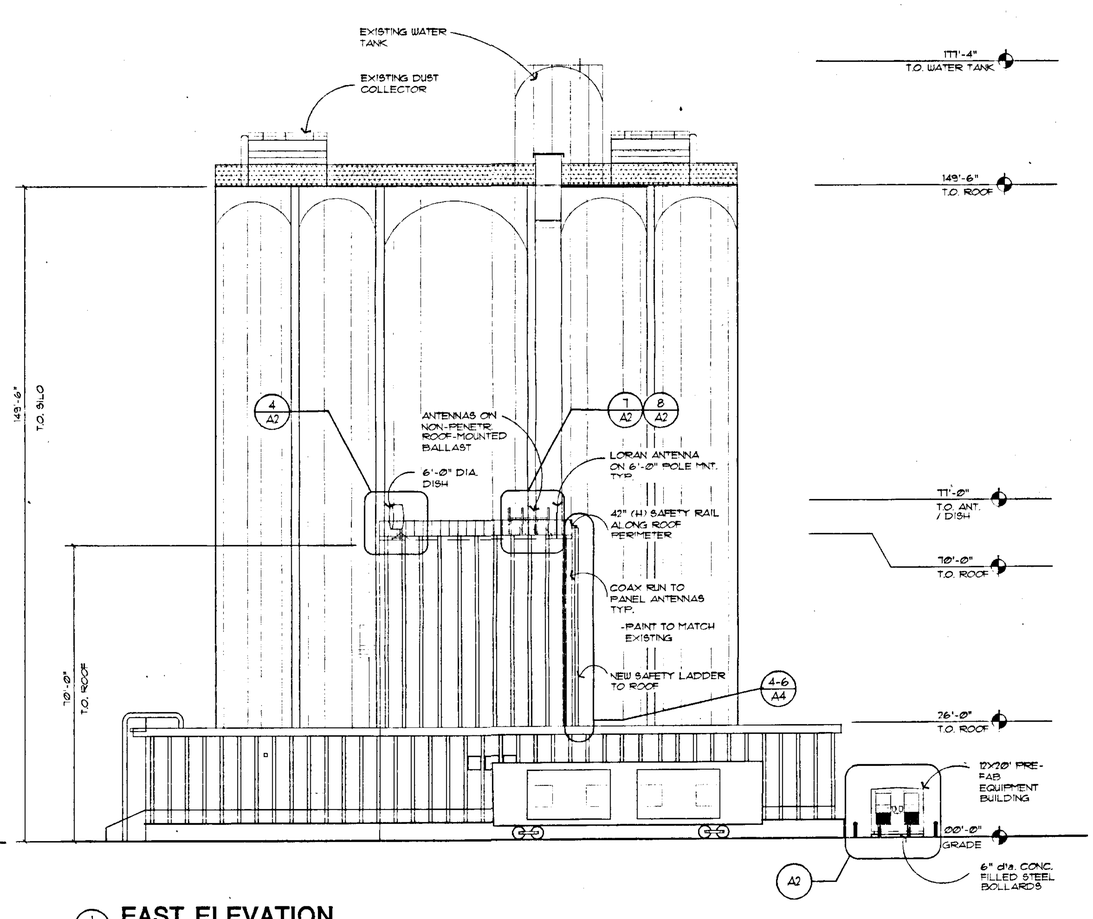

1/A3 EAST ELEVATION

SCALE 1/16" = 1'- 0"

Stamp

STATE OF COLORADO
REX ALLAN CROOR
201548
LICENSED ARCHITECT

T•REX Architex
a architecture
a planning
a interiors
2155 Filmore • Suite 250
Denver Colorado 80206-5023
303 388-2918 • fax 303 388-2838

Drawings

Drawings and Specifications as instruments of service are and shall remain the property of the architect whether the Project for which they are made is executed or not. The Owner shall be permitted to retain copies, including reproducible copies, of Drawings and Specifications for information and reference in connection with the Owner's use and occupancy of the Project. The Drawings and Specifications shall not be used by the Owner on other projects, for additions to this Project or for the completion of this Project by others, provided the Architect is not in default under this Agreement, except by agreement in writing and with appropriate compensation to the Architect.

AIRTOUCH Cellular
3305 160th Avenue SE
Second Floor
Bellevue, WA 98008

DATE	ISSUED AS
08-28-97	— preliminary
—	zoning-special use permit application
—	construction permit application
—	issued for zoning / construction
—	issued for construction
—	issued zoning & construction permit
—	as built / record set
11-12-97	owner approval

Project Title

DEN-LYONS
ALT. 8
CELL SITE


Southdown Cement Plant
5134 Ute Highway
Thornton, Colorado 80503

Issue Date
11-12-97

Date Revisions

Sheet 3 of 4

A3

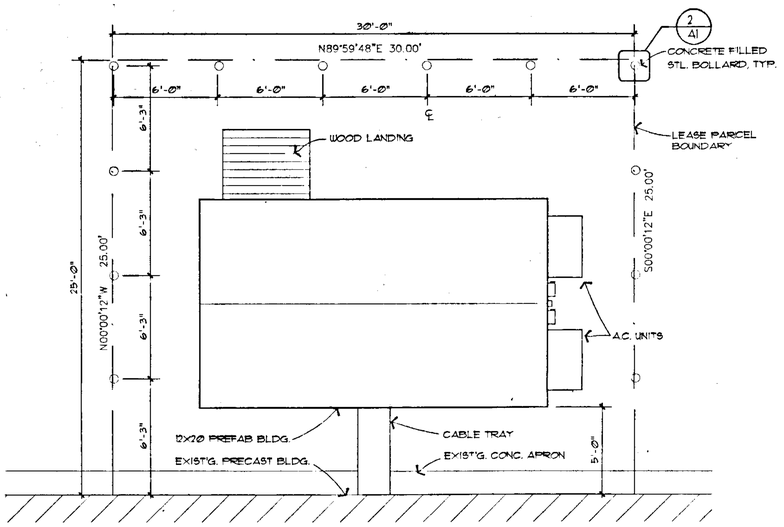

NORTH


2 A1 **ENLARGED SITE PLAN**

SCALE: 1/4"=1'-Ø"

STANDARD CIVIL NOTES:

SITE WORK

1. ALL SITE WORK SHALL BE AS INDICATED ON THE DRAWINGS AND STIPULATED IN THE SPECIFICATION PROJECT SUMMARY.
2. RUBBISH, STUMPS, DEBRIS, STICKS, STONES AND OTHER REFUSE SHALL BE REMOVED FROM THE SITE AND DISPOSED OF LEGALLY.
3. THE SITE SHALL BE GRADED TO CAUSE SURFACE WATER TO FLOW AWAY FROM THE PCS EQUIPMENT AND TOWER AREAS.
4. NO FILL OR EMBANKMENT MATERIAL SHALL BE PLACED ON FROZEN GROUND. FROZEN MATERIALS, SNOW OR ICE SHALL NOT BE PLACED IN ANY FILL OR EMBANKMENT.
5. ALL EXISTING ACTIVE SEWER, WATER, GAS, ELECTRIC AND OTHER UTILITIES WHERE ENCOUNTERED IN THE WORK SHALL BE PROTECTED AT ALL TIMES, AND WHERE REQUIRED FOR THE PROPER EXECUTION OF THE WORK, SHALL BE RELOCATED AS DIRECTED BY ENGINEERS. EXTREME CAUTION SHOULD BE USED BY THE CONTRACTOR WHEN EXCAVATING OR PIER DRILLING AROUND OR NEAR UTILITIES. CONTRACTOR SHALL PROVIDE SAFETY TRAINING FOR THE WORKING CREW.
6. ALL EXISTING INACTIVE SEWER, WATER, GAS, ELECTRIC AND OTHER UTILITIES, WHICH INTERFERE WITH THE EXECUTION OF THE WORK, SHALL BE REMOVED AND SHALL BE CAPED, PLUGGED OR OTHERWISE DISCONTINUED AT POINTS WHICH WILL NOT INTERFERE WITH THE EXECUTION OF THE WORK, SUBJECT TO THE APPROVAL OF ENGINEERING.

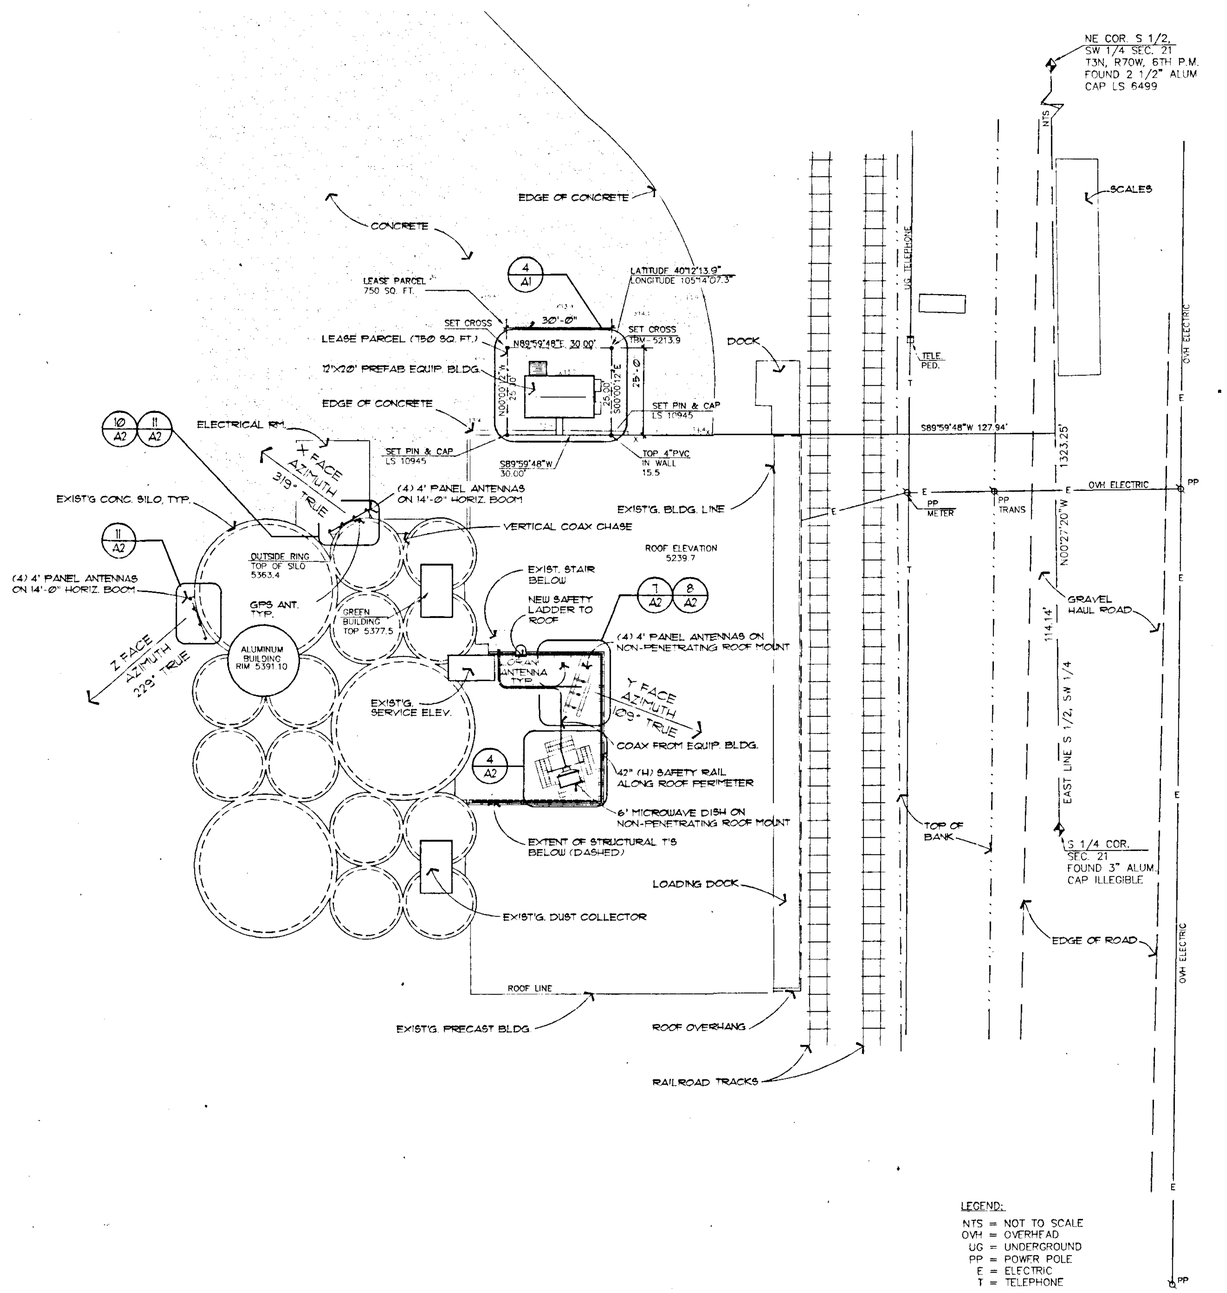

LEGEND:
NTS = NOT TO SCALE
OVH = OVERHEAD
UG = UNDERGROUND
PP = POWER POLE
E = ELECTRIC
T = TELEPHONE

NORTH

1 A1 **SITE PLAN**

SCALE 1" = 20'-Ø"

20 10 Ø 20 40 60 FEET

Stamp

STATE OF COLORADO
REX ALAN CROOK
20548
LICENSED ARCHITECT

T•REX Architex
architecture planning interiors
2135 Fillmore • Suite 260
Denver, Colorado 80206-6003
(303) 388-2918 • fax: (303) 388-0538

Drawings

Drawings and Specifications as instruments of service are and shall remain the property of the Architect whether the Project for which they are made is executed or not. The Owner shall be permitted to retain copies, including reproducible copies, of Drawings and Specifications for information and reference in connection with the Owner's use and occupancy of the Project. The Drawings and Specifications shall not be used by the Owner on other projects, for additions to this Project or for the completion of this Project by others, provided the Architect is not in default under this Agreement, except by agreement in writing and with appropriate compensation to the Architect.

AIRTOUCH Cellular
3305 160th Avenue SE
Second Floor
Bellevue, WA 98008

DATE	ISSUED AS
08-28-97	preliminary
—	zoning-special use permit application
—	construction permit application
—	issued for zoning / construction
—	issued for construction
—	issued zoning & construction permit
—	as built / record set
11-12-97	owner approval

Project Title

DEN-LYONS
ALT. 8
CELL SITE


Southdown Cement Plant
5134 Ute Highway
Thornton, Colorado 80503

Issue Date
11-12-97


Date Revisions

Sheet 1 of 4


A1

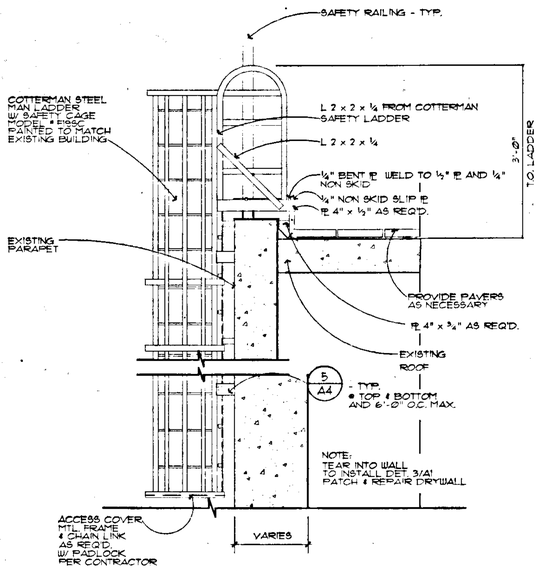


6 A4 **MAN LADDER W/ SAFETY CAGE**
SCALE 1/16" = 1'- 0"

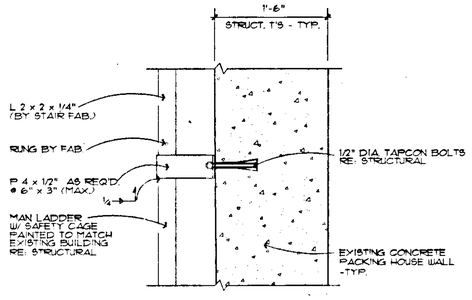


5 A4 **CONNECTION DETAIL**
SCALE 1" = 1'- 0"

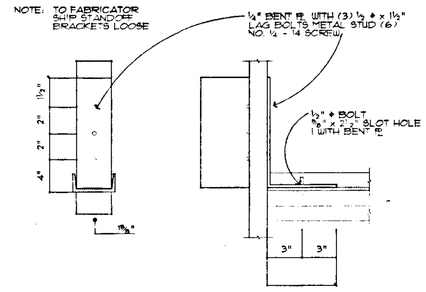


4 A4 **CONNECTION DETAIL**
SCALE 1" = 1'- 0"

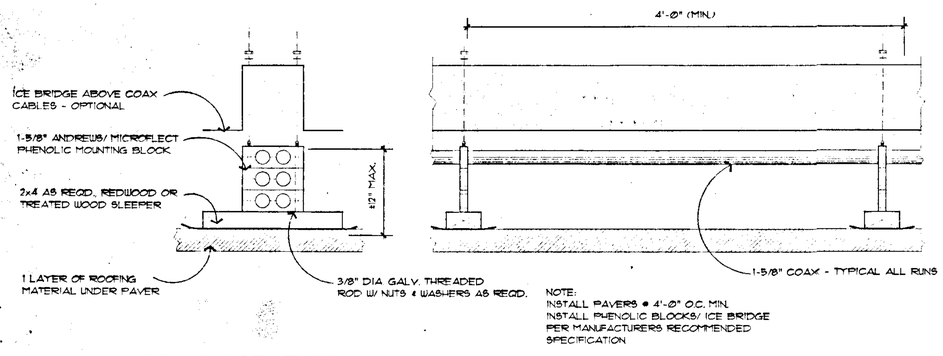

3 A4 **COAX CABLE TRAY** PER CONTRACTOR (AS REQD.)
SCALE 1-1/2" = 1'-0"

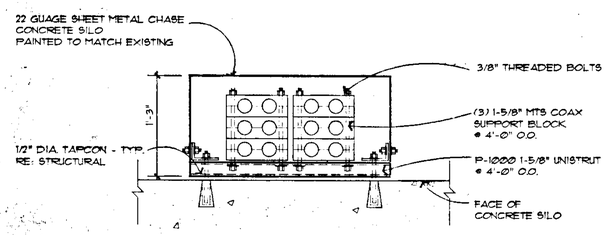

2 A4 **VERTICAL COAX RACEWAY**
SCALE 1-1/2" = 1'- 0"

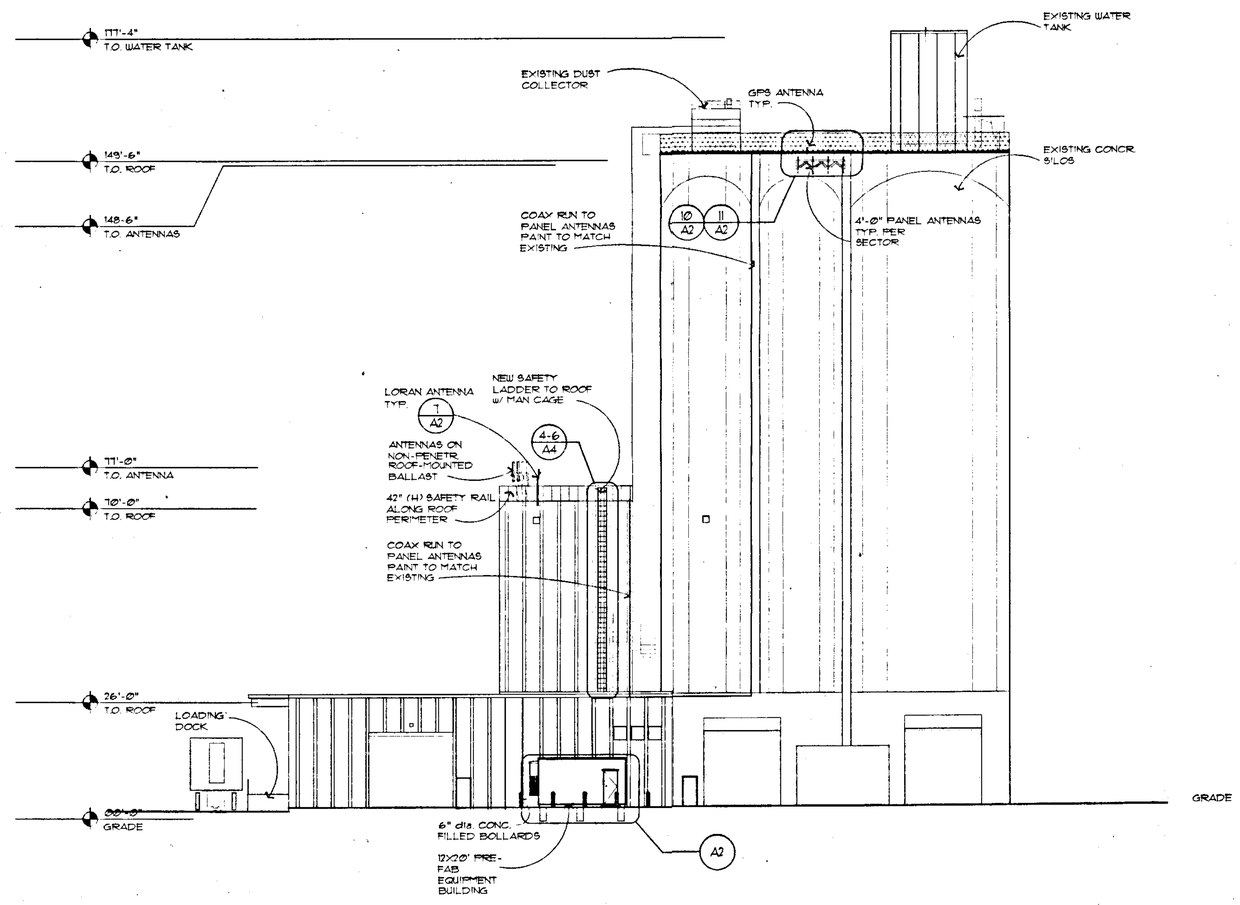

1 A4 **NORTH ELEVATION**
SCALE 1/16" = 1'- 0"

STATE OF COLORADO
REX ALAN CROOK 201548
LICENSED ARCHITECT

T·REX Architex
o architecture o planning o interiors
2135 Fillmore • Suite 260
Denver Colorado 80205-5023
303 388-2915 • fax 303 388-2838

Drawings

Drawings and Specifications as instruments of service are and shall remain the property of the Architect whether the Project for which they are made is executed or not. The Owner shall be permitted to retain copies, including reproducible copies, of Drawings and Specifications for information and reference in connection with the Owner's use and occupancy of the Project. The Drawings and Specifications shall not be used by the Owner on other projects, for additions to this Project or for the completion of this Project by others provided the Architect is not in default under this Agreement, except by agreement in writing and with appropriate compensation to the Architect.

AIRTOUCH Cellular
3305 160th Avenue SE
Second Floor
Bellevue, WA 98008

ISSUED AS	DATE
preliminary	08-28-97
zoning-special use permit application	—
construction permit application	—
issued for zoning / construction	—
issued for construction	—
issued zoning & construction permit	—
as built / record set	—
owner approval	11-12-97

Project Title

DEN-LYONS
ALT. 8
CELL SITE


Southdown Cement Plant
5134 Ute Highway
Thornton, Colorado 80503

Issue Date
11-12-97

Date Revisions


Sheet 4 of 4

A4

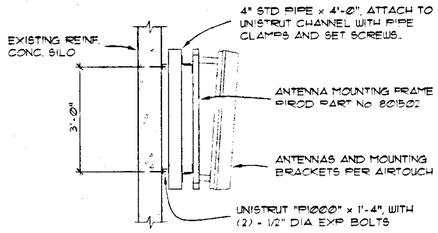


ANTENNA FRAME SUPPORT

SECTION 2 / S-1 — 1/2" = 1'-0"

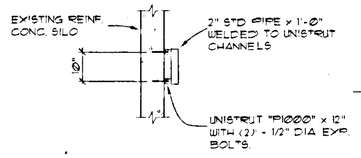


TIEBACK SUPPORT

SECTION 3 / S-1 — 1/2" = 1'-0"

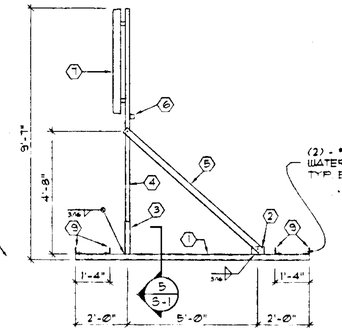

SECTION 4 / S-1 — 3/8" = 1'-0"

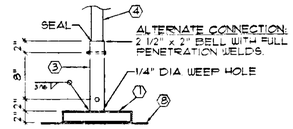

SECTION 5 / S-1 — 1" = 1'-0"

GENERAL NOTES

REINFORCED CONCRETE

GENERAL. Fabrication and construction shall conform to the ACI Building Code, latest edition. Cement shall be Type II as recommended by the Soils Engineer in the report noted below under foundations. Concrete shall have a minimum compressive strength of 3,000 psi in 28 days.

REINFORCEMENT. Reinforcing steel, unless otherwise noted, shall be ASTM A-615-83, Grade 60 except bars to be welded which shall be ASTM A-615-83, Grade 40. Horizontal wall reinforcing shall be made continuous at all corners, or corner bars provided. Provide not less than two #5 bars around all openings in concrete and extend 2'-0" beyond. Bond splices shall be lapped 24 diameters or a minimum of 24 inches. Tack welding will not be permitted on Grade 40 or Grade 60 steel. Splice all bottom reinforcing bars at centerline of caisson and all top reinforcing bars at mid-point between caissons.

CONCRETE PROTECTION FOR REINFORCING

Concrete deposited against ground ..... 3" Min. Cover

Concrete exposed to ground or weather after removal of forms
#5 and smaller bars ..... 1 1/2" Min. Cover
#6 and larger bars ..... 2" Min. Cover

STRUCTURAL STEEL

Fabrication and erection shall conform to the AISC. "Specification For The Design, Fabrication and Erection of Structural Steel For Buildings" (latest edition). Connections shall be standard framed beam connections using ASTM A-307 bolts, unless otherwise noted.

Structural steel is specified as ASTM A-36 for beams and A-46 for columns.

All welding shall be performed by operators qualified in accordance with specifications of the American Welding Society.

Anchor bolts shall be A-307.

All metal (bolts, straps, nails, screws, etc.) exposed to weather shall be galvanized or weather resistance finish as directed by Architect or US West NewVector Group, Inc.

WOOD

Fabrication and erection shall conform to the "National Design Specifications for Stress Grade Lumber and its Fastenings" (latest edition) as recommended by the National Lumber Manufacturers Association Washington, D.C., and the Uniform Building Code - current edition.

All nailing shall be in accordance with Tables 25P and 25Q, Uniform Building Code (latest edition), or in accordance with local building code and standard practice.

All framing members to be Hem Fir No. 2, unless otherwise noted.


Wood exposed to weather or earth shall be pressure-treated or wood with natural resistance to decay.

PREFABRICATED BUILDING

Manufactured by Dupont Building Inc., P. O. Box 13, Cameron, LA. 70631, (318)775-5928.

LIVE LOADS

Roof(snow) ..... 30 PSF Floors ..... 125 PSF
Seismic ..... ZONE 1 Wind (Exposure "C") ..... 100 MPH

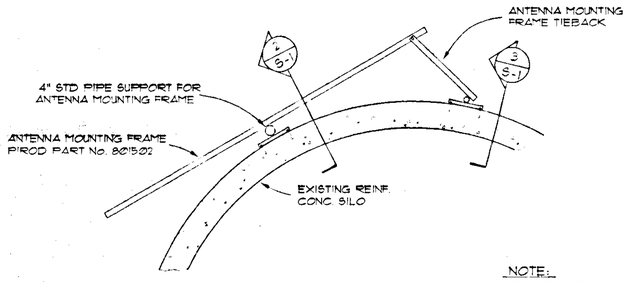


PLAN

SILO ANTENNA MOUNTS

3/8" = 1'-0"

NOTE:
RE. ARCH. DRAWINGS FOR LOCATION AND ORIENTATION OF ANTENNA MOUNTS

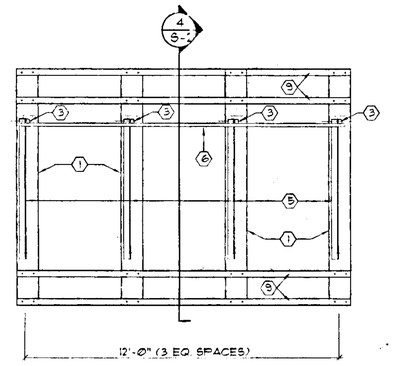


PLAN

"Y" FACE ANTENNA MOUNT

3/8" = 1'-0"

KEY


1. TS12 x 2 x 1/4
2. PL 1/4 x 3 x 0'-6".
3. PIPE 2 1/2 STD WITH (2)-1/2" DIA THROUGH BOLTS.
4. PIPE 2 STD
5. L3 x 3 x 1/4, WITH 1/2" DIA BOLT EACH END.
6. UNISTRUT P1000
7. ANTENNA WITH BRACKETS AND CLAMPS.
8. 1 LAYER 90 POUND MINERAL FELT BETWEEN ANTENNA SUPPORT AND EXISTING ROOF.
9. L 3 x 3 x 1/4 ATTACH TO TS 12 x 2 x 1/4

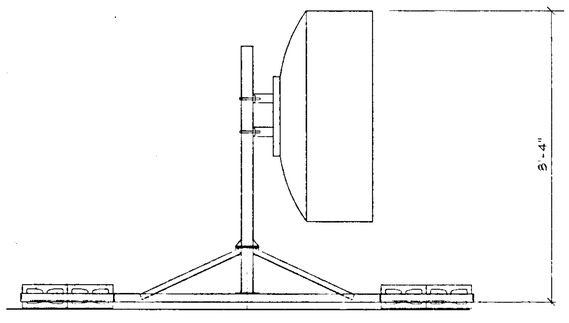

PREENGINEERED ANTENNA MOUNT, BAIRD MODEL BPTS-6 WITH TWO ROWS OF 6 BLOCKS PER LEG FOR A BALLAST WEIGHT OF 1440 POUNDS.


MICROWAVE DISH MOUNT

3/8" = 1'-0"

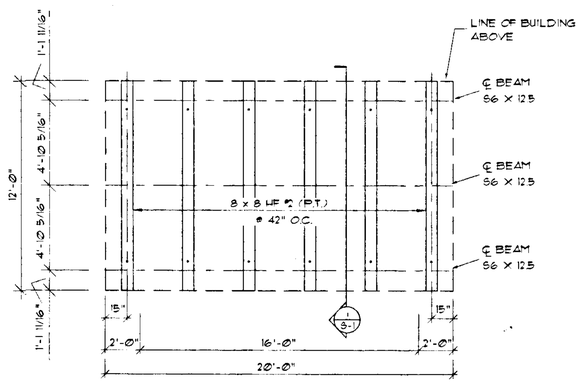

FOUNDATION PLAN (12' X 20')

1/4" = 1'-0"

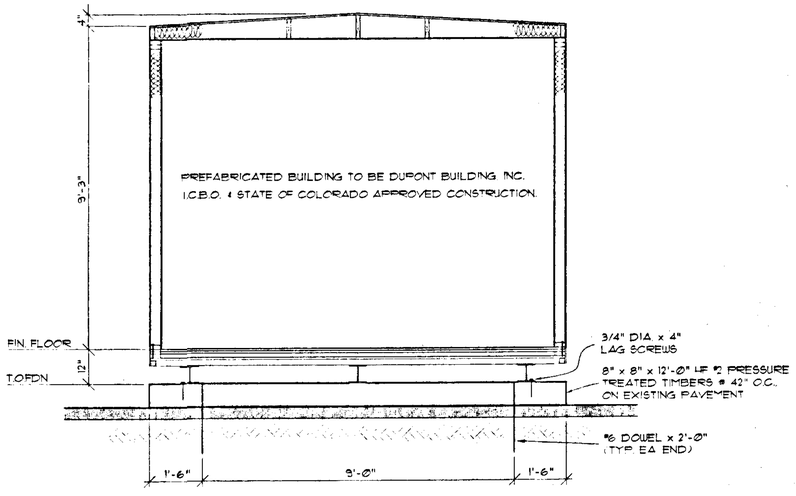

SECTION 1 / S-1 — 1/2" = 1'-0"

TEG PROJECT NO. U07254

THE ENGINEERING GROUP, INC.
7000 SOUTH BROADWAY, STE. 1-D
LITTLETON, CO 80122
(303)798-4794

USWEST NEWVECTOR GROUP
dba: AIRTOUCH CELLULAR
3305 160th Avenue SE
Second Floor
Bellevue, WA 98008

DATE	ISSUED AS
10/20/97	preliminary
11/12/97	PERMIT & CONSTRUCTION
...	...
...	...
...	...
...	...
...	...

Project Title


DEN-LYONS
ALT.8
CELL SITE

Southdown Cement Plant
5134 Ute Highway
Lyons, Colorado 80503

COLORADO REGISTERED PROFESSIONAL ENGINEER
11-12-97
30597

S1


E:\U07\254\S1 Wed Nov 12 12:29:31 1997

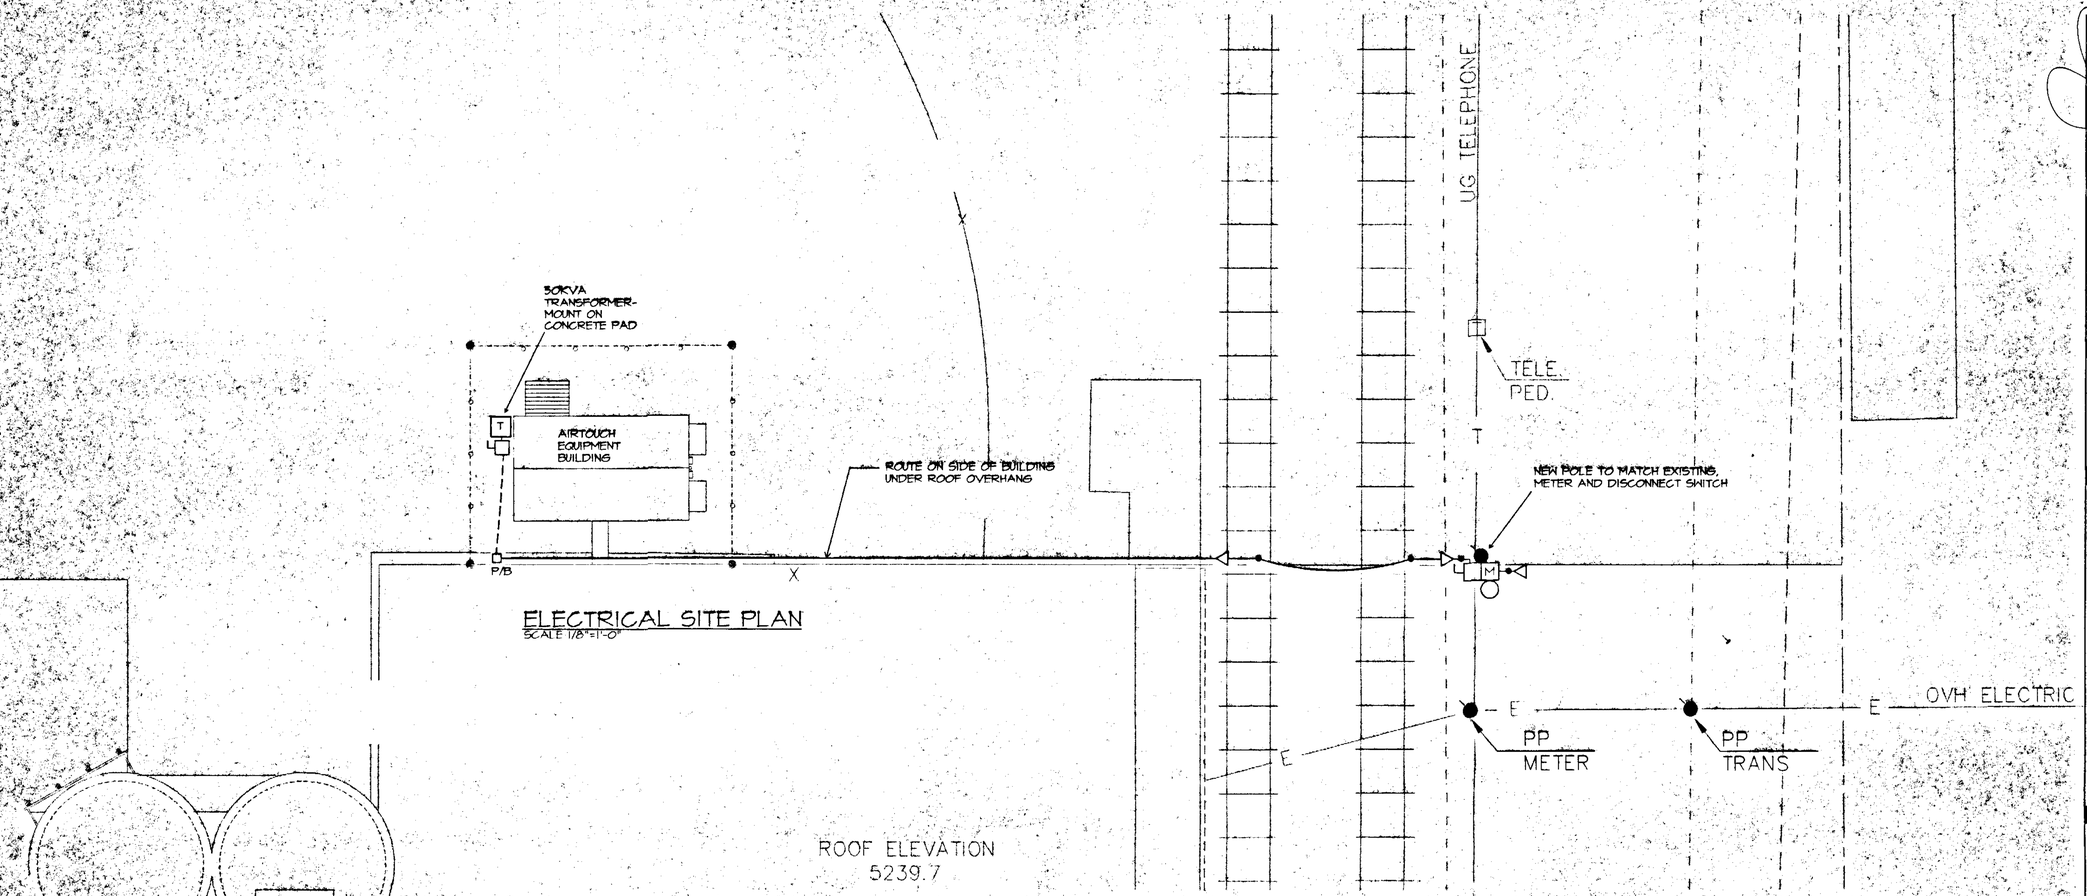


ELECTRICAL SITE PLAN

SCALE 1/8"=1'-0"

ROOF ELEVATION
5239.7

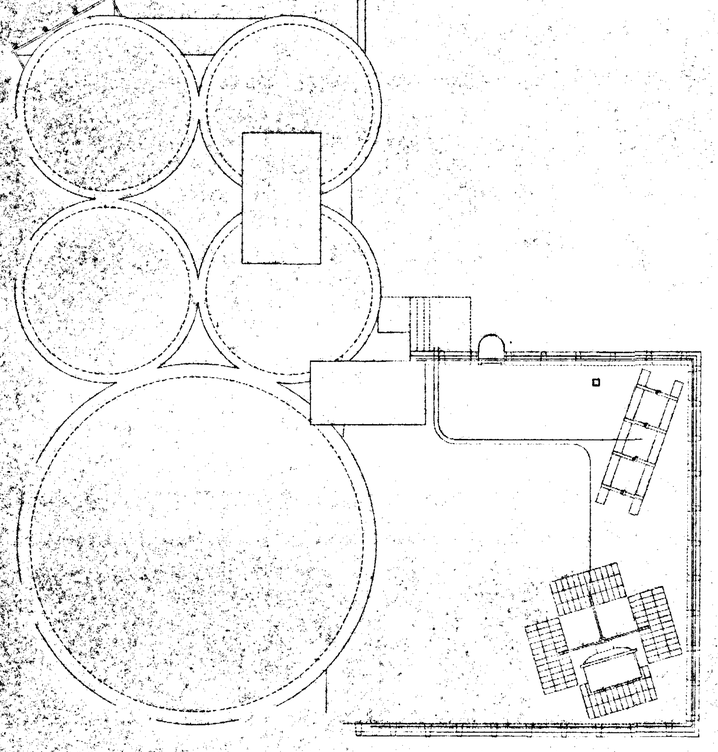

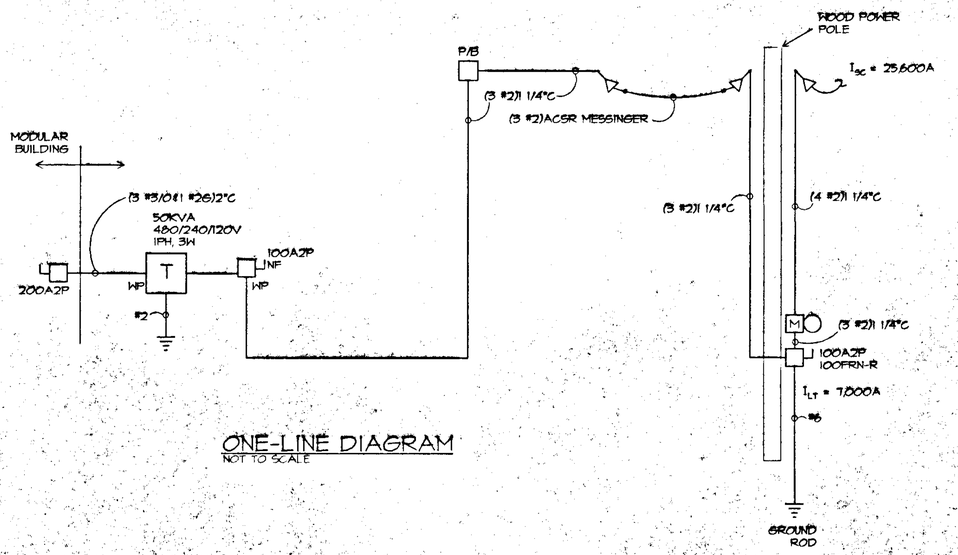

ONE-LINE DIAGRAM

NOT TO SCALE

$$F = \frac{1.73 \times 150 \times 14{,}200}{208 \times 11{,}364} = 1.83$$

$$F = \frac{2 \times 150 \times 14{,}200}{240 \times 11{,}364} = 1.83$$

$$I_{SC} = \frac{14{,}200}{1 + 1.83} = 5{,}627A$$

David M. Kazin & Associates
Consulting Electrical Engineers
8751 E. Hampden Ave., Suite C-2
Denver, Colorado 80231
(303) 671-0816 FAX (303) 671-0837

Stamp

COLORADO REGISTERED DAVID M. KAZIN 20747 PROFESSIONAL ENGINEER

T•REX Architex
architecture planning interiors
235 Fillmore - Suite 250
Denver Colorado 80206-5023
303 388-2916 - fax 303 388-1936

Drawings

Drawings and Specifications as instruments of service are and shall remain the property of the Architect whether the Project for which they are made is executed or not. The Owner shall be permitted to retain copies including reproducible copies, of Drawings and Specifications for information and reference in connection with the Owner's use and occupancy of the Project. The Drawings and Specifications shall not be used by the Owner on other projects, for additions to this Project or for completion of this Project by others provided the Architect is not in default under this Agreement, except with the prior written agreement of the Architect and with appropriate compensation to the Architect.

AIRTOUCH Cellular
3305 160th Avenue SE
Second Floor
Bellevue, WA 98008

DATE	ISSUED AS
---	preliminary
---	zoning, special use permit application
---	construction/permit application
---	issued for zoning / construction
---	issued for construction
---	issued zoning & construction permit
---	as built / record set
---	owner approval

Project Title

DEN-LYONS
ALT. 8
CELL SITE

Southdown Cement Plant
5134 Ute Highway
Thornton, Colorado 80503

Issue Date
09-11-97

Date Revisions

Sheet 1 of 1

E1