
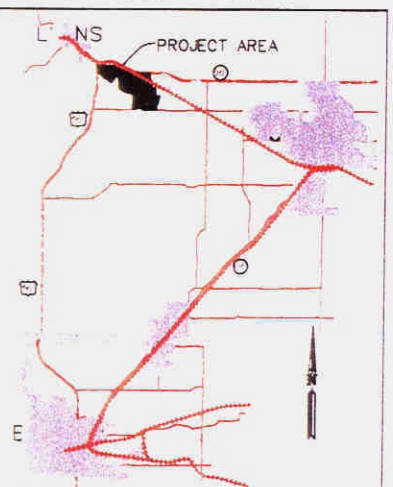
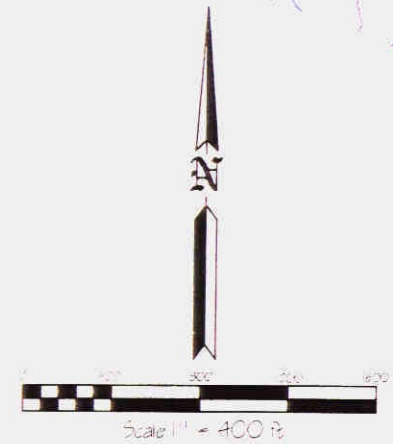


M-74-015

NOTES:

1. THIS RECLAMATION PLAN IS FOR CONCEPTUAL USE ONLY. ADJUSTMENTS WILL NEED TO BE MADE AS NECESSARY IN THE FIELD.
2. RECLAIMED SLOPES WILL VARY BASED UPON OVERBURDEN AND OTHER NON-AGGREGATE MATERIALS AVAILABLE. RECLAIMED SLOPES SHALL NOT EXCEED 3 HORIZ. TO 1 VERT.
3. DITCHES & LATERALS TO BE RE-ALIGNED PER EXISTING WATER RIGHTS.
4. PERIMETER OF EXCAVATED PHASES (I,II,III) SHALL BE CONSTRUCTED WITH COMPACTED BACKFILL IN ORDER TO RETARD GROUND WATER INFILTRATION FROM THE SURROUNDING AQUIFER.
5. THE OUTER STORAGE RESERVOIR LOCATED AT THE FAR SOUTH-EAST END OF PHASE III WILL BE SEALED EITHER WITH COMPACTED BACKFILL OR SOIL BENONITE SLURRY.
6. THE GROUND WATER RECHARGE CHANNEL WILL BE LOCATED NORTH OF HYGIENE RD., BETWEEN THE FOOTHILLS OUTLET CHANNEL AND NORTH OF 61st ST., IN THE AREA OF PHASE III LOCATED EAST OF THE FOOTHILLS RESERVOIR OUTLET CHANNEL. THE GROUND WATER RECHARGE CHANNEL WILL BE CONSTRUCTED NO LATER THAN 12 MONTHS PRIOR TO THE START OF DEWATERING AND MINING OPERATIONS.

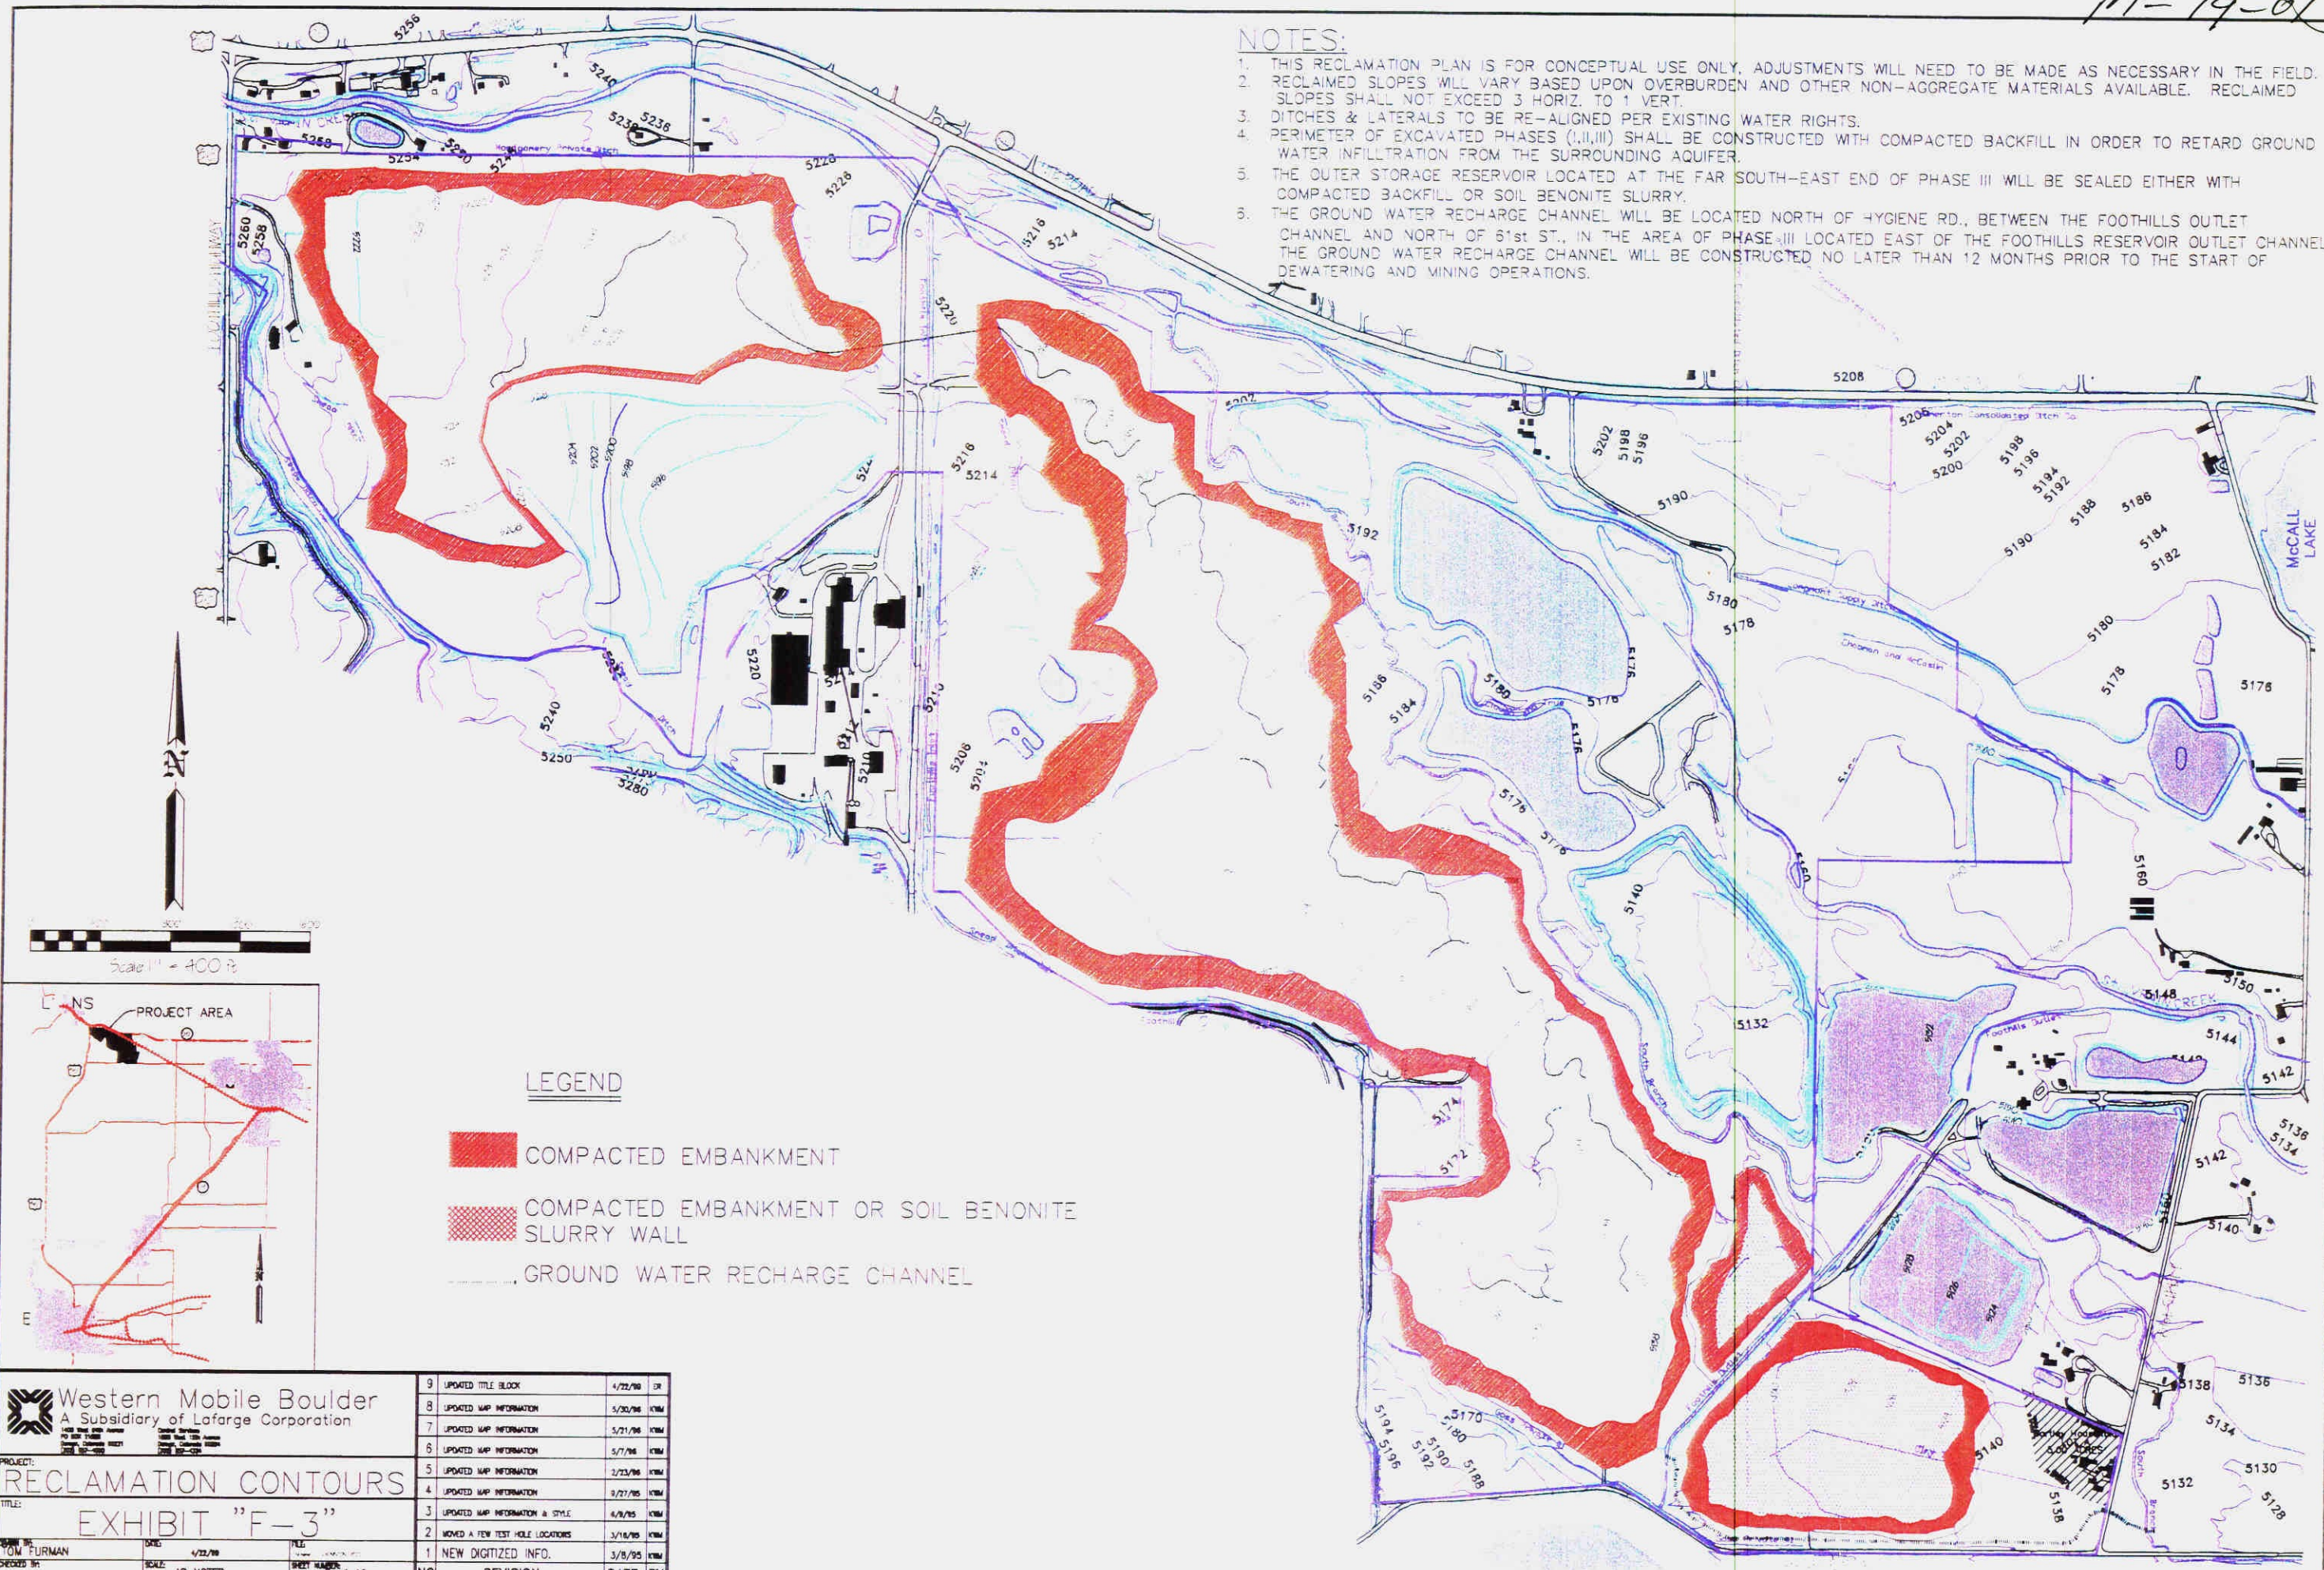

LEGEND

- COMPACTED EMBANKMENT
- COMPACTED EMBANKMENT OR SOIL BENONITE SLURRY WALL
- GROUND WATER RECHARGE CHANNEL

 Western Mobile Boulder A Subsidiary of Lafarge Corporation	9	UPDATED TITLE BLOCK	4/22/90	DR
	8	UPDATED MAP INFORMATION	5/30/90	KRM
	7	UPDATED MAP INFORMATION	5/21/90	KRM
	6	UPDATED MAP INFORMATION	5/7/90	KRM
	5	UPDATED MAP INFORMATION	2/23/90	KRM
	4	UPDATED MAP INFORMATION	9/27/89	KRM
	3	UPDATED MAP INFORMATION & STYLE	6/9/89	KRM
	2	MOVED A FEW TEST HOLE LOCATIONS	3/16/89	KRM
	1	NEW DIGITIZED INFO.	3/8/89	KRM
NO		REVISION	DATE	BY
PROJECT: RECLAMATION CONTOURS				
TITLE: EXHIBIT "F-3"				
DESIGNED BY: TOM FURMAN	DATE: 4/22/90	FILE: 10000000		
CHECKED BY:	SCALE: AS NOTED	SHEET NUMBER: 8 of 12		

0016983