



## Land Use

Courthouse Annex • 2045 13th Street • Boulder, Colorado 80302 • Tel: 303.441.3930 • Fax: 303.441.4856  
Mailing Address: P.O. Box 471 • Boulder, Colorado 80306 • [www.bouldercounty.org](http://www.bouldercounty.org)

October 24, 2011

Dave Closser  
Closser Consulting LLC  
4628 Gordon Dr.  
Boulder, CO 80305

Re: SPR-97-160 Modification Request

Dear Dave,

Land Use staff has reviewed your request to modify the approval of SPR-97-160. Staff understands that the proposed upgrade involves bringing fiber phone service to the equipment shelter at the base of the silos. This fiber will replace the existing copper phone service to the site and will be located underground. Additionally an antenna upgrade is proposed. Currently, there are 3 identical sets of Verizon Wireless antennas at the site. Two sets are up high on the silos, one facing west the other facing north. The third set is on a lower attached building facing east. At this time, Verizon Wireless would like to add 2 new antennas to each existing set of 4. The two new antennas will provide coverage for LTE/4G. Some coaxial cable will also be run between the equipment shelter on the ground and the new antennas.

The Verizon facilities were approved through SPR-97-160 and constructed per BP-97-1785. SPR-97-160 approved the location of three arrays of four antennas (two arrays on the silos and one array on the roof of the upper pack house). In addition, a 6' diameter dish antenna was approved to be located on the roof of the upper pack house and an (12'x 20') equipment shelter to be located on the ground immediately adjacent to the north wall of the pack house. Staff has determined that due to the highly industrial nature of this site and its relative isolation the land use impacts of the additional antenna are insubstantial and with the conditions listed below the proposed modification can be considered minor.

It is unclear to staff why these facilities were permitted through the site plan review process rather than the special use process as is required by the Land Use Code for Telecommunications Facility exceeding the height of the zone district limits. Further changes to this facility may not be considered minor and at such time a special use approval shall be required.

The following conditions shall apply to this minor modification approval:

1. Any vegetated areas disturbed during the upgrade construction shall be revegetated.
2. All antenna support structures and wiring shall be mounted as flush to the silo wall as possible and shall be painted to match the existing structure.
3. A building permit for the project shall be obtained and completed.
4. Documentation of the property owner's approval of this modification shall be provided prior to the issuance of a building permit.

If I may be of further assistance, please call me at 720-494-2641.

Regards,



Hannah L. Hippely, Senior Planner

## Hippely, Hannah

---

**From:** DCLOSSER@aol.com  
**Sent:** Monday, October 24, 2011 11:48 AM  
**To:** Hippely, Hannah  
**Subject:** Re: Verizon Wireless - Cemex in Lyons  
**Attachments:** DenLyonsDS3LTECdRevB\_091911.pdf

Hannah, I attach the drawing set depicting the proposed site upgrades. There are two main components to this upgrade which will make the site LTE/4G capable. The first I mentioned briefly when we spoke this morning. It involves bringing buried fiber phone service to our equipment shelter at the base of the silos. This fiber will replace the existing copper phone service to the site, providing the greatly increased bandwidth required for 4G/LTE. This is best seen on page A1.0 of the attached drawing set. It will be all underground, no visual impact.

The second component is the antenna upgrade we've been discussing. There are 3 identical sets of Verizon Wireless antennas at the site. Two sets are up high on the silos, one facing West the other facing North. The third set is on a lower attached building facing East. At this time Verizon Wireless would like to add 2 new antennas to each existing set of 4. The two new antennas will provide coverage for LTE/4G. The existing and proposed antenna configurations are best seen on page A2.2 of the attached drawing set. We'll also need to run some additional coaxial cable between our equipment shelter on the ground and the new antennas.

Let me know if there's any additional information you require.

Dave

Dave Closser  
Closser Consulting LLC  
4628 Gordon Dr.  
Boulder, CO 80305  
303-554-5627 office  
303-859-1080 mobile

In a message dated 10/24/2011 11:02:03 A.M. Mountain Daylight Time, [hhippely@bouldercounty.org](mailto:hhippely@bouldercounty.org) writes:

Hi Dave, Could you send the materials related to the Verizon proposal at the Cemex plant that we discussed this morning?

Thanks,

Hannah

---

Hannah L. Hippely, AICP

Senior Planner  
Boulder County Land Use Department  
PO Box 471 | Boulder CO 80306 | 303-441-3930  
[hhippely@bouldercounty.org](mailto:hhippely@bouldercounty.org)

**From:** DCLOSSER@aol.com [mailto:DCLOSSER@aol.com]  
**Sent:** Tuesday, October 18, 2011 5:25 PM


**To:** Hippely, Hannah  
**Subject:** Verizon Wireless - Cemex in Lyons

Hannah,


After we spoke earlier I spoke with my colleague Ann Closser who handled the original zoning for this project in 1997. She had records of pretty much everything she did on this. I attach a letter received by County Planning on 7/31/97. I'll bring the remainder of the information included the original zoning submittal package to our Monday meeting.

Dave

Dave Closser  
Closser Consulting LLC  
4628 Gordon Dr.  
Boulder, CO 80305  
303-554-5627 office  
303-859-1080 mobile

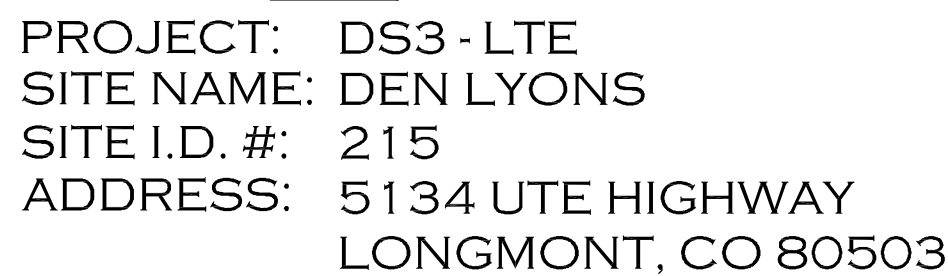

## GENERAL NOTES

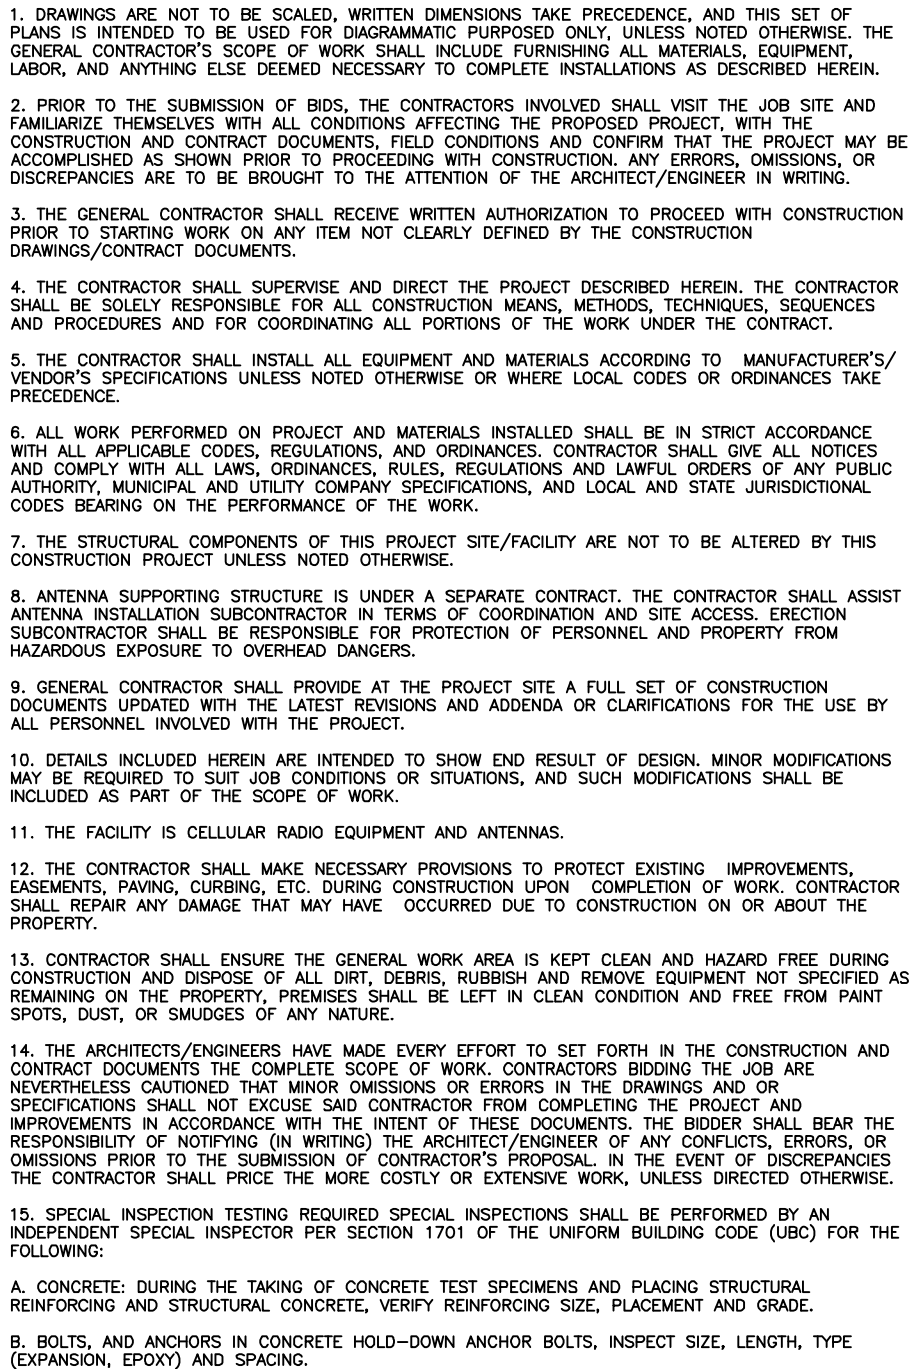**CLIENT**

VERIZON WIRELESS  
CONSTRUCTION MANAGER  
LARRY OTTERSTEIN  
3131 S. VAUGHN WAY  
SUITE 550  
AURORA, CO 80014  
CELL: 303.653.8000  
DESK: 303.873.2726

**ARCHITECT:**

**CHARLES STECKLY**  
CSAi  
5935 S. ZANG ST.  
SUITE 280  
LITTLETON, CO 80127  
PHONE: 303.932.9974  
FAX: 303.932.6561

**CIVIL SURVEYOR:**

**CALVADA**  
**SURVEYING & ENGINEERING**  
**56 INVERNESS DRIVE EAST**  
**STE. 100**  
**ENGLEWOOD, CO 80112**  
**PHONE: 720.488.1303**  
**FAX: 720.488.1306**

**LEC:**

BARTON GARNER  
QWEST  
LONGMONT, CO  
PHONE: 303.255.6122

## RF ENGINEER

VERIZON WIRELESS  
DAVID BORN  
SENIOR RF ENGINEER  
3131 S. VAUGHN WAY  
SUITE 550 AURORA, CO  
80014 PHONE:  
303.829.0002

## DRAWING INDEX

| SHEET | DESCRIPTION            |
|-------|------------------------|
| T1.0  | TITLE SHEET            |
|       |                        |
| LS1   | LAND SURVEY (PENDING)  |
|       |                        |
| A1.0  | SITE PLAN              |
| A1.1  | ENLARGED SITE PLAN     |
| A2.0  | EQUIPMENT ROOM PLAN    |
| A2.1  | EQUIPMENT DETAILS      |
| A2.2  | ANTENNA PLAN & RF DATA |
| A3.0  | ELEVATION              |
| A4.0  | DETAILS                |
|       |                        |
|       |                        |
## VICINITY MAP

JURISDICTION: - BOULDER COUNTY

ZONING DESIGNATION: - G1

OCCUPANCY GROUP: - U


CONSTRUCTION TYPE: - V-B

FULLY SPRINKLERED: - N/A

NO. OF STORIES: - N/A

GOVERNING CODES:  
2009 IBC, 2009 IMC, 2009 IFC, 2009 IECC 2008 NEC

A.D.A. COMPLIANCE:  
THIS FACILITY IS UNMANNED AND NOT FOR HUMAN HABITATION.

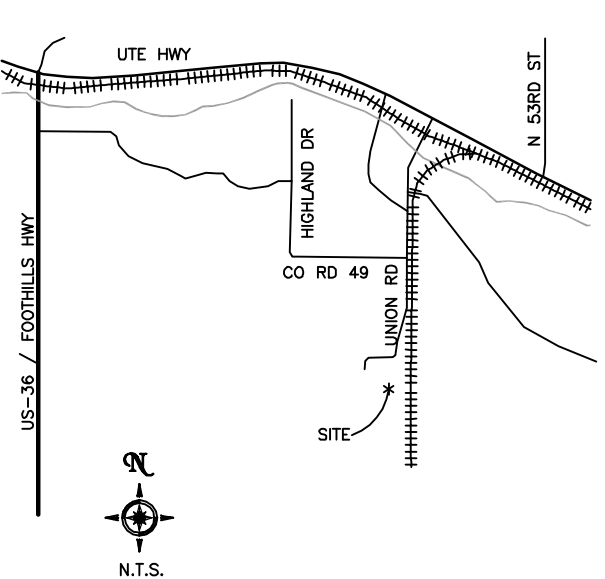

## DIRECTIONS TO SITE

SITE AUDIT FOR FIBER INSTALLATION. REMOVE & REPLACE ANTENNAS. ADD 6 ANTENNAS AND NEW COX.

HEAD WEST ON S. VAUGHN WAY. TURN LEFT ONTO THE  
COLORADO 83 N RAMP TO I-225. MERGE ONTO S. PARKER  
ROAD. TAKE THE I-225 N RAMP. KEEP RIGHT AT FORK. FOLLOW  
SIGNS FOR I-225 N AND MERGE ONTO I-225 N. TAKE EXIT  
12A ON THE LEFT TO MERGE ONTO I-70 W TOWARD DENVER.  
SLIGHT RIGHT ONTO I-270 W (SIGNS FOR FORT COLLINS)  
CONTINUE ONTO US-36 W. TURN RIGHT ONTO US-66/UTE HWY.  
DESTINATION WILL BE ON THE RIGHT.

### APPROVAL BLOCK

CONTRACTOR SHALL VERIFY ALL PLANS AND EXISTING DIMENSIONS AND CONDITIONS ON THE JOB SITE AND SHALL IMMEDIATELY NOTIFY THE ARCHITECT IN WRITING OF ANY DISCREPANCIES BEFORE PROCEEDING WITH THE WORK OR BE RESPONSIBLE FOR SAME.

THESE DRAWINGS ARE ONLY TO SCALE WHEN PLOTTED ON 24x36 SHEET. USE GRAPHIC SCALE WHEN PLOTTED ON 11x17 SHEET.


CALL BEFORE YOU DIG - COLORADO LAW REQUIRES 3 WORKING  
DAYS NOTICE FOR CONSTRUCTION PHASE.  
UTILITY NOTIFICATION CENTER OF COLORADO - 1-800-922-1987

THESE DRAWINGS MAY NOT SHOW ALL UNDERGROUND PIPING AND UTILITIES. THE CONTRACTOR SHALL EXERCISE EXTREME CARE DURING ALL EXCAVATION AND OTHER CONSTRUCTION ACTIVITIES.

CONTRACTOR IS RESPONSIBLE FOR ALL UTILITY LOCATES AND UTILITY RELOCATIONS REQUIRED FOR THIS INSTALLATION. CONTRACTOR SHALL SCHEDULE AND COORDINATE ALL WORK WITH THE OWNER TO ENSURE NO DISRUPTION TO OWNERS OPERATIONS.

| TITLE             | SIGNATURE | DATE |
|-------------------|-----------|------|
| OWNER             |           |      |
| ENGINEER          |           |      |
| CONSTRUCTION MGR. |           |      |
| PROJECT MANAGER   |           |      |
|                   |           |      |

ACKNOWLEDGMENT OR "SIGN-OFF" BY PARTIES TO THE CONSTRUCTION DRAWINGS DOES NOT CONSTITUTE ALTERATION OF THE LEASE TERMS.

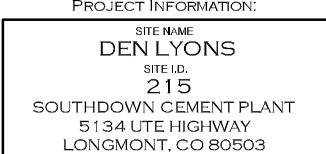[illegible]

PLANS PREPARED BY:

**CSAi**  
**CHARLES STECKLY ARCHITECTURE, Inc.**  
 ARCHITECTURE — PLANNING — DESIGN  
 5935 SOUTH ZANG STREET, SUITE 280  
 LITTLETON, COLORADO 80127  
 OFFICE: 303.932.9974  
 FAX: 303.932.6561

LICENSURE NO:

|           |      |      |
|-----------|------|------|
| DRAWN BY: | CHK: | APV: |
| JTT       | TN   | CS   |

CONSULTANT:


SHEET TITLE:

# TITLE SHEET

SHEET NUMBER:

# T1.0

M:\2011\Projects\Verizon Wireless LTE\DEN Lyons\CD\A10.dwg  
PLOTTED Sep 19, 2011 AT 2:29pm

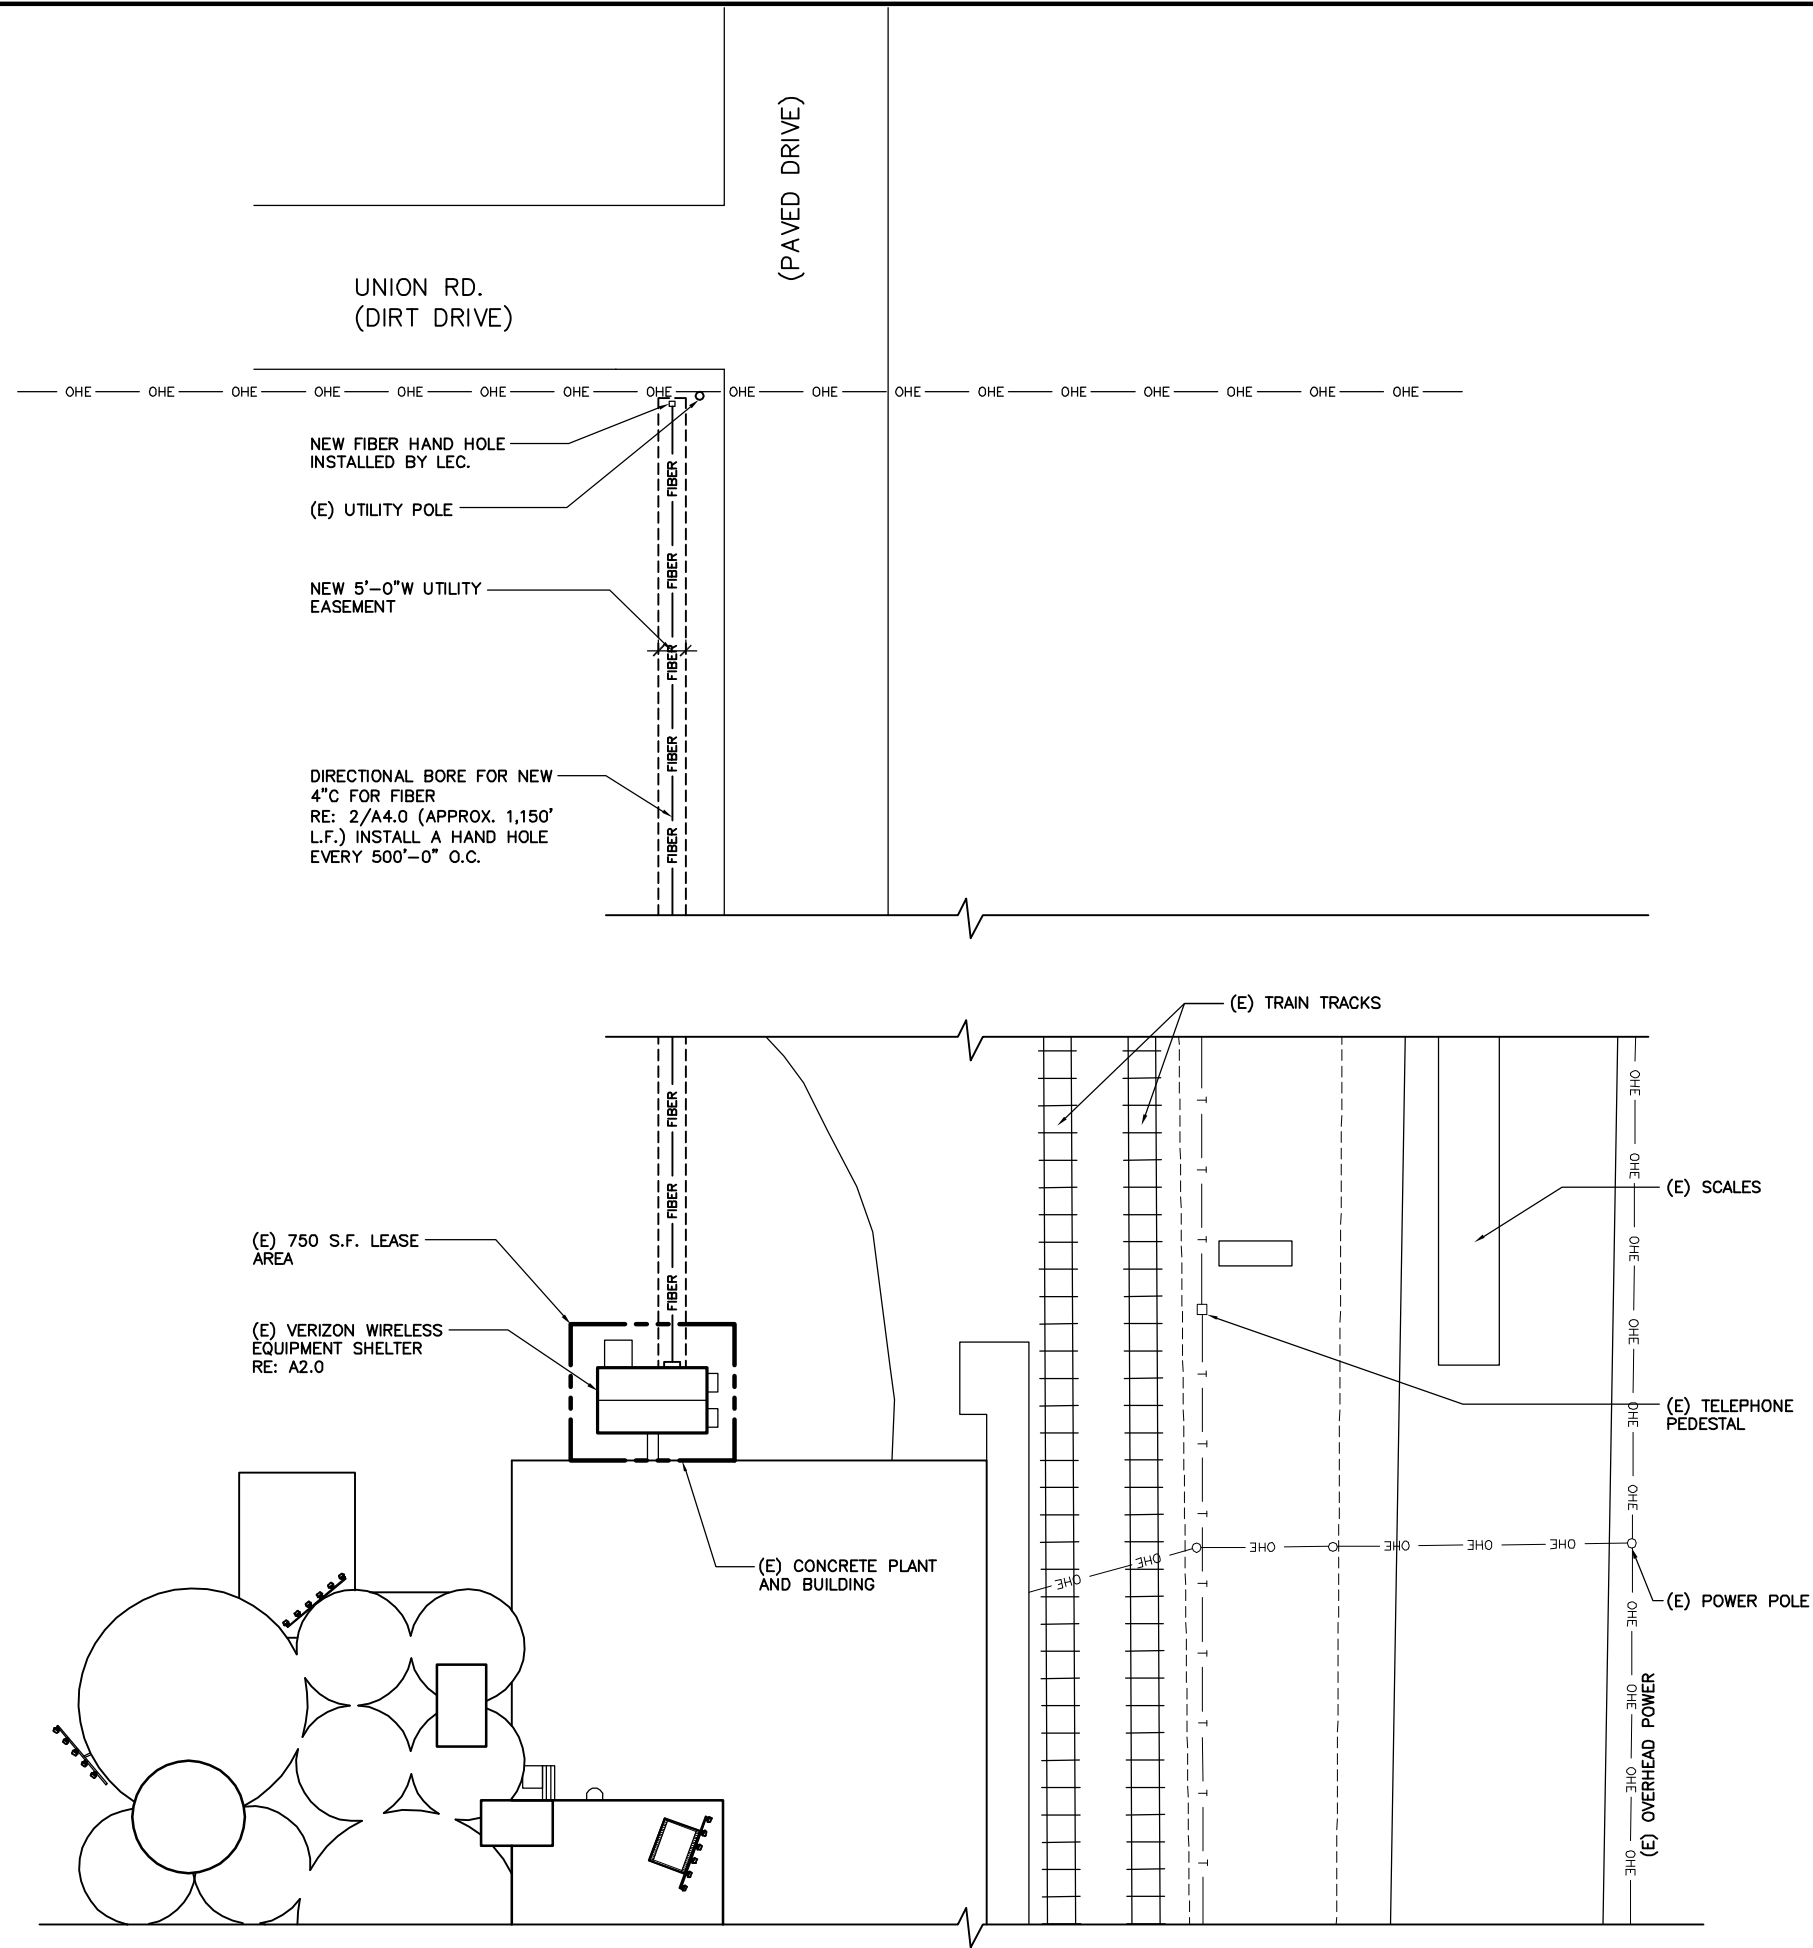

**verizon wireless**

VERIZON WIRELESS SERVICES  
3131 S. VAUGHN WAY, SUITE 550  
AURORA, CO 80014  
PHONE: 303.873.2800

PROJECT INFORMATION:

SITE NAME  
**DEN LYONS**

SITE ID.  
**215**

SOUTHDOWN CEMENT PLANT  
5134 UTE HIGHWAY  
LONGMONT, CO 80503

| REV: | DATE:    | DESCRIPTION:    | BY: |
|------|----------|-----------------|-----|
| A    | 08/08/11 | CD REVIEW       | SSB |
| B    | 09/19/11 | CLIENT COMMENTS | JTT |
|      |          |                 |     |
|      |          |                 |     |
PLANS PREPARED BY:

**CSAi**  
CHARLES STECKLY ARCHITECTURE, Inc.

ARCHITECTURE - PLANNING - DESIGN  
5935 SOUTH ZANG STREET, SUITE 280  
LITTLETON, COLORADO 80127  
OFFICE: 303.932.9974  
FAX: 303.932.6561

LICENSURE NO:

| DRAWN BY: | CHK: | APV: |
|-----------|------|------|
| JTT       | TN   | CS   |

CONSULTANT:

SHEET TITLE:

**SITE  
PLAN**

SHEET NUMBER:


**A1.0**



SCALE:  
1/16" = 1'-0"

16' 8' 0 16'

M:\2011\Projects\Verizon Wireless LTE\DEN Lyons\CD\A11.dwg  
PLOTTED Sep 19, 2011 AT 2:29pm

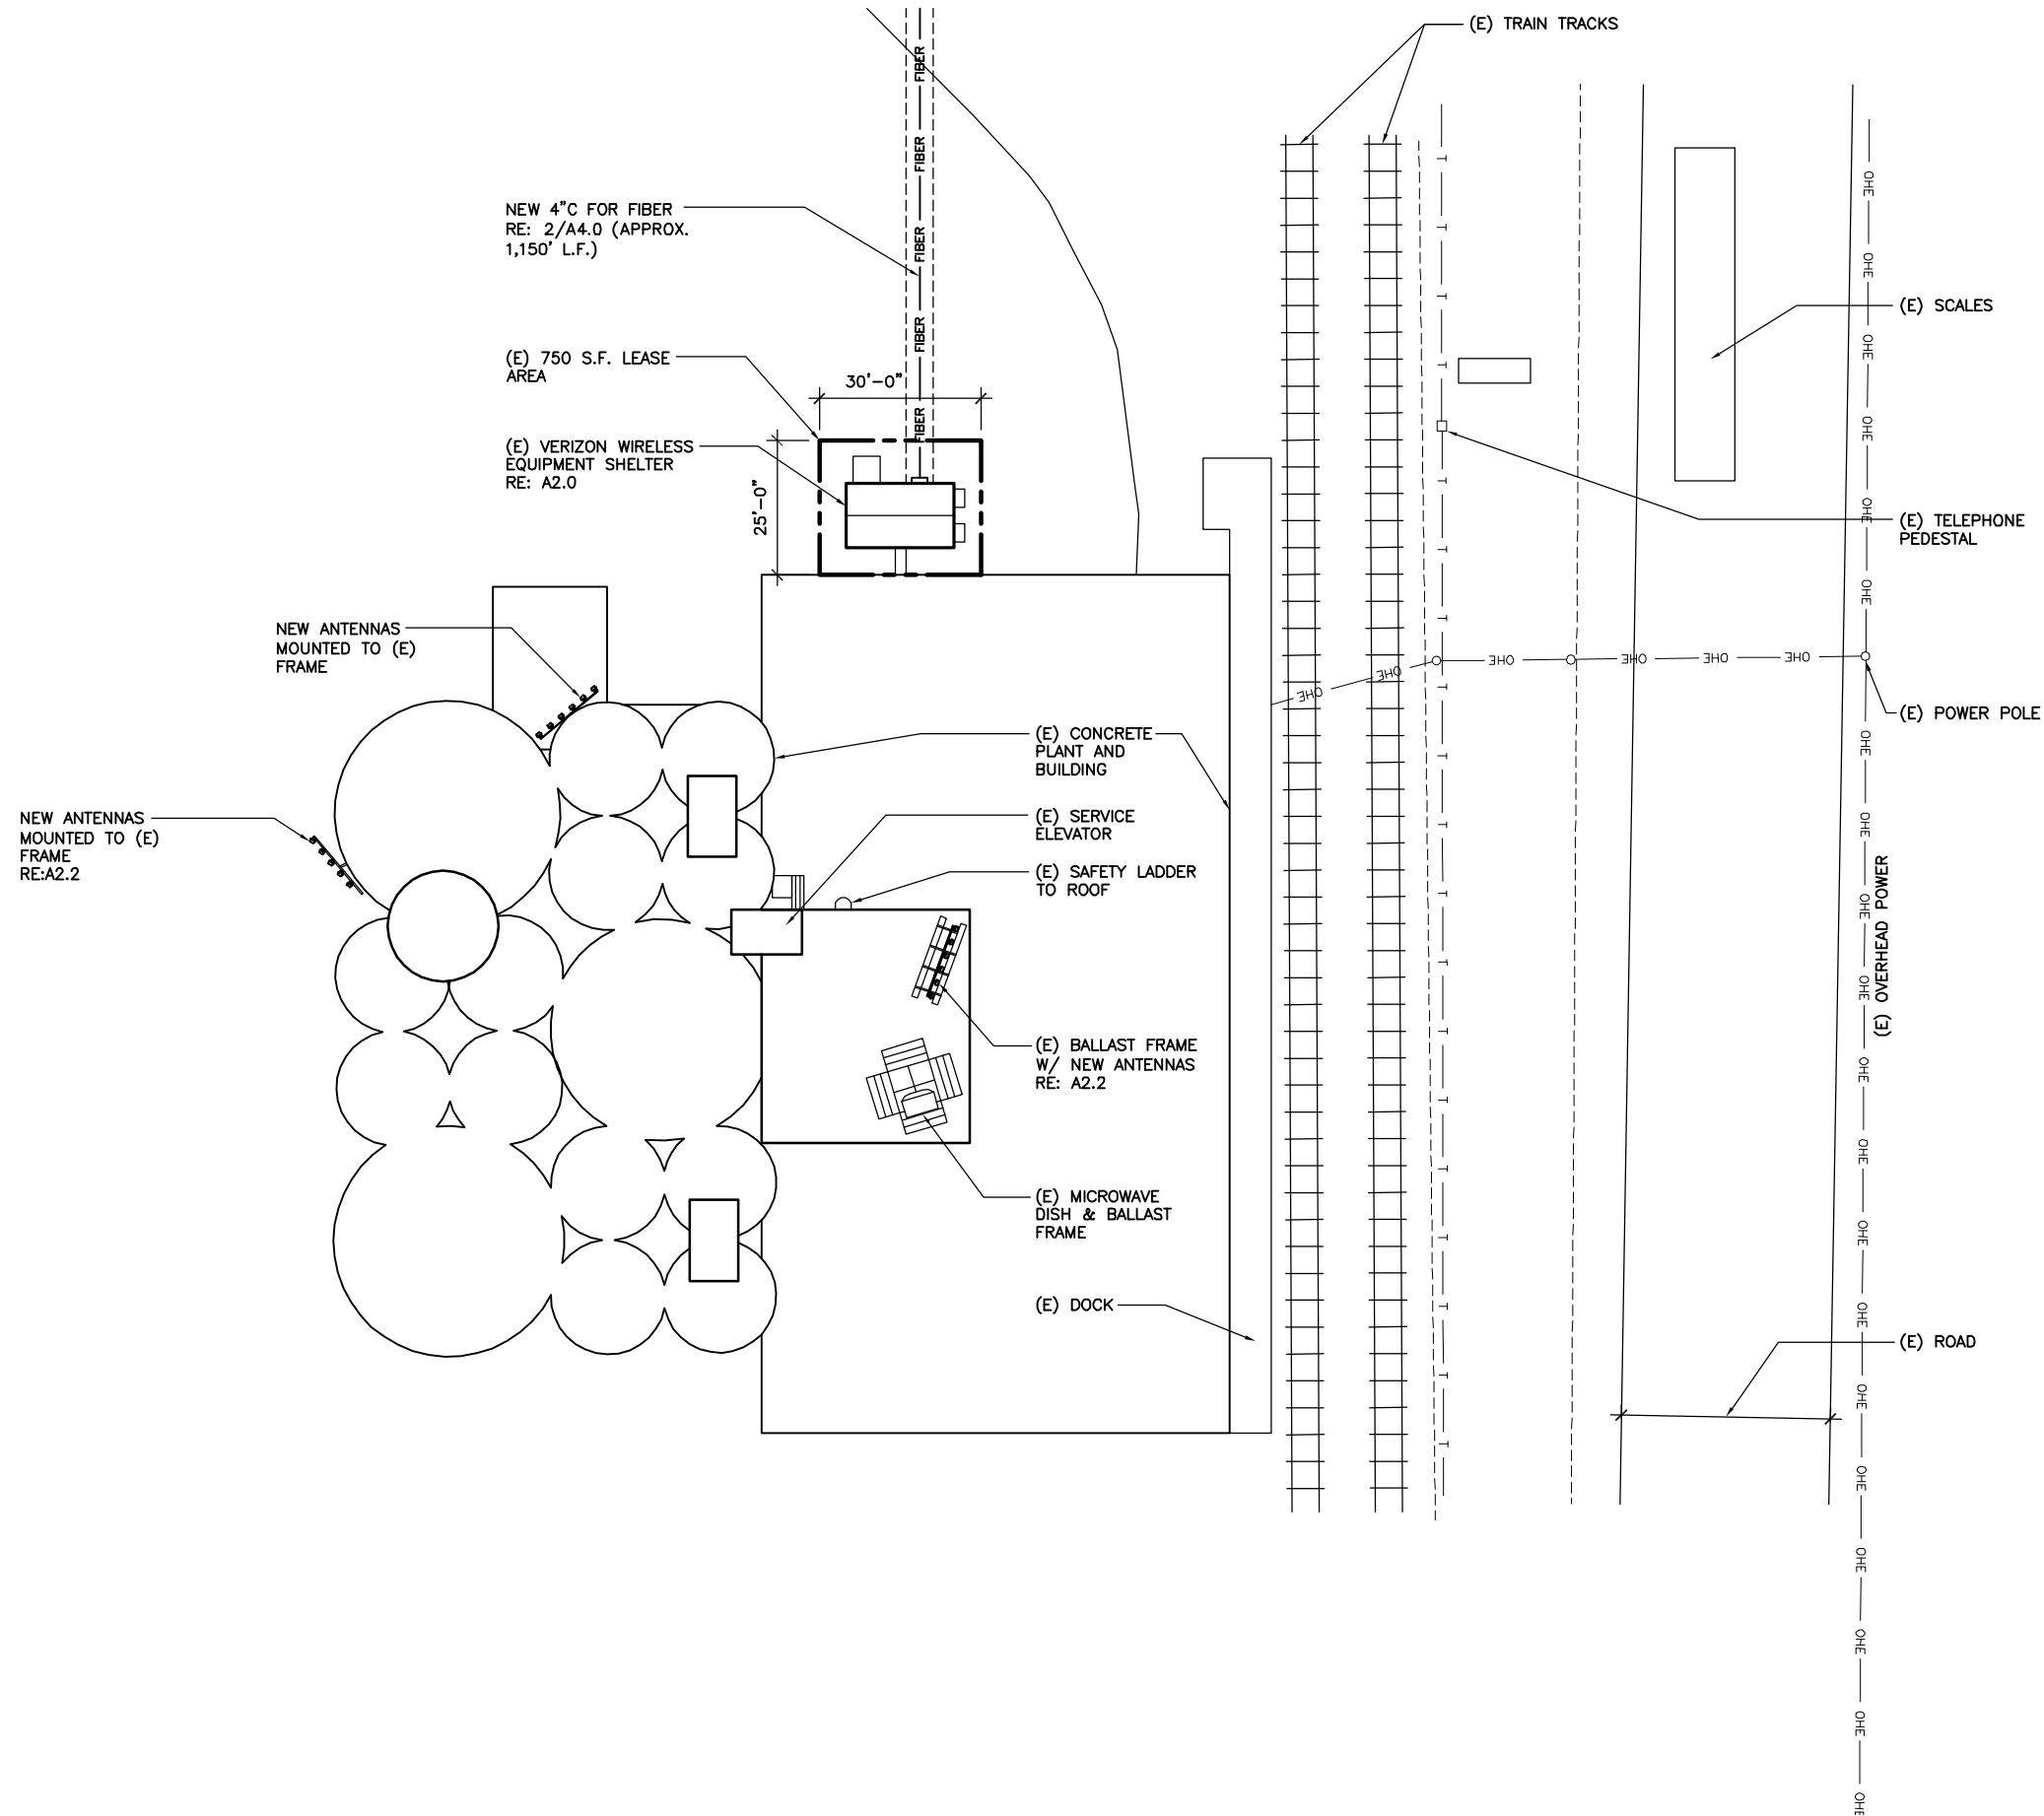

SCALE:  
1/16" = 1'-0"

16' 8' 0 16'

**verizon wireless**

VERIZON WIRELESS SERVICES  
3131 S. VAUGHN WAY, SUITE 550  
AURORA, CO 80014  
PHONE: 303.873.2800

PROJECT INFORMATION:

SITE NAME  
**DEN LYONS**

SITE ID.  
**215**

SOUTHDOWN CEMENT PLANT  
5134 UTE HIGHWAY  
LONGMONT, CO 80503

| REV: | DATE:    | DESCRIPTION:    | BY: |
|------|----------|-----------------|-----|
| A    | 08/08/11 | CD REVIEW       | SSB |
| B    | 09/19/11 | CLIENT COMMENTS | JTT |
|      |          |                 |     |
|      |          |                 |     |
PLANS PREPARED BY:

**CSAi**  
CHARLES STECKLY ARCHITECTURE, Inc.

ARCHITECTURE - PLANNING - DESIGN  
5935 SOUTH ZANG STREET, SUITE 280  
LITTLETON, COLORADO 80127  
OFFICE: 303.932.9974  
FAX: 303.932.6561

LICENSURE NO:

|           |      |      |
|-----------|------|------|
| DRAWN BY: | CHK: | APV: |
| JTT       | TN   | CS   |

CONSULTANT:

SHEET TITLE:

**ENLARGED SITE  
PLAN**

SHEET NUMBER:

**A1.1**

PROJECT INFORMATION:

SITE NAME  
DEN LYONS  
SITE I.D.  
215  
SOUTHDOWN CEMENT PLANT  
5134 UTE HIGHWAY  
LONGMONT, CO 80503

[illegible]

PLANS PREPARED BY:

**CSAi**  
**CHARLES STECKLY ARCHITECTURE, Inc.**  
 ARCHITECTURE — PLANNING — DESIGN  
 5935 SOUTH ZANG STREET, SUITE 280  
 LITTLETON, COLORADO 80127  
 OFFICE: 303.932.9974  
 FAX: 303.932.6561

LICENSURE No:

|           |      |      |
|-----------|------|------|
| DRAWN BY: | CHK: | APV: |
| JTT       | TN   | CS   |



CONSULTANT:

SHEET TITLE:

## EQUIPMENT PLANS

SHEET NUMBER:

## A2.0

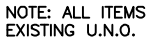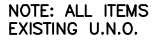









\\ms2011\Projects\Verizon Wireless LTE\DEN Lyons\CD\A22.dwg  
PLOTTED Sep 19, 2011 AT 5:08pm

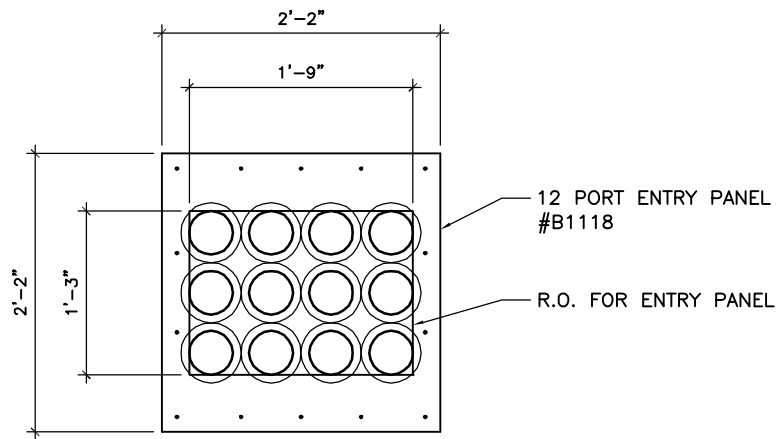

4 NEW ENTRY PORT DETAIL

SCALE:  
N.T.S.

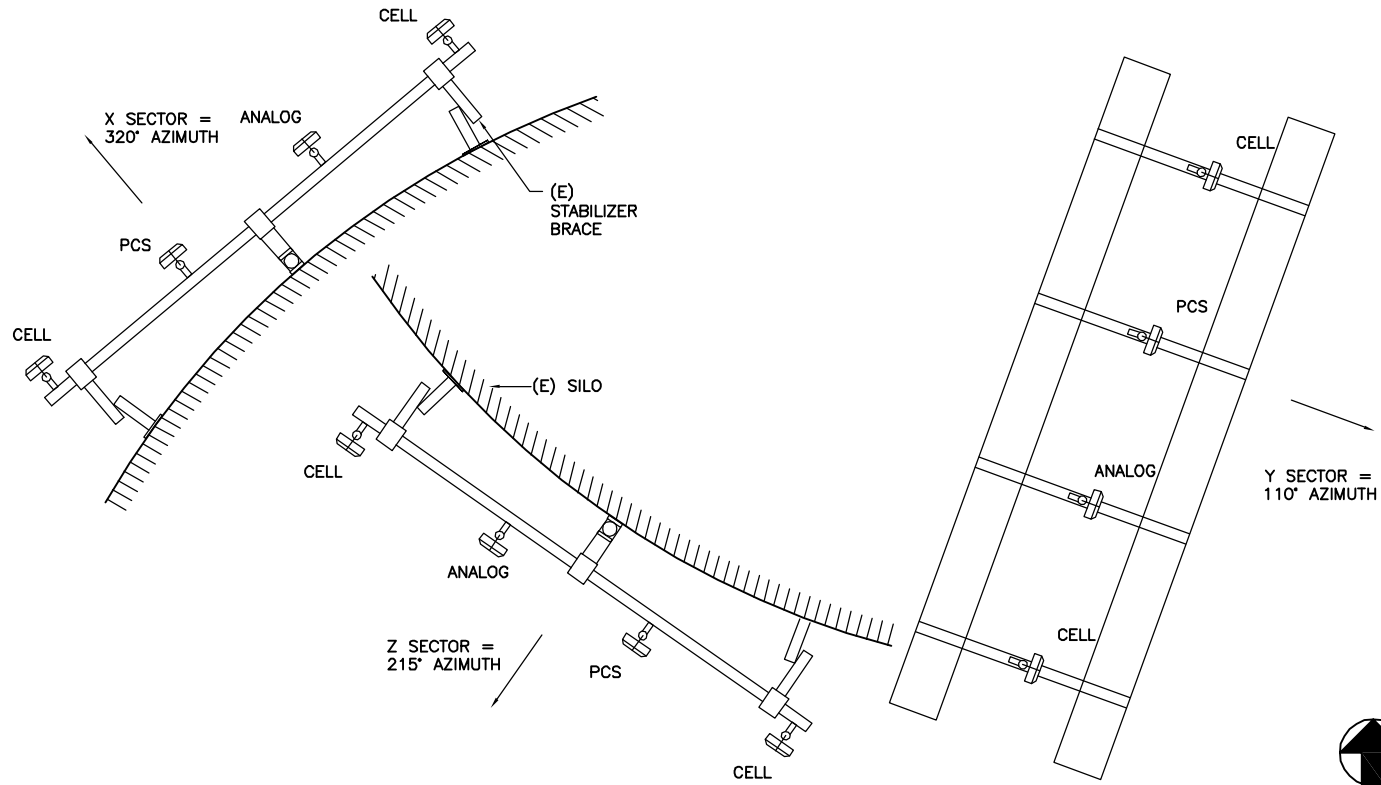

2 EXISTING ANTENNA CONFIGURATION


SCALE:  
N.T.S.

1. GENERAL: PROVIDE ALL LABOR, EQUIPMENT AND MATERIALS NECESSARY FOR RECEIVING, INSTALLING, TESTING AND ADJUSTING ANTENNA CABLES FROM THE ANTENNA TO THE CONNECTORS AT THE BASE TRANSMISSION SYSTEM (BTS). THIS SHALL INCLUDE ALL EQUIPMENT SHOWN OR REQUIRED FOR A COMPLETE OPERATING SYSTEM. ANTENNA, ANTENNA CABLES, CONNECTORS, AND FITTINGS SHALL BE THIRD PARTY FURNISHED COMPONENTS AS SHOWN ON THE BILL OF MATERIALS.
2. MATERIALS
- A. ANTENNA CABLES: AS SCHEDULED
  - B. ANTENNA CONNECTORS: AS SCHEDULED
  - C. CABLE HANGERS: INSTALLED AT MAXIMUM 4' SPACING
  - D. GROUNDING KITS: AS SPECIFIED
3. INSTALLATION
- A. ANTENNA CABLE LENGTHS SHALL BE FIELD MEASURED PRIOR TO PURCHASE OF CABLE. INSTALLER SHALL NOTIFY VZW OF THE OVERALL LENGTH REQUIRED.
  - B. CABLES SHALL BE LABELED IN ACCORDANCE WITH VZW SPECIFICATIONS.
  - C. ALL OUTSIDE CABLE CONNECTIONS SHALL BE COVERED WITH WEATHERPROOFING TAPE.
  - D. THE MINIMUM BENDING RADIUS FOR ALL ANTENNA CABLES SHALL BE AS SHOWN BELOW OR AS PER THE MANUFACTURER, WHICHEVER IS MORE CONSERVATIVE:
- | CABLE  | IN AIR / CABLE TRAY | IN CONDUIT |
|--------|---------------------|------------|
| 1/2"   | 5"                  | 10"        |
| 7/8"   | 10"                 | 18"        |
| 1 5/8" | 20"                 | 28"        |
- E. CABLES SHALL BE INSTALLED WITH THE MINIMUM NUMBER OF BENDS. CABLES SHALL NOT BE LEFT UNTERMINATED IN THE FIELD.
  - F. GROUNDING KITS - AFTER INSTALLATION OF GROUND STRAPS, THE CONNECTION SHALL BE MADE WEATHER TIGHT USING WEATHERPROOFING KITS AS IDENTIFIED ABOVE. GROUND PIGTAILS SHALL BE BROUGHT OUT IN THE DOWNWARD DIRECTION FROM THE CONNECTIONS TO THE ANTENNA CABLE WITHOUT ANY SHARP BENDS (MINIMUM BEND RADIUS 10") AND CONNECTION SHALL BE MADE TO GROUNDING SYSTEM.

3 ANTENNA NOTES AND REQUIREMENTS

INSTALL (3)  
1 5/8" COAX

X SECTOR =  
320° AZIMUTH

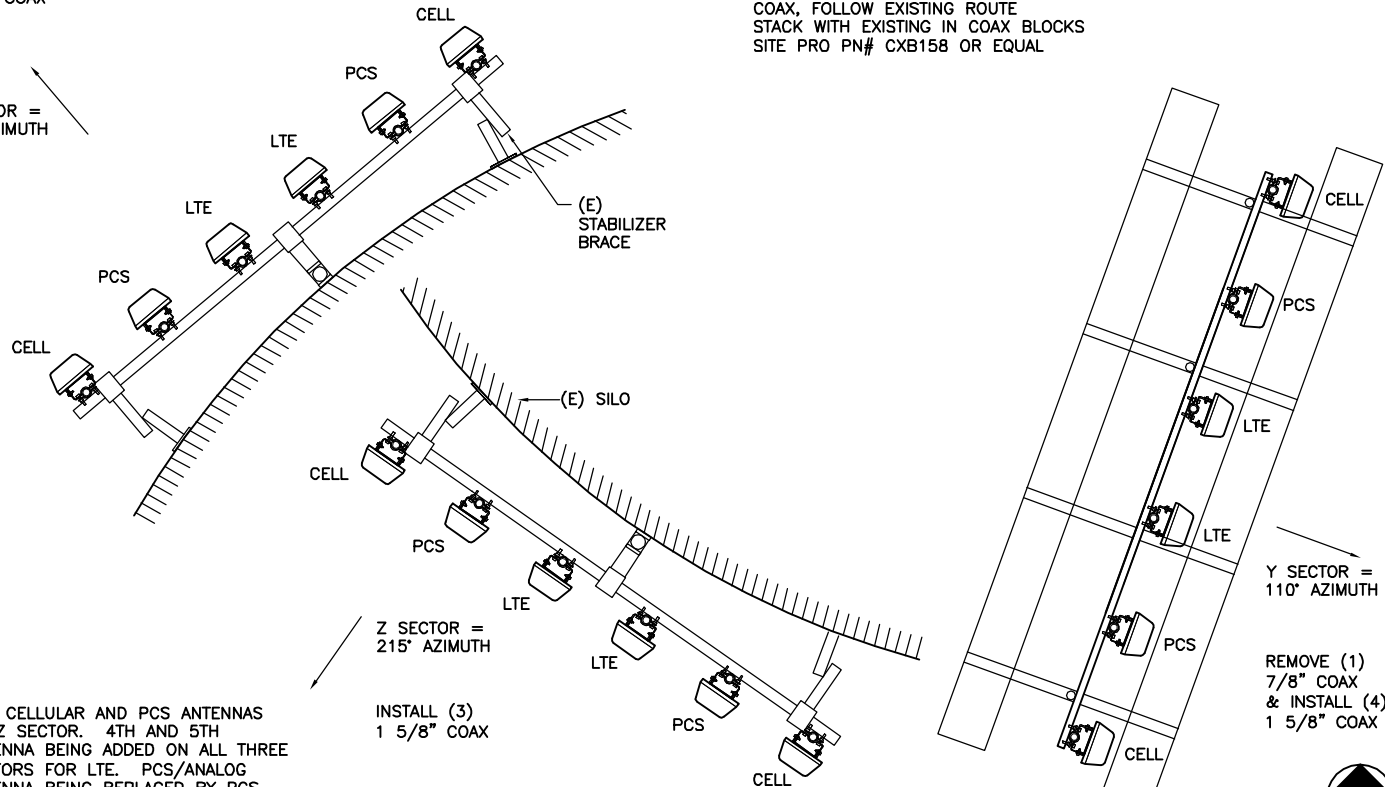

NEW CELLULAR AND PCS ANTENNAS ON Z SECTOR. 4TH AND 5TH ANTENNA BEING ADDED ON ALL THREE SECTORS FOR LTE. PCS/ANALOG ANTENNA BEING REPLACED BY PCS ANTENNA ON X AND Y. SPACE ALL ANTENNAS EQUALLY.

INSTALL (3)  
1 5/8" COAX

NOTE:  
REMOVE (1) 7/8" COAX TO 'Y' SECTOR AND ADD (10) NEW 1 5/8" COAX, FOLLOW EXISTING ROUTE STACK WITH EXISTING IN COAX BLOCKS SITE PRO PN# CXB158 OR EQUAL

REMOVE (1)  
7/8" COAX  
& INSTALL (4)  
1 5/8" COAX

1 PROPOSED ANTENNA CONFIGURATION

SCALE:  
N.T.S.



VERIZON WIRELESS SERVICES  
3131 S. VAUGHN WAY, SUITE 550  
AURORA, CO 80014  
PHONE: 303.873.2800

PROJECT INFORMATION:

SITE NAME  
**DEN LYONS**  
SITE ID.  
**215**  
SOUTHDOWN CEMENT PLANT  
5134 UTE HIGHWAY  
LONGMONT, CO 80503

| REV: | DATE:    | DESCRIPTION:    | BY: |
|------|----------|-----------------|-----|
| A    | 08/08/11 | CD REVIEW       | SSB |
| B    | 09/19/11 | CLIENT COMMENTS | JTT |
|      |          |                 |     |
|      |          |                 |     |
PLANS PREPARED BY:

**CSAi**  
CHARLES STECKLY ARCHITECTURE, Inc.  
ARCHITECTURE - PLANNING - DESIGN  
5935 SOUTH ZANG STREET, SUITE 280  
LITTLETON, COLORADO 80127  
OFFICE: 303.932.9974  
FAX: 303.932.6561

LICENSURE NO:

DRAWN BY: CHK: APV:

JTT TN CS

CONSULTANT:


SHEET TITLE:

**ANTENNA PLAN  
& RF DATA**

SHEET NUMBER:

**A2.2**

M:\2011\Projects\Verizon Wireless\L\TEDEN Lyons\CD\A30.dwg  
PLOTTED Sep 19, 2011 AT 2:29pm

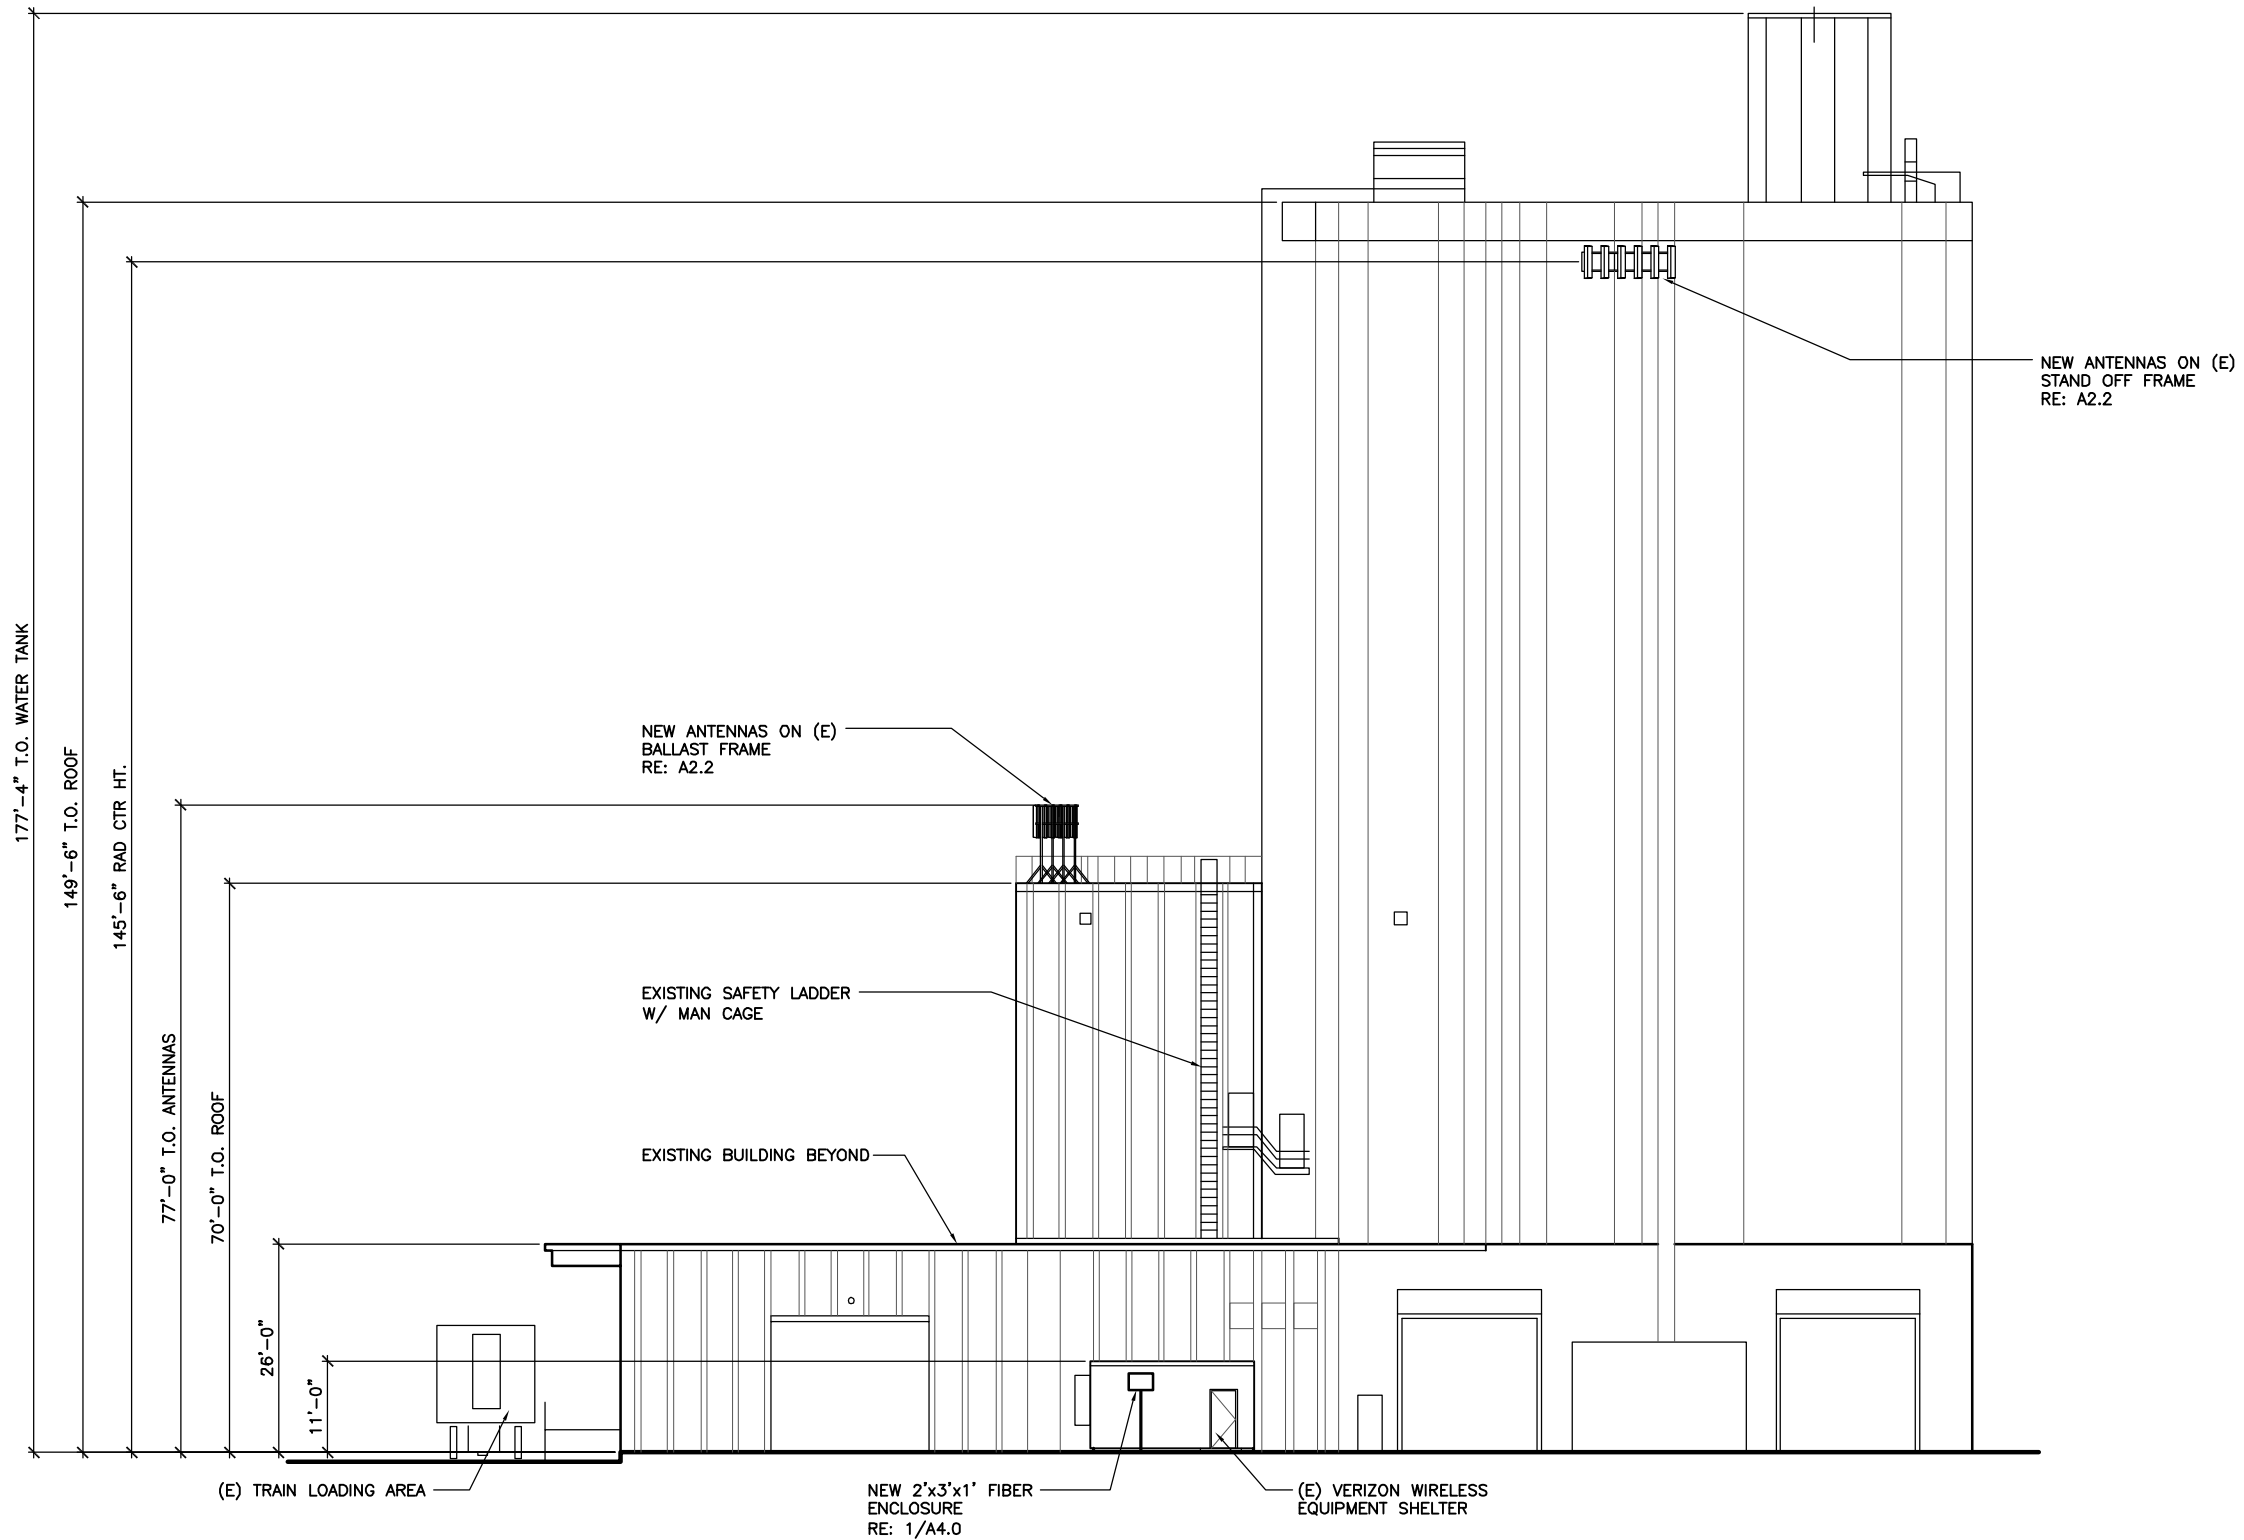

VERIZON WIRELESS SERVICES  
3131 S. VAUGHN WAY, SUITE 550  
AURORA, CO 80014  
PHONE: 303.873.2800

PROJECT INFORMATION:

SITE NAME  
**DEN LYONS**  
SITE I.D.  
**215**  
SOUTHDOWN CEMENT PLANT  
5134 UTE HIGHWAY  
LONGMONT, CO 80503

| REV: | DATE:    | DESCRIPTION:    | BY: |
|------|----------|-----------------|-----|
| A    | 08/08/11 | CD REVIEW       | SSB |
| B    | 09/19/11 | CLIENT COMMENTS | JTT |
|      |          |                 |     |
|      |          |                 |     |
PLANS PREPARED BY:

**CSAi**  
CHARLES STECKLY ARCHITECTURE, Inc.  
ARCHITECTURE – PLANNING – DESIGN  
5935 SOUTH ZANG STREET, SUITE 280  
LITTLETON, COLORADO 80127  
OFFICE: 303.932.9974  
FAX: 303.932.6561

LICENSURE NO:

DRAWN BY:      CHK:      APV:

|     |    |    |
|-----|----|----|
| JTT | TN | CS |
|-----|----|----|

CONSULTANT:

SHEET TITLE:

ELEVATION

SHEET NUMBER:

A3.0

\\M2011\Projects\Verizon Wireless LTE\DEN Lyons\CD\A40.dwg  
PLOTTED Sep 19, 2011 AT 2:29pm

5 NOT USED

3 CONDUIT DETAIL

SCALE:  
N.T.S.

2 TRENCH DETAIL


SCALE:  
N.T.S.

6 NOT USED


4 NOT USED

1 SECTION AT FIBER ENCLOSURE


SCALE:  
N.T.S.

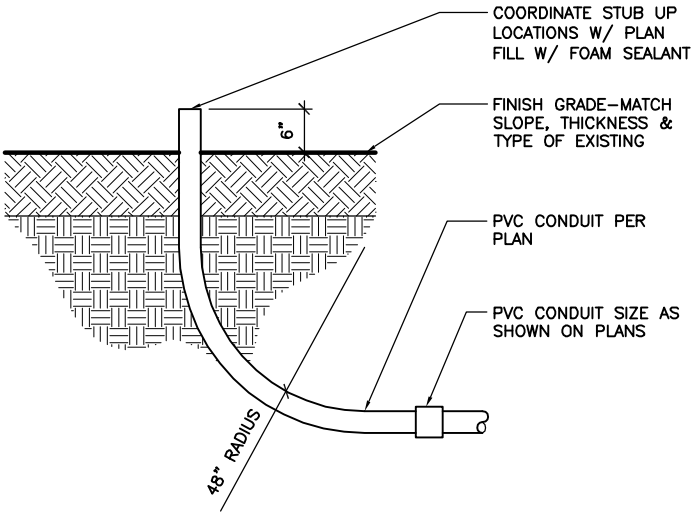

NOTE:  
INSTALL 200# TENSILE PULL WIRE (TRUE-TAPE)  
CALIBRATED IN FEET INSIDE EMPTY CONDUITS & TIE OFF  
AT EACH END.

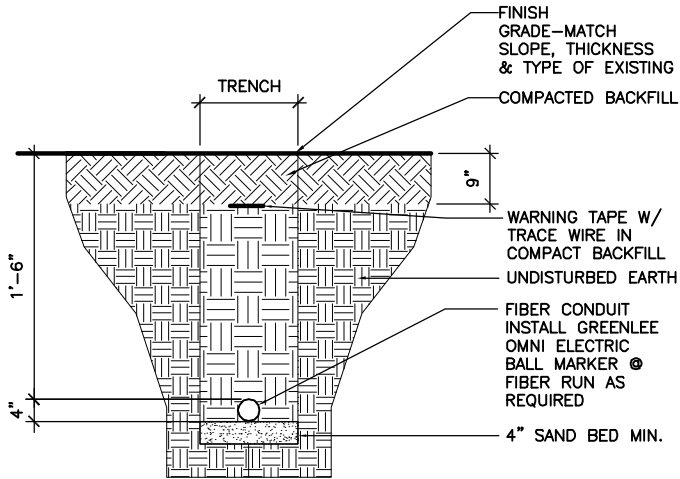

NOTES:  
1. INSTALL ALL UNDERGROUND UTILITIES PER LOCAL UTILITY REQUIREMENTS.  
2. LOCATE ALL UNDERGROUND UTILITIES PRIOR TO TRENCHING / EXCAVATION.  
3. COORDINATE SIZE AND TYPE WITH LOCAL UTILITY COMPANIES REQUIREMENTS.  
4. REFER TO ELECT PLAN FOR EXACT SIZE AND LOCATION.  
5. COMPACT BACKFILL TO 95% PROCTOR DENSITY AT ALL DRIVEWAY OR HARD SURFACED AREAS. COMPACT TO 90% PROCTOR DENSITY ALL OTHER AREAS UNLESS NOTED OTHERWISE, REFER TO GEOTECHNICAL REPORT.  
6. BACKFILL AND SAND BED NOT REQ'D WHEN BORING.

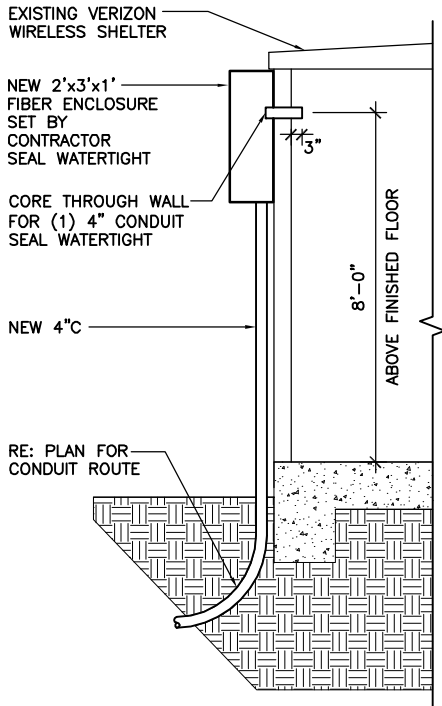

**verizon** wireless

VERIZON WIRELESS SERVICES  
3131 S. VAUGHN WAY, SUITE 550  
AURORA, CO 80014  
PHONE: 303.873.2800

PROJECT INFORMATION:

SITE NAME  
**DEN LYONS**  
SITE ID.  
**215**  
SOUTHDOWN CEMENT PLANT  
5134 UTE HIGHWAY  
LONGMONT, CO 80503

REV: DATE: DESCRIPTION: BY:

|   |          |                 |     |
|---|----------|-----------------|-----|
| A | 08/08/11 | CD REVIEW       | SSB |
| B | 09/19/11 | CLIENT COMMENTS | JTT |
|   |          |                 |     |
|   |          |                 |     |
PLANS PREPARED BY:

**CSAi**  
CHARLES STECKLY ARCHITECTURE, Inc.  
ARCHITECTURE - PLANNING - DESIGN  
5935 SOUTH ZANG STREET, SUITE 280  
LITTLETON, COLORADO 80127  
OFFICE: 303.932.9974  
FAX: 303.932.6561

LICENSURE NO:

DRAWN BY: CHK: APV:

|     |    |    |
|-----|----|----|
| JTT | TN | CS |
|-----|----|----|

CONSULTANT:


SHEET TITLE:

DETAILS

SHEET NUMBER:

A4.0

# Verizon Wireless Telecommunications Facility at Cemex Plant in Lyons

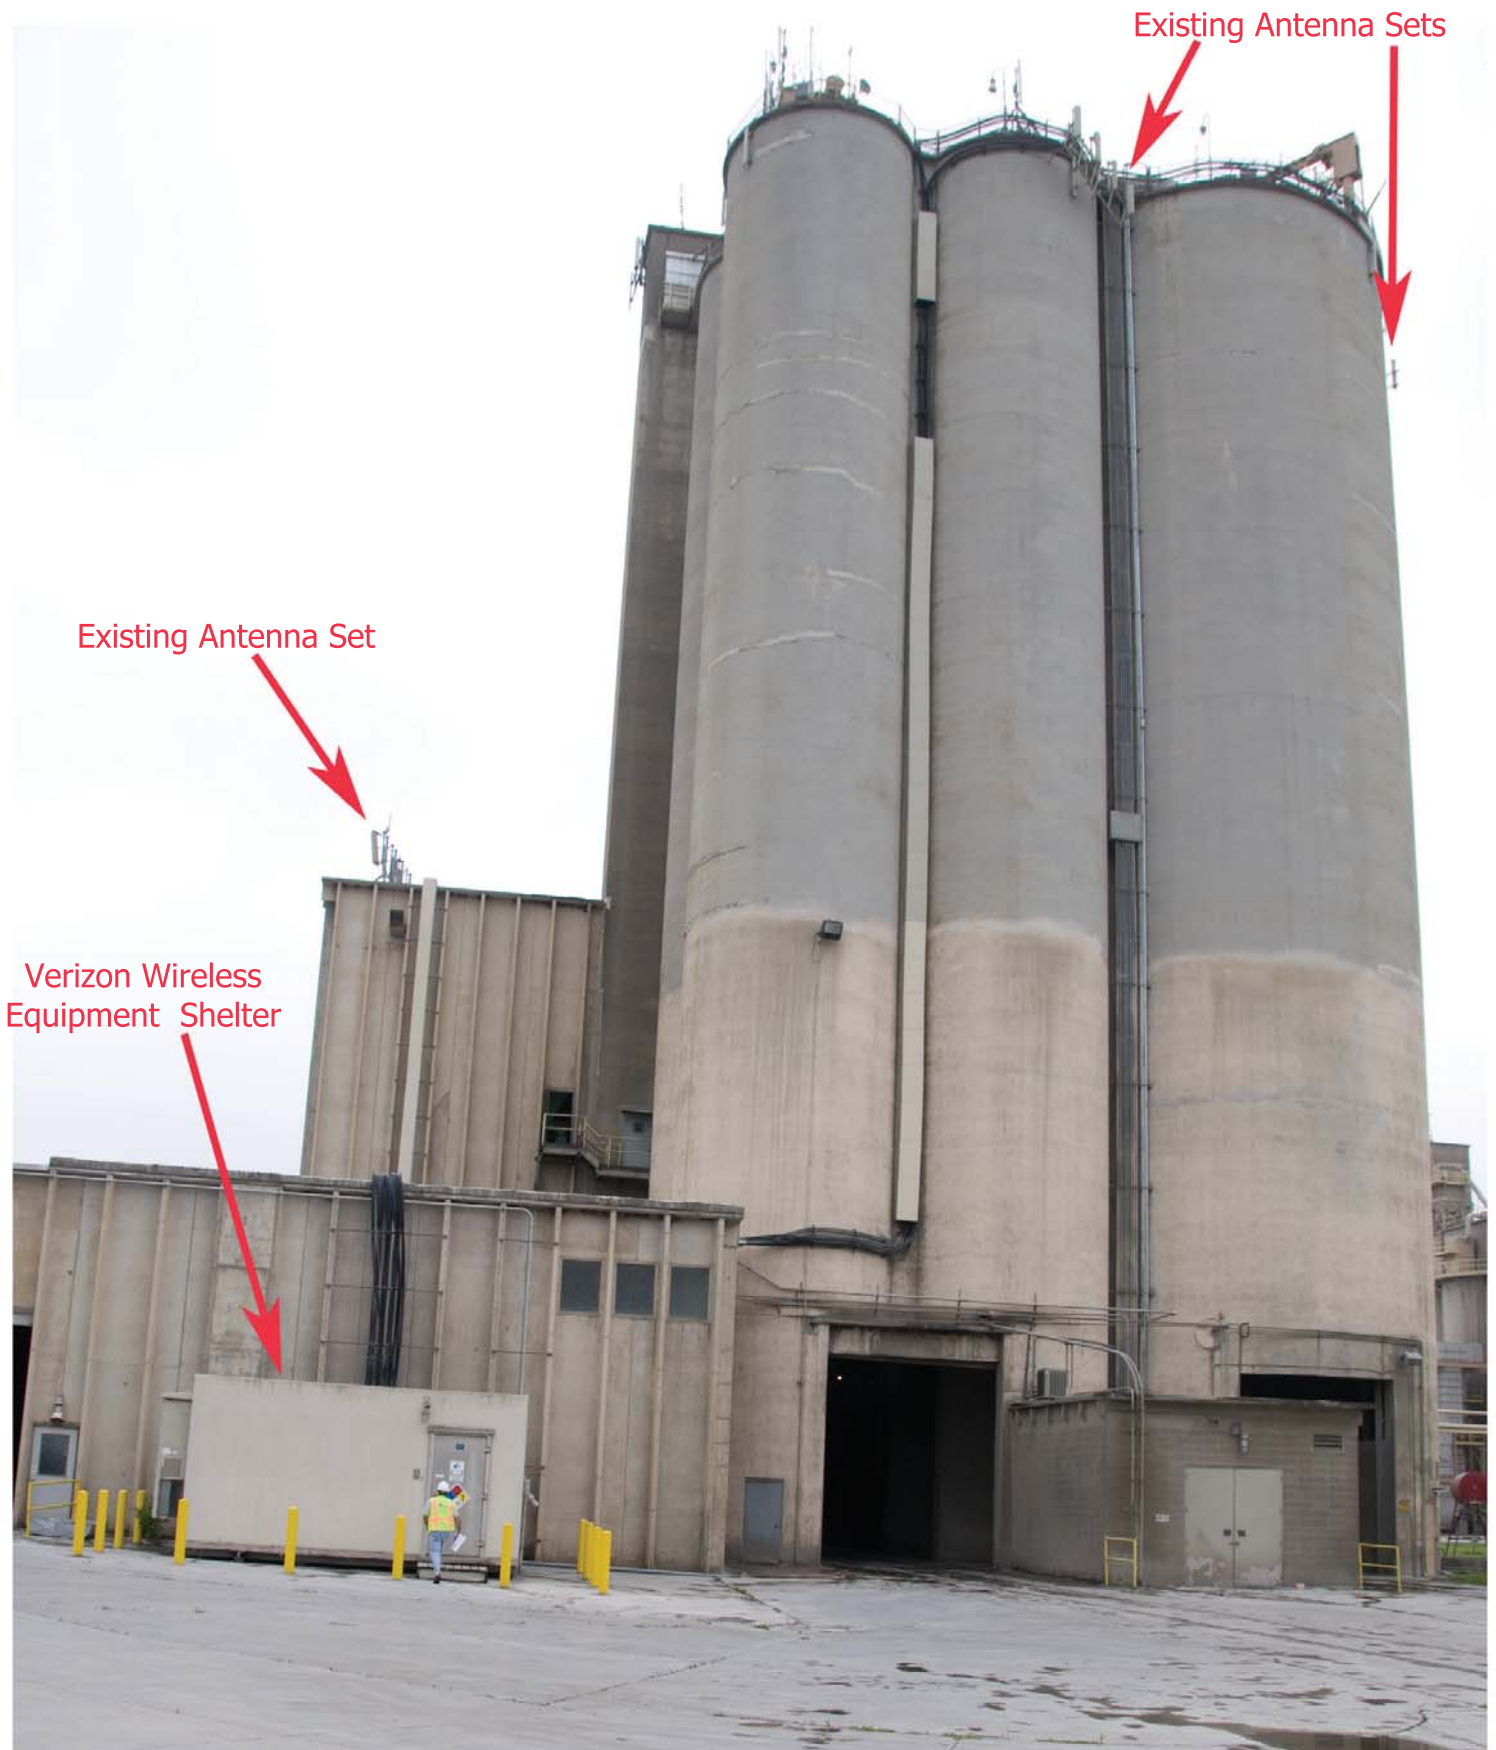

Three existing sets of 4 antennas on the silos. Verizon Wireless would like to add 2 additional antennas to each set of 4