

DATE RECEIVED (OFFICE USE ONLY)

JUN 02 2008

BOULDER COUNTY
BUILDING DIV.

BUILDING PERMIT APPLICATION

Land Use Department - BUILDING SAFETY & INSPECTION SERVICES DIVISION

2045 13th Street / 13th & Spruce Streets / Courthouse Annex

Mailing address: PO Box 471; Boulder, CO 80306.

Phone 303-441-3925 / http://www.co.boulder.co.us/lu

PROJECT LOCATION

BUILDING

BP-08- 871

PROJECT STREET ADDRESS

5134 Ute Highway

CITY/ZIP CODE

LYONS / 80540

LOT

BLOCK

SUBDIVISION

SECTION

TOWNSHIP

RANGE

☐ CONTACT

OWNERSHIP

OWNER'S NAME

Gumax

DAYTIME NUMBER

303 823 2111

ADDRESS

P.O. Box 529

EVENING NUMBER

CITY

LYONS

STATE

CO

80540

FAX NUMBER

303 823-2199

EMAIL ADDRESS

☐ CONTACT

CONTRACTOR

CONTRACTOR'S NAME

Gumax

DAYTIME NUMBER

ADDRESS

EVENING NUMBER

CITY

STATE

ZIP

FAX NUMBER

EMAIL ADDRESS

DESCRIBE THE PROJECT

Install dust collector on existing garment unloading system.

VALUATION

\$ 15,000

PROJECT INCLUDES: ☐ PLUMBING☐ ELECTRICAL☐ MECHANICAL

TYPE OF PROJECT (CHECK ONE)

- (01) ☐ New Structure
 (02) ☒ Addition To: *garment unloading*
 (03) ☐ Remodel
 (04) ☐ Electrical
 (07) ☐ Deconstruction of Structure
 (08) ☐ Change of Use
 (09) ☐ Moved-in Structure

TYPE OF STRUCTURE (CHECK ONE)

- (01) ☐ One Family Dwelling
 (02) ☐ Two Family or Attached Dwelling (including Townhouse)
 (03) ☐ Three and Four Family Dwelling
 (04) ☐ Hotel or Motel
 (06) ☐ Amusement & Recreation Building
 (07) ☐ Church & Other Religious Building
 (08) ☐ Industrial Building, Manufacturing Plant, Factory
 (09) ☐ Service Station & Repair Garage
 (10) ☐ Detached Garage
 (12) ☐ Office, Bank, and Professional Building
 (13) ☐ School
 (14) ☐ Store, Customer Service
 (15) ☐ Barn, Storage Shed, Outbuilding
 (16) ☐ Mobile/Manufactured Home
 (22) ☐ Public Works, Utility Building
 (23) ☐ Pool, Hot Tub, Fence, Retaining Wall, Pump (Non-structure)
☐ Other: *Dust Collector Support*

	EXISTING BUILDING	NEW CONSTRUCTION	EXISTING & NEW TOTAL
Height of Structure measured from existing grade	FT. <i>20'-3"</i>	FT. <i>20'-3"</i>	FT. <i>20'-3"</i>
# of Bedrooms			
# of Bathrooms			
Property Size:			

SETBACKS (Distance of Project to Property Lines)

FRONT SETBACK EXISTING	SIDE SETBACK EXISTING	SIDE SETBACK EXISTING	REAR SETBACK EXISTING
FT.	FT.	FT.	FT.
FRONT SETBACK PROPOSED	SIDE SETBACK PROPOSED	SIDE SETBACK PROPOSED	REAR SETBACK PROPOSED
FT.	FT.	FT.	FT.

PROPOSED NEW BUILDING OR ADDITION		
STRUCTURE SIZE	FINISHED	UNFINISHED
Basement	SQ. FT.	SQ. FT.
1st Floor	SQ. FT.	SQ. FT.
2nd Floor	SQ. FT.	SQ. FT.
3rd Floor	SQ. FT.	SQ. FT.
All other Floors	SQ. FT.	SQ. FT.
Garage	SQ. FT.	SQ. FT.
Deck	SQ. FT.	Covered Porch
	SQ. FT.	SQ. FT.

WATER SERVICE (✓ one) ☐ Individual Well ☐ Community Well ☐ N/A ☐ Public: _____	SEWER SERVICE (✓ one) ☐ Septic Tank ☐ Vault ☐ N/A ☐ Public: _____	ELECTRICAL SERVICE (✓ one) ☐ Xcel Energy ☐ United Power ☐ Egas Park ☒ Poudre Valley Rea ☐ Longmont ☐ N/A	GAS SERVICE (✓ one) ☐ Xcel Energy ☐ Propane ☐ N/A ☐ Other: _____	ACCESS (✓ one) ☐ Existing Driveway ☐ New Driveway ☐ N/A ☐ Other: _____
---	--	--	---	---

CERTIFICATION

I certify that the above information is correct and agree to construct this building in accordance with the plot, building plans and specifications submitted herewith, and in strict compliance with all the provisions of the Zoning Ordinance, Building Code, Electrical Code, and Health and Plumbing Regulations of the County of Boulder.

APPLICANT (PLEASE PRINT)

Randy Wiley

DATE

5-15-08

TITLE

Project Mgr.

APPLICANT SIGNATURE

Randy Wiley

Revised: 11/30/05

g:\handouts\building\current\bldg_app.pmd

120 m.p.h.

BP-08-871

This parcel at 005134 UTE HY
is owned by
CEMEX INC
ATTN TAX DEPT
PO BOX 1500
HOUSTON, TX 77251

Its Legal Description is
21-3N-70, 28-3N-70, 29-3N-70 SE 1/4
SE 1/4 20-3N-70 & PT W 1/2 27-3N-70
& E 500 FT OF LESS .19 ACS M/L TO
BOCO & LESS PTS TO US LESS PT TO
HWY DEPT TOTAL 757.85 ACS SPLITS
128969 & 142930 TO HWY DEPT
PROPERTY ADDRESS: 005134 UTE HY
LONGMONT□

Its GIS Land Area is 37738557 square feet, 866.358 acres.

It is Parcel Number 120328000001 and this owner has Account Number R0053049.

These owners are taxed in the following:
BOULDER COUNTY GENERAL OPERATING
ST VRAIN REIJ GENERAL OPERATING
NORTHERN COLO WATER CONTRACT OBLIG
ST VRAIN LEFT HAND WATER GENERAL OPER
HYGIENE FIRE DIST GENERAL OPERATING
LONGMONT CONSERVATION DIST GEN OPER
RTD GENERAL OPERATING

Recent deeds for this parcel:

SW at Reception Number 613148 from to for \$42000000 on 4/5/1984
QD at Reception Number 1284471 from to for \$0 on 4/21/1993
QD at Reception Number 1284471 from to for \$0 on 4/21/1993
SW at Reception Number 1432787 from to for \$818000 on 6/1/1994
SW at Reception Number 1432787 from to for \$818000 on 6/1/1994
SW at Reception Number 1477357 from to for \$0 on 11/7/1994
SW at Reception Number 1477357 from to for \$0 on 11/7/1994
SW at Reception Number 1756839 from to for \$0 on 12/19/1997

NOTE: Because of small inconsistencies in the locations of lines in the map layers, GIS searches may return data from adjacent polygons even though no overlap is visible on the screen. Display the layers in question to resolve any uncertainty.

PLSS Section, Township, Range on or adjacent to this Parcel:
T3NR70WS20
T3NR70WS21
T3NR70WS29
T3NR70WS28

T3NR70WS27

Zoning Districts on or adjacent to this Parcel:

GI

GI with Floodplain Overlay

A with Floodplain Overlay

A with Floodplain Overlay

A

A

Open Space ownerships on or adjacent to this Parcel:

CE BRALY SE SUB

COS WESTERN MOBILE

COS MONTGOMERY (DONALD)

COS WESTERN MOBILE

COS WESTERN MOBILE

COS WESTERN MOBILE

County Plats on or adjacent to this Parcel:

Permits for this Parcel:

BP-00-872 ELEC FOR WATER PUMP MAIN PLANT

BP-00-1207 CELLULAR ANTENNA SITES

BP-01-494 SIGN REPLACEMENT

BP-01-2179 INSTALL PCS EQUIP & ANTENNAS ON CEMENT PLANT - FINAL INSPECTION
COMPLETED ON 2/11/02 BY J.H.

BP-04-1389 TEMPORARY OFFICE TRAILER(APPLICATION EXPIRED-11/21/07)

BP-04-1670 STOREROOM MODIFICATIONS(APPLICATION EXPIRED-11/21/07)

BP-05-129 REPLACE EXISTING CONDITIONING TOWER

BP-06-692 INSTALL TWO 100GAL WATER HEATERS IN THE OFFICE BLDG

BP-07-598 INSTALL 3 GROUPS OF PANEL ANTENNAS

BP-07-762 RUNNING POWER TO PARTICULATE METER

BP-65-8040 EARTHWORK & FOUNDATIONS FOR CEMENT PLANT

BP-66-9358 NEW RES

BP-67-10137 SUPERSTRUCTURE FOR CEMENT PLANT

BP-70-13156 SIGN FOR CEMENT PLANT
BP-73-18153 COAL STORAGE SILO
BP-75-19820 SHOP
BP-78-22476 REPAIR OVERHEAD DOOR
BP-78-23408 ELEC FOR NEW PUMP
BP-79-324 ENLARGE STORAGE BLDG
BP-79-463 COMBUSTION CHANGE/KILN
BP-79-513 5 CONSTRUCTION MOHOS
BP-80-619 ELEC FOR MOBILE HOME
BP-81-71 elec for traffic light
BP-84-182 FOUNDATION FOR CLINKER COOLER
BP-90-230 REPAIR GAS LEAK/NEW WATERLINE
BP-94-2403 DEMO-DWELLING,BARN,GAR,SHED,SILO
BP-94-2566 OFFICE TRAILER
BP-97-1785 TELECOM SITE/WALL MOUNTED

Dockets for this Parcel:

AP-02-003 SIERRA CLUB Appeal
AP-03-003 CEMEX Appeal #1
AP-03-004 CEMEX Appeal #2
LS-94-0097
LS-96-0243
NWE-05-012 CEMEX INC.
PAC-03-032 CEMEX INC.
SE-96-18 WESTERN MOBILE BOULDER, INC.
SPR-97-160 SOUTHDOWN INC / US WEST NEWVECTOR G

SU-01-08 QWEST WIRELESS (Cemex Cement Plant)

SU-03-05 CEMEX (Lyons Cement Plant) SU/SSDP

SU-06-016 CINGULAR WIRELESS (Cemex Inc.) Tele

SU-88-21 LYONS RUBBER RECYCLING CENTER

SU-96-18 WESTERN MOBILE BOULDER, INC.

ZON-07-028 CEMEX INC — 3/30/07 resolved

Assessor land and structure listing for this parcel: XFOB = Extra Feature or Building

ACCOUNTNO	MODEL	OCCURANCE	ATRIBTYPE	ATRIBDESC
R0053049	COMML	1.0	ABSTRACT_CODE	MANUFACTURING/PROCESSING IMPRO
R0053049	COMML	1.0	CONST	TEES/TILT
R0053049	COMML	1.0	DEPR01	1969
R0053049	COMML	1.0	DESIGN	MASONRY
R0053049	COMML	1.0	HEIGHT	42 - HEIGHT
R0053049	COMML	1.0	QUALITY	AVERAGE
R0053049	COMML	1.0	STORIES	1 - STORIES
R0053049	COMML	1.0	YEAR	1960 - YEAR
R0053049	LAND COMML	1.0	ABSTRACT_CODE	REFINING/MILLING-LAND
R0053049	LAND COMML	100.0	ABSTRACT_CODE	MANUFCTNG/PROCESNG-LAND
R0053049	LAND COMML	101.0	ABSTRACT_CODE	REFINING/MILLING-LAND
R0053049	LAND MT	3.0	ABSTRACT_CODE	SINGLE FAM.RES.-LAND
R0053049	RESMT	3.0	ABSTRACT_CODE	SINGLE FAMILY RESIDENTIAL IMPR
R0053049	RESMT	3.0	BATH_F	1 - BATH FULL
R0053049	RESMT	3.0	BEDROOMS	BEDROOMS
R0053049	RESMT	3.0	CONST	FRAME
R0053049	RESMT	3.0	DEPR01	YEAR
R0053049	RESMT	3.0	DESIGN	1 STORY - RANCH
R0053049	RESMT	3.0	QUALITY	AVG PLUS
R0053049	RESMT	3.0	ROOMS	ROOMS
R0053049	RESMT	3.0	YEAR	1960 - YEAR
R0053049	XFOB	301.0	ABSTRACT_CODE	SINGLE FAM RES IMPROVEMENTS
R0053049	XFOB	301.0	DEPR01	YEAR
R0053049	XFOB	301.0	XFOB_CODE	BARN-D,LOW 15 YRS
R0053049	XFOB	301.0	YEAR	1960 - YEAR

Assessor land and structure areas or counts for this parcel: Correlate with land and structures by Model+Occurance for each Account.

ACCOUNTNO	MODEL	OCCURANCE	SUB_CODE	AREA_ACT
-----------	-------	-----------	----------	----------

R0053049	COMML	1.0	4940	181928.0
R0053049	LAND_COMML	1.0	SQFT	1829520.0
R0053049	LAND_COMML	100.0	SQFT	1873080.0
R0053049	LAND_COMML	101.0	ACRES	232.0
R0053049	LAND_MT	3.0	ACRES	440.85
R0053049	RESMT	3.0	AREA_FIRST	1508.0
R0053049	RESMT	3.0	B_SUB_UNF	1508.0
R0053049	RESMT	3.0	POR_PORCH	260.0
R0053049	XFOB	301.0	XFOB_UNITS	840.0



BUILDING PERMIT APPLICATION REVIEW FORM

FILE NUMBER

08-871


PROJECT LOCATION					
PROJECT ADDRESS			UNIT	CITY	ZIP CODE
5134 Ute Hwy					
LOT	BLOCK	SUBDIVISION NAME	SECTION	TOWNSHIP	RANGE
			28	3N	70W
OWNER'S NAME					
Cemex Inc					
OCCUPANCY GROUP		TYPE OF CONSTRUCTION		VALUATION	
				\$	

STRUCTURE DATA	EXISTING	TO BE CONSTRUCTED
Height of Structure	FT	20 FT
Number of Stories		
Number of Dwellings		
Number of Bedrooms		
Number of Bathrooms		

Water	
Electric	
Sewer	
Gas	
Access	

STRUCTURE SIZE (For new construction & additions only)	FINISHED	UNFINISHED
Basement	SQ. FT.	SQ. FT.
1st Floor		
2nd Floor		
All other Floors		
Deck		
Covered Roof		
Garage		
Totals		
Snowload		
Windload		

Tax I.D.#	53049
Parcel #	
Deed #	
Tax Area	
Service Area	
School District	3V
Fire District	HY
Property Size	8.66 ACRE(S)
Zoning (1)	GI ACRE(S)
Zoning (2)	FD ACRE(S)

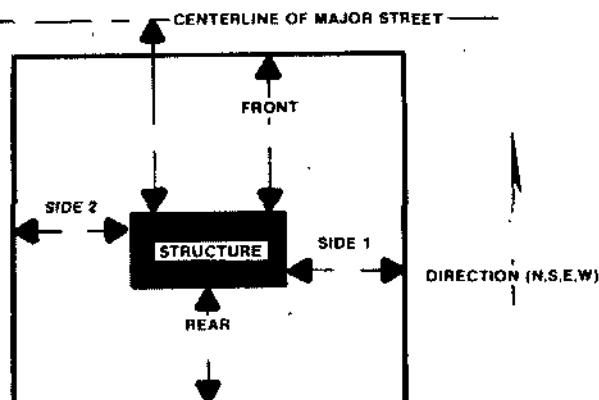

Building Permit Routing Form

BP-08- 871

Owner Name Cemey

Permit Tech KA
Plan's Exam LP
CSFS Y/N

Project Description Install dust collector on unloading system

Fees:

Application Deposit \$ 25.00 PA check

Subtotal \$ 493.70

Building Division Fees \$ 463.70

Less deposit \$ 25.00

Investigation Fee \$ _____

Access Fee \$ _____

BALANCE DUE: \$ 468.70

Escrow \$ _____

Floodplain Fee \$ _____

Permit Tech comments:

Zoning Approval

SPR reqd _____ zoning affidavit _____ height survey reqd _____ setback survey reqd _____
Comments:

approved by/date

Historic Approval

Comments:

not a sub. modification
approved by/date

Site Plan Review

Site Plan Review # _____ notified owner/date: _____ notified contractor/date: _____

Comments:

approved by/date

Wildfire

Comments:

approved by/date

Transportation Approval

access permit # _____ road maint. waiver reqd _____ inspection reqd prior to CO _____

Comments:

approved by/date

Floodplain

floodplain permit # _____

Comments:

approved by/date

Plan Check

Soils Report Info: Caiss _____ Spd Ftgs _____ Per.Drain _____ Voids _____ Float.Slabs _____
Fire Dept _____ Health Dept - Comm. Kitchen _____

Comments:

MBH
6.10.08
approved by/date

Chief Building Official

Comments:

6/10/08
approved by/date

WFM

SPR

zoning

transportation

well/water

septic/sanitation

access permit

road maint waiver

notification:

called (whom?) Randy
ivm 6/11/08

sent card

mailed permit



BP-08-871

SMH ENGINEERING, INC.
3609 S. WADSWORTH BLVD. STE 320
LAKEWOOD, CO 80235
[303] 989-2110
[303] 989-8058 fax

May 30, 2008

Mr. Randy Wiley
Cemex Lyons Plant
PO Box 529
Lyons, CO 80540

RECEIVED
JUN 02 2008

BOULDER COUNTY
BUILDING DIV.

Re: Design Review of Existing Support Structure
SMH No. 6008.0528

Dear Mr. Wiley:

On Wednesday, May 28, 2008, Devlynn Rodriguez and I visited the Lyons Plant to obtain data for an existing dust collector support structure. This dust collector vents the rail unloading screw conveyor and FK pump located at the southeast corner of the cement shipping silos and pack house structure. We measured all steel members of the support structure. Attached are drawings S-1 and S-2 recording our measurements. Gernot Appelt is the Senior Structural Engineer for SMH Engineering. Attached is a copy of his calculations based on the data provided on the drawings. Please note the calculations include the 120 MPH wind speed as required for your plant location.

The calculations verify that the structure is adequately designed. The drawings and calculations have been stamped and signed for your records.

Thank you for the opportunity to work for Cemex again. If there are questions, please let us know.

Regards,
SMH ENGINEERING, INC.

Ric Laman, P.E.
President



Post Office Box 471 ° Boulder, Colorado 80306

Land Use Department

Courthouse Annex

2045 13th Street ° 13th & Spruce Streets ° Boulder, Colorado 80302 ° (303) 441-3930

File Number: **BP-8-871**

Date: **June 16, 2008**

Owner Name: **,**

Project Address: **5134 UTE HW**

Project Description: **INSTALL DUST COLLECTOR ON UNLOADING SYSTEM**

APPROVED PLANS AND REVIEW LIST

I agree to read the Boulder County Building Division plan review list that was prepared for my building project and attached to the approved building plans. I understand that my building project must comply with all applicable code requirements.

I also understand that this plan review list and the approved plans must be kept on the job site, and must be available to the inspector when inspections are made.

I further understand that not having the approved plans and review list on site may result in no inspection being made and a reinspection fee being charged.

Owner / Agent



BUILDING PERMIT

Land Use Department • Building Safety & Inspection Division
Courthouse Annex • 2045 13th St • 13th & Spruce Streets
P.O. Box 471 • Boulder, Colorado 80306-0471

(303) 441-3925 Fax 303.441.4856

Permit Number
BP - 08 - 871

File Copy

PROJECT LOCATION

Project Address	Unit Number	City	Zip Code
5134 UTE HW		LY	80540
Lot	Block	Subdivision Name	Section Township Range
		UNPLATTED	28 3N 70

WORK DESCRIPTION

Description of Work
INSTALL DUST COLLECTOR ON UNLOADING SYSTEM

OWNER

Owner Name & Address
CEMEX INC
5134 UTE HW

City State Zip Code
LONGMONT CO 80503

Day / Primary Phone Night / Secondary Phone
(303) -823-2111

CONTRACTOR / AGENT

Contractor Name & Address
CEMEX INC
5134 UTE HW

City State Zip Code
LONGMONT CO 80503

Day / Primary Phone Night / Secondary Phone
(303) -823-2111

STRUCTURE DATA

Activity Code	Description Code		
2 Addition to structures.	8 Industrial buildings, manufacturing plants, factories		
Occupancy Group	Construction Type	Stories	Structure Height (FT)
U	VB	0	20
Snow Load (PSF)	Wind Speed (MPH)	New Bedrooms	New Bathrooms
		0	0

SETBACKS / ZONING / FEES

Setback #1 (FT)	Setback #2 (FT)	Setback #3 (FT)	Setback #4 (FT)	Property Size (Acres)
				866
Zoning District(s)	Parcel ID Number			
GI/FO/A	120328000001			
Tax ID Number	Deed Number	Access Permit Number		
53049	1756839			

New Construction Square Footage

	Finished	Unfinished
Basement:	0	0
1st Story:	0	0
2nd Story:	0	0
3rd Story:	0	0
All Other Stories:	0	0

Decks	Covered Area	Greenhouse	Garage
-------	--------------	------------	--------

Fee Summary

Project Valuation:	15,000
Building Permit Fee:	269.95
Plan Check Fee:	175.00
Access Fee:	.00
Taxes:	48.75
Receipt Number	Total Fees:
56260	493.70

Utilities & Services

Water Provider	Sanitation Provider
Not Known	Not Known
Electric Provider	Gas Provider
Poudre Valley REA	Not Known
Fire District	
Hygiene	

Approved By Chief Building Official

Jeff Dwight

Date Of Issue

June 16, 2008

The approval of plans and specifications does not permit the violation of any section of the Boulder County Building Code, Land Use Code, or any other Ordinance or State Law.

* FIELD INSPECT TO CODE *

Permit shall become null and void if construction is not commenced within 180 days of issuance, or if work is suspended or abandoned for a period of 180 days after the work is commenced.



REQUIREMENTS & REMARKS

Land Use Department • Building Safety & Inspection Division
Courthouse Annex • 2045 13th St • 13th & Spruce Streets
P.O. Box 471 • Boulder, Colorado 80306-0471

(303) 441-3925 Fax 303.441.4856

Permit Number

BP - 08 - 871

Building Code

• Land Use Dept / Building Division / 303 - 441 - 3925

Comments

All work per the applicable provisions of the Boulder County Building Code to include: the 2006 IBC, 2006 IMC, 2006 IPC, 2006 IFGC, 2006 IECC, 2005 NEC, and the Boulder County Amendments.

New or replacement exterior lighting fixtures must be down-lit shielded fixtures in conformance with Article 7-1600 of the Boulder County Land Use Code.

Inspector Copy

5134 UTE HW.

5134 UTE HW.



BUILDING INSPECTION RECORD

Land Use Department • Building Safety & Inspection Division
Courthouse Annex • 2045 13th St • 13th & Spruce Streets
P.O. Box 471 • Boulder, Colorado 80306-0471

(303) 441-3925 Fax 303.441.4856

Permit Number

BP - 08 - 871

Site Address

5134 UTE HW

Inspector must date and initial each inspection pertaining to this job.

DO NOT POUR CONCRETE OR COVER ANY WORK UNTIL APPROVED BY INSPECTOR

FINAL BUILDING INSPECTIONS

INSPECTION	DATE APPROVED	INSPECTOR	COMMENTS	INSPECTOR	DATE
GRADING & DRAINAGE					
FINAL FRAMING					
ELECTRICAL FIXTURES	08/13/08	<i>[initials]</i>	COAR	<i>[initials]</i>	06/25/08
PLUMBING FIXTURES					
FINAL HEATING & VENTILATION					
Other:					
Other:					
Other:					
BUILDING INSPECTIONS COMPLETED	08/13/08	<i>[initials]</i>			
ALL REQUIREMENTS COMPLETED					

Use or occupancy is not permitted until all building inspections have been completed and approved and all other required inspections and approvals have been obtained. See also the "Requirements & Remarks" page, printed on the opposite side of the "Building Permit" page, for details on what other requirements may exist.

METER RELEASES


INSPECTION	DATE APPROVED	INSPECTOR	AGENCY	CONTACT	RELEASE DATE	BY
TEMPORARY CONSTRUCTION ELECTRIC METER RELEASE						
FINAL ELECTRIC METER RELEASE						
FINAL GAS METER RELEASE						

Building division staff typically informs utility companies of released meters on the business day following the meter release inspection.

All requests for inspection(s) must be received prior to 3:30 p.m., business days, in order to be scheduled for the following business day. Monday inspections must be scheduled by 3:30 p.m. Friday. Please provide the following information: PERMIT NUMBER, PROJECT ADDRESS, OWNER'S NAME, TYPE OF INSPECTION and DATE OF INSPECTION... CALL: (303) 441-3925, press 1, then 2 to schedule an inspection.

**POOR QUALITY
COPY**

**PAGE(S) POSSIBLY
ILLEGIBLE AFTER
SCANNING**

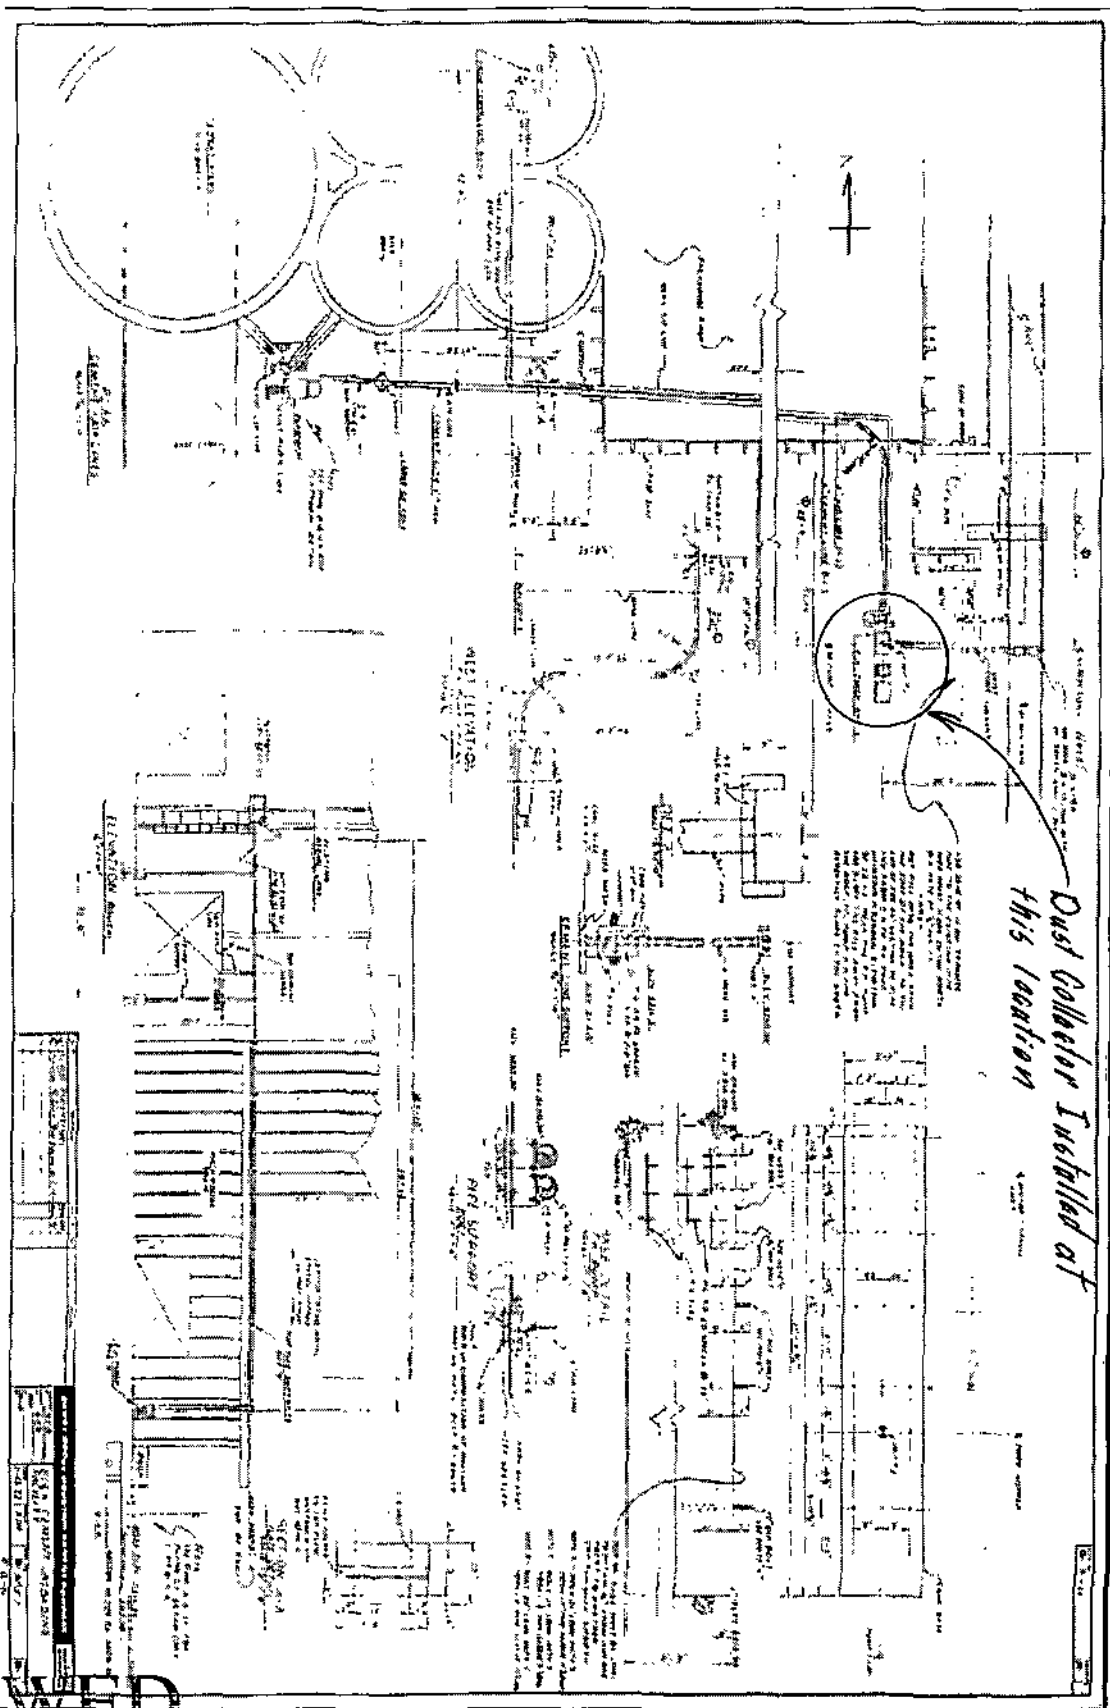


1-13-72

REVIEWED

JUN 10 2008

BOULDER COUNTY
BUILDING DIVISION

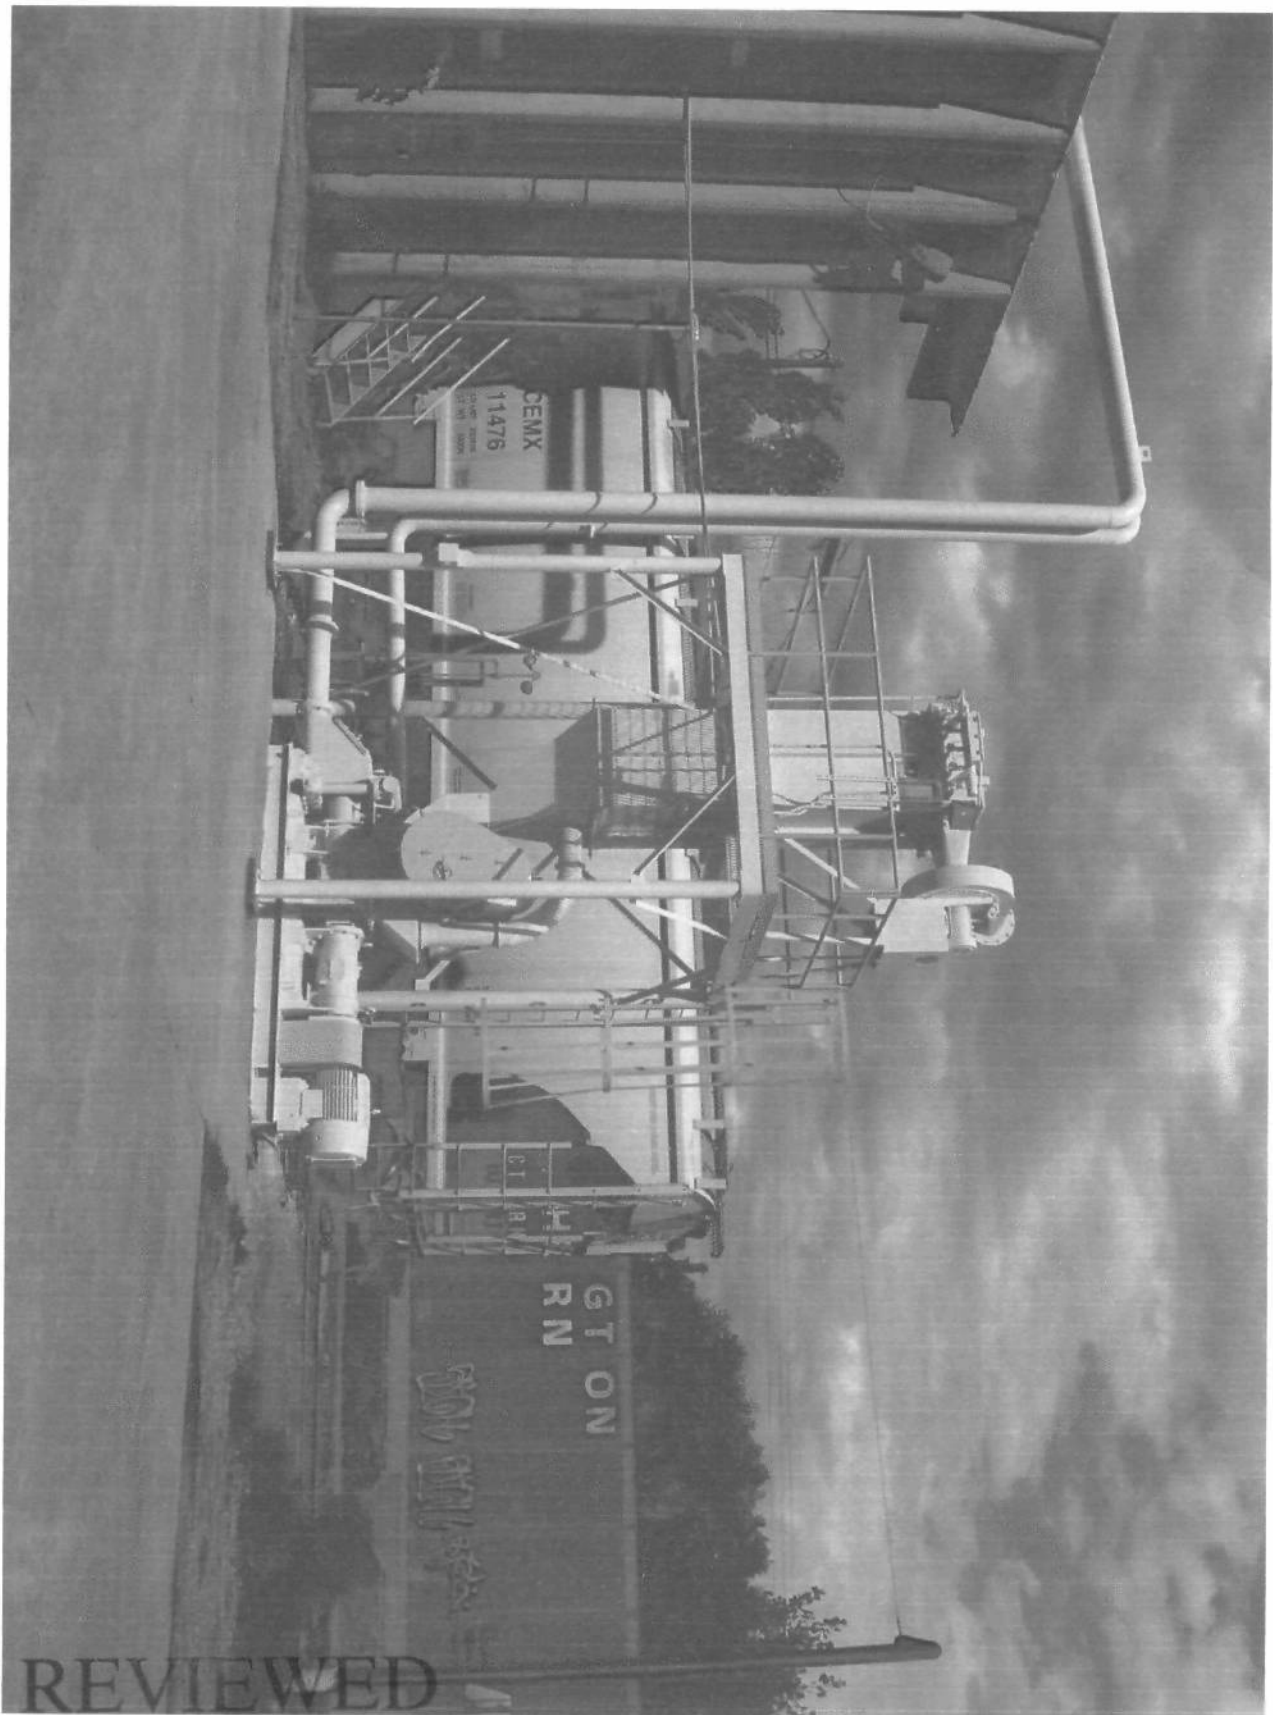


JUN 10 2008

BOULDER COUNTY
BUILDING DIVISION

Platform
10' x 8'-8"
Dust Collector
W = 3'
D = 3'
H = 11'-2"
Overall Height
20' 3"



SMH JOB NO. 6008-0528 DATE 5-29-02 BY G.D.A. CHECKED BY
CLIENT CEMEX - LYONS PLANT PROJECT DUST COLLECTOR SUPPORT
SUBJECT

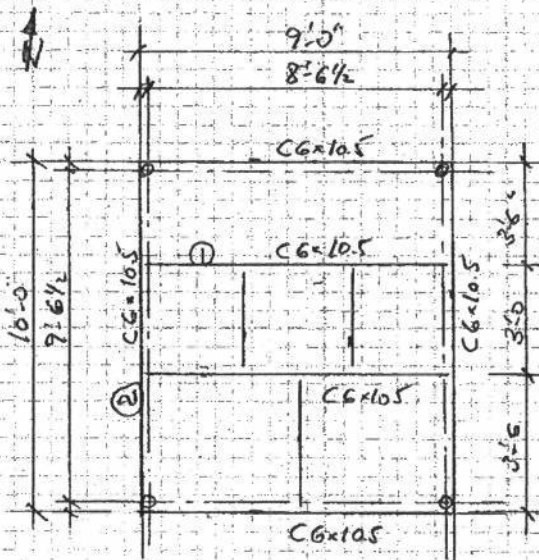

CODE: IBC 2003 (ASCE 7-02)

LOADING

DUST COLLECTION (MIXED-PUR 25 STRS) = 1.6
CEMENT IN HOPPER $3.0' \times 3.0' \times 1/2' \times 0.15 = 1.4$ 3.0

PLATFORM DL $9.0' \times 10.0' \times 0.02 = 1.8$
LL $9.0' \times 10.0' \times 0.06 = 5.4 - 0.2 = 7.0$ 10.0 K

LOAD PER COL = $10.0' \div 4 = 2.5$ K

WIND BASIC SPEED $V = 120$ MPH

$K_z K_{zt} = 1.0 / K_d = 0.85, I = 1.0$

$Q_s = 0.00256 K_z K_{zt} K_d V^2$
 $= 0.00256 \times 1.0 \times 0.85 \times 120^2 = 1.0$ 32 psf

GROSS AREA $9.0' \times 13.0' + 3.0' \times 5.8' = 135$ sq

$W = 135 \times 0.032 = 4.3$ K + 2.2' / RENT

$M_w = 2.2 \times 8.0 = 17.6$ 17 K

$C-T = 17.6 + 9.0 = 2.0$ K

COLUMN $M_w = 1.1 \times 12.0 = 13.2$ K

REDUCTION FOR WIND $13.2 \times 0.75 = 9.9$ K

$F_{RED} = 9.9 \times 0.5 = 5.0$

USE 5" STD PIPE ($5.5 \times 5.5 > 5.0$)

A. BOLTS UPLIFT = 2.3 K

USE 4-1/2" ϕ 5" EMBED ($4 \times 4.0 = 16$ K)

KNEE BRACE

$L = 2 \times 1/4, A = 0.94, r = 0.39, l = 5.0', K = 1.0$

$Kr/r = 133, F_a = 8.4$ ksi

$P_{nu} = 0.94 \times 8.4 = 7.9$ K > 2.6 K

BEAM ① DUST COLL $P = 3.0 \times 2 = 1.5$ K

PLATE $W = 0.08 \times 3.3 = 0.3$ K


$M = (1.5 \times 9.0 \div 4) + (0.3 \times 9.0^2 \div 2) = 2.4 + 13.0 = 6.4$ K

$F_{RED} = 6.4 \times 0.5 = 3.2$

USE C6x10.5

BEAM ② $M = 2.1 \times 3 = 6.3$ K

USE C6x10.5

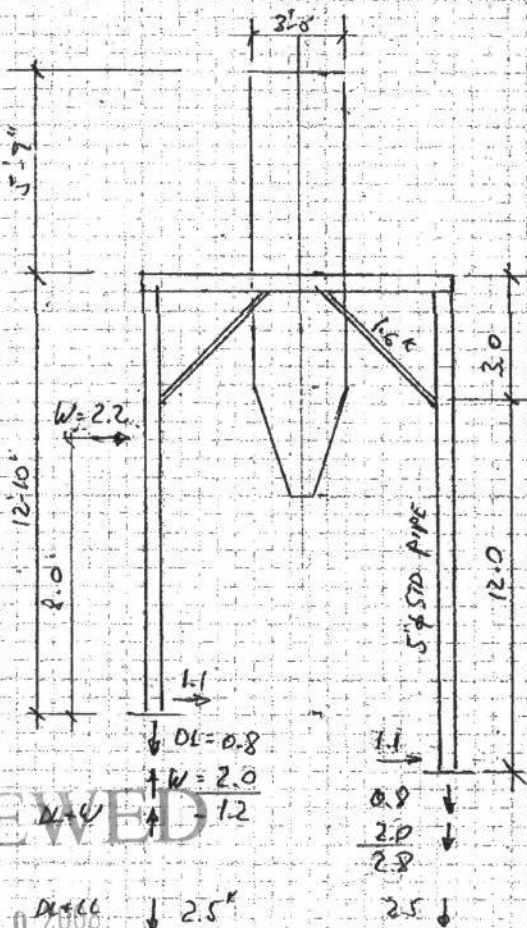


REVIEWED

JUN 10 2002

BOULDER COUNTY
BUILDING DIVISION



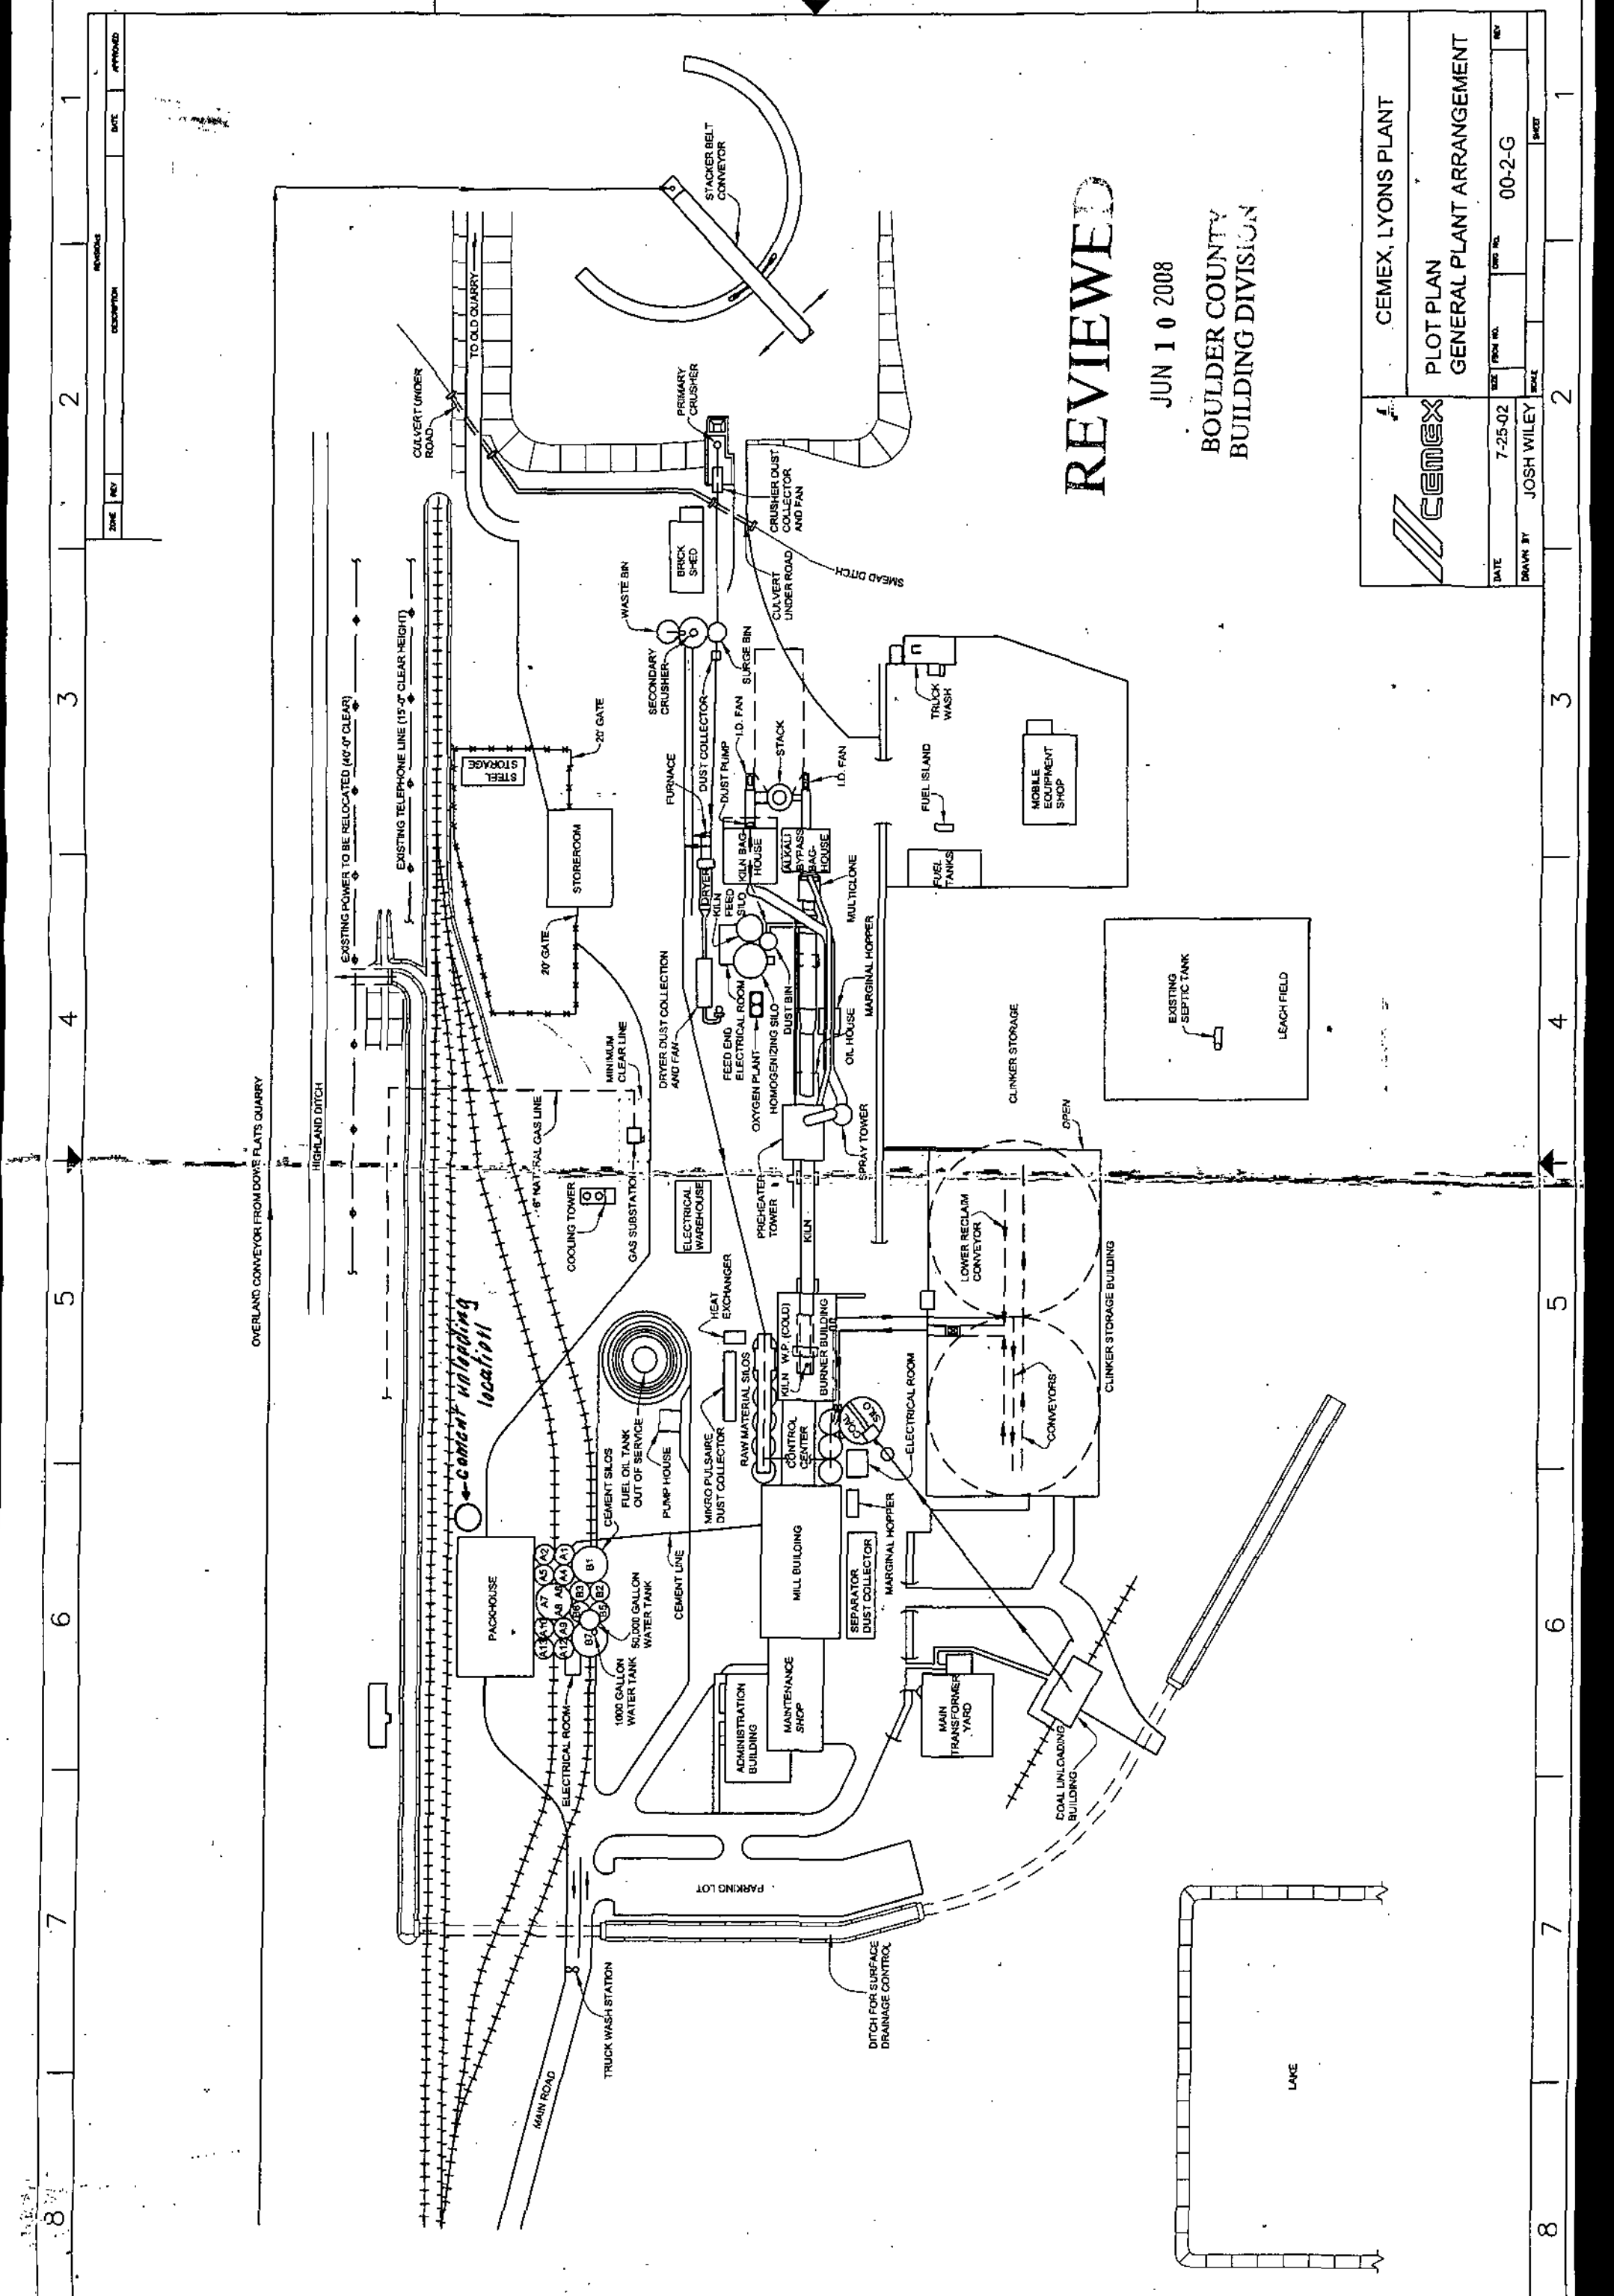


REVIEWED


JUN 10 2008
BOULDER COUNTY
BUILDING DIVISION

		CEMEX, LYONS PLANT	
PLOT PLAN		GENERAL PLANT ARRANGEMENT	
DATE	7-25-02	DESIGN NO.	00-2-G
DRAWN BY	JOSH WILEY	SCALE	


ZONE	REV	DESCRIPTION	DATE	APPROVED

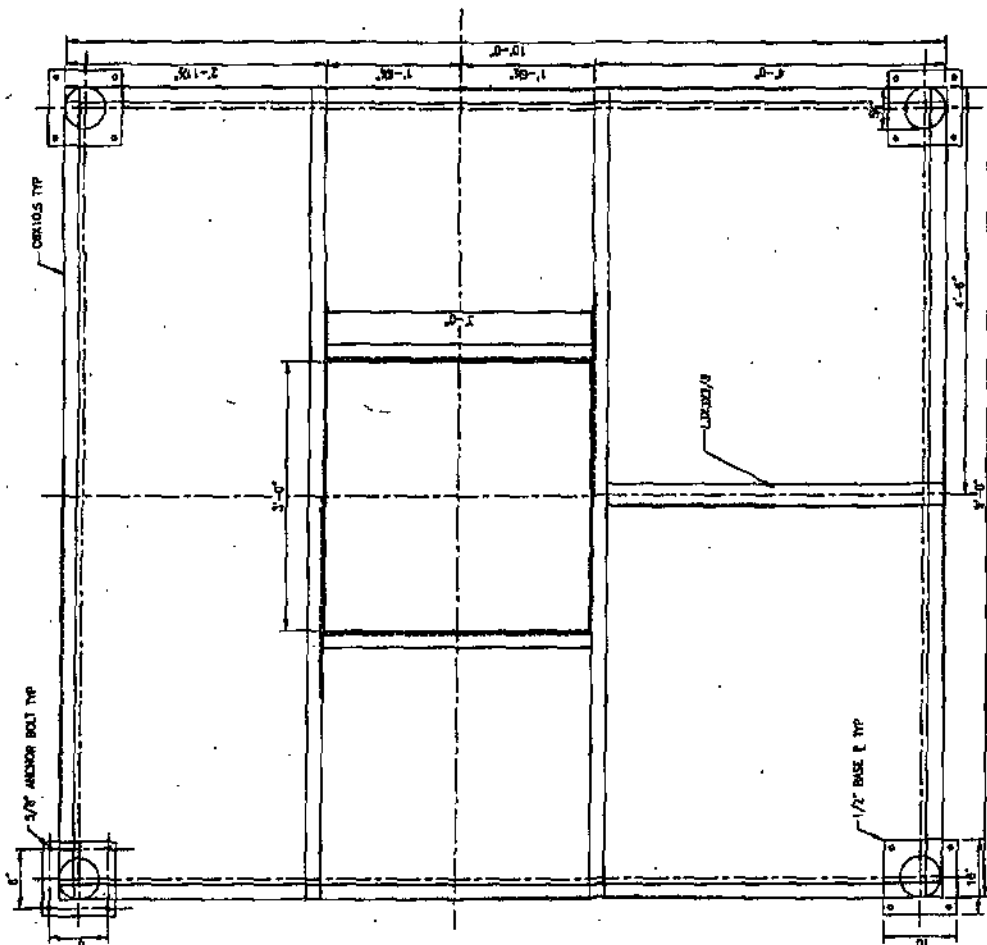

PLAN VIEW
1" = 1'-0"

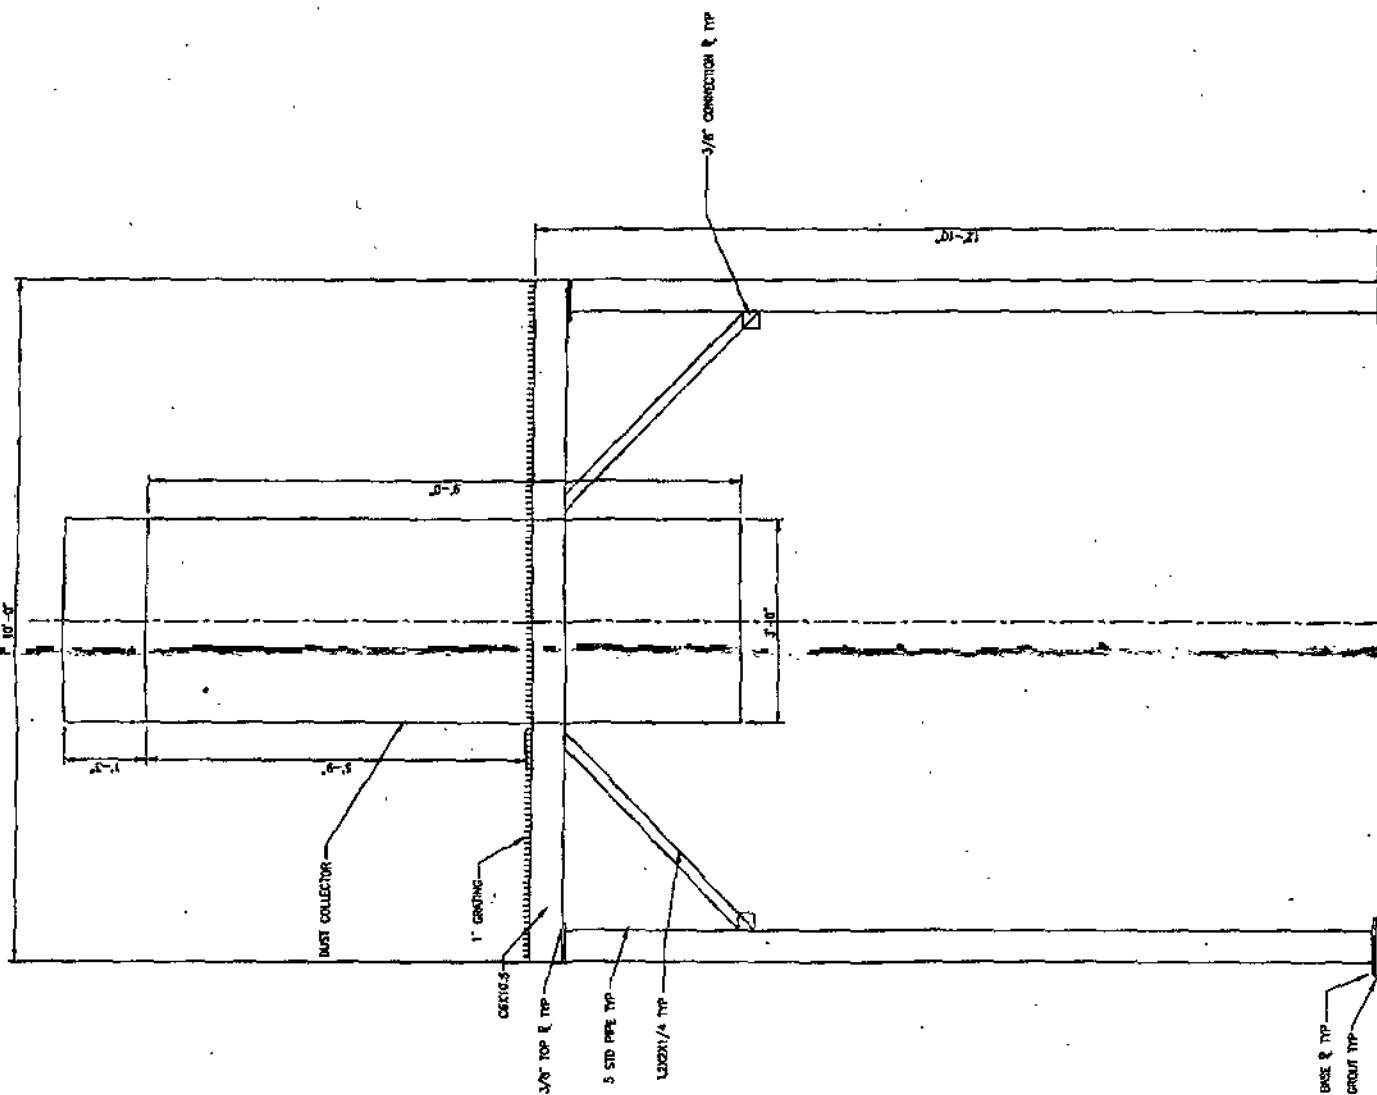

WEST ELEVATION
3/4" = 1'-0"

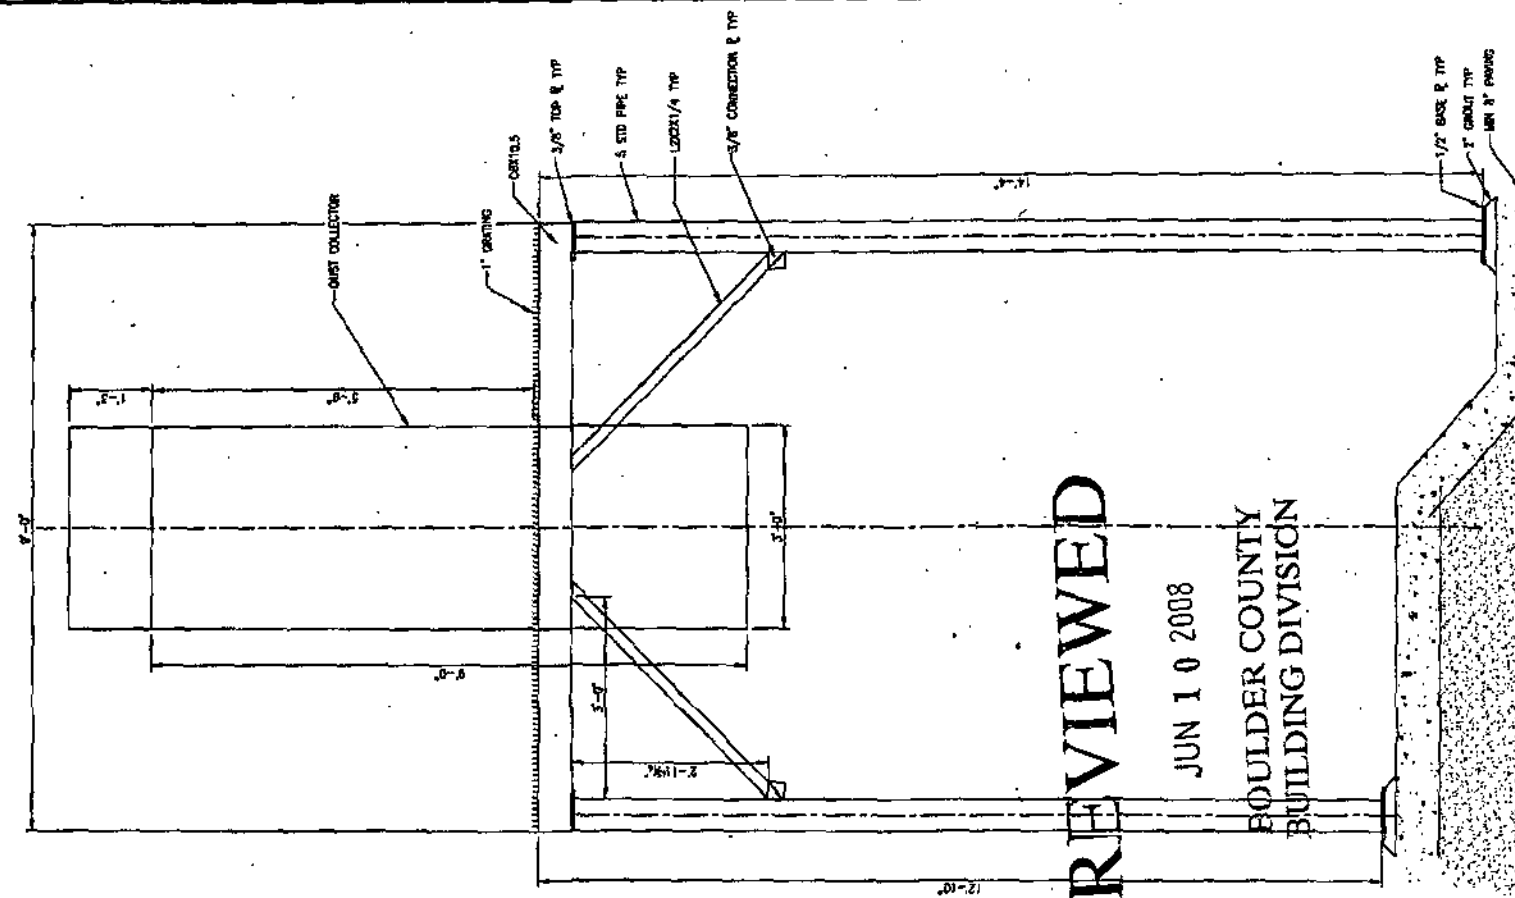


SOUTH ELEVATION
3/4" = 1'-0"

REVIEWED


JUN 10 2008

BOULDER COUNTY
BUILDING DIVISION

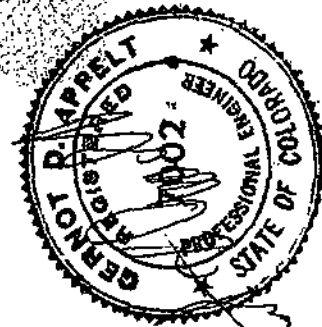


SMH ENGINEERING, INC.		80235
3608 SOUTH WASHINGTON LAKESIDE CO		
DATE	BY	SCALE
DESIGNED	CHK	AS NOTED
CHECKED	QA	
APPROVED	RA	
LIONS PLANT		
DUST COLLECTOR STRUCTURE		
CEMEX		
S-1		

REVISION 4	REVISION 3	REVISION 2	REVISION 1

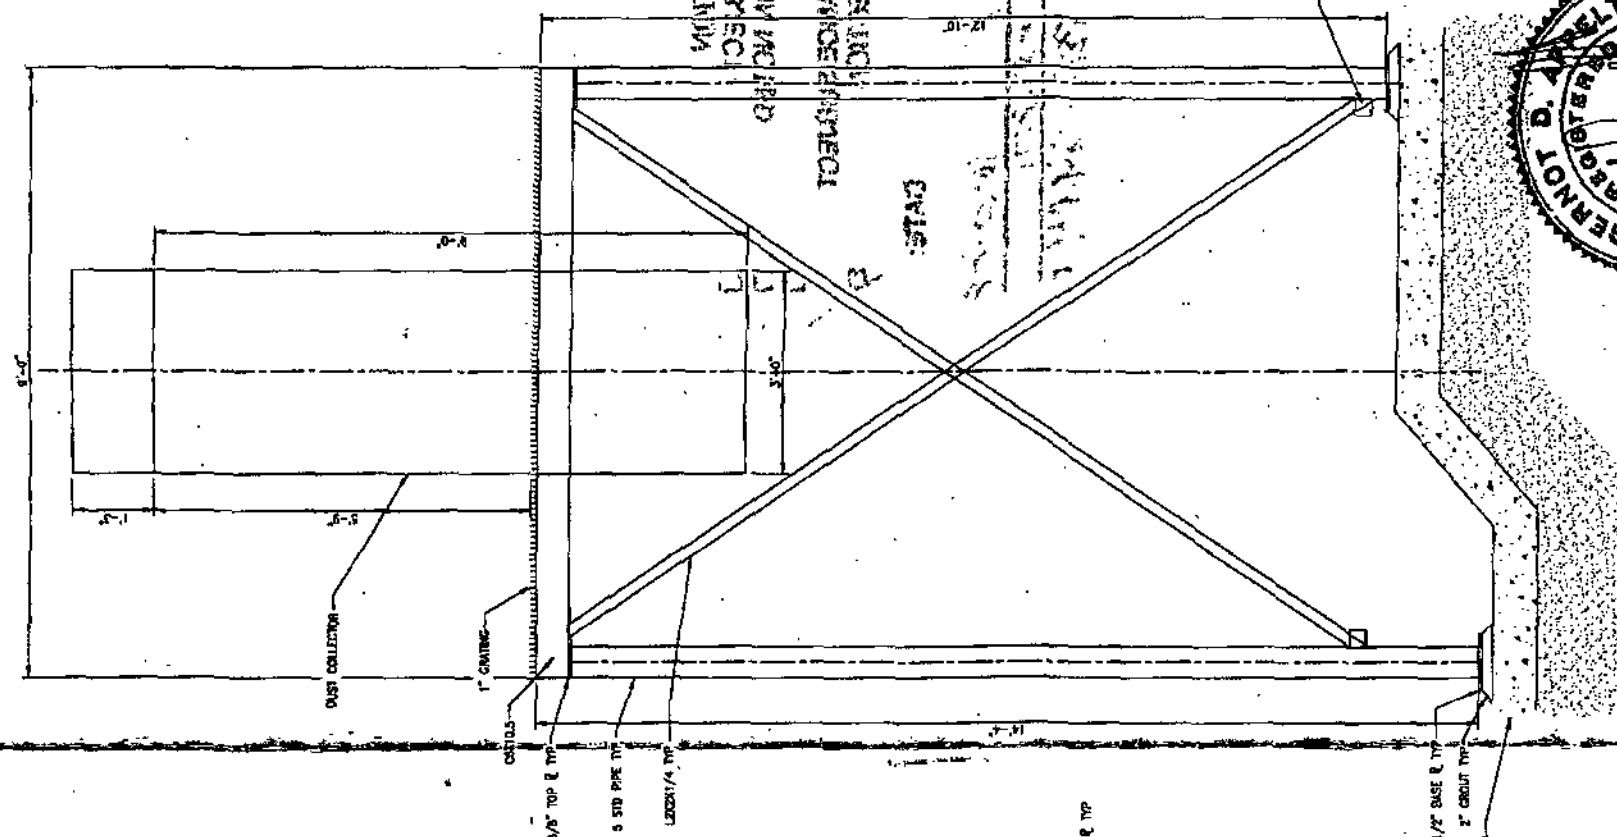

NORTH ELEVATION
3/4" = 1'-0"

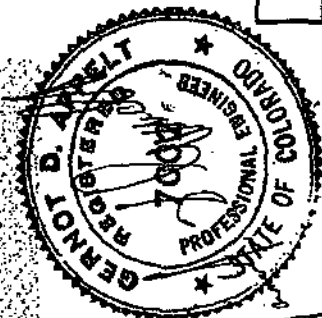

NO RECORDS IN THE
LAWST VOCEALVINGE DISTRICT
RECORDED
10 CORRECTION FAC RD
VOCALIST SUBJECT
2663411 SECONDARY
BIVVREVIEW

REVIEWED

JUN 10 2008

BOULDER COUNTY
BUILDING DIVISION

SMH ENGINEERING, INC.
3609 SOUTH WADSWORTH LAKEWOOD CO 80235

[illegible]