


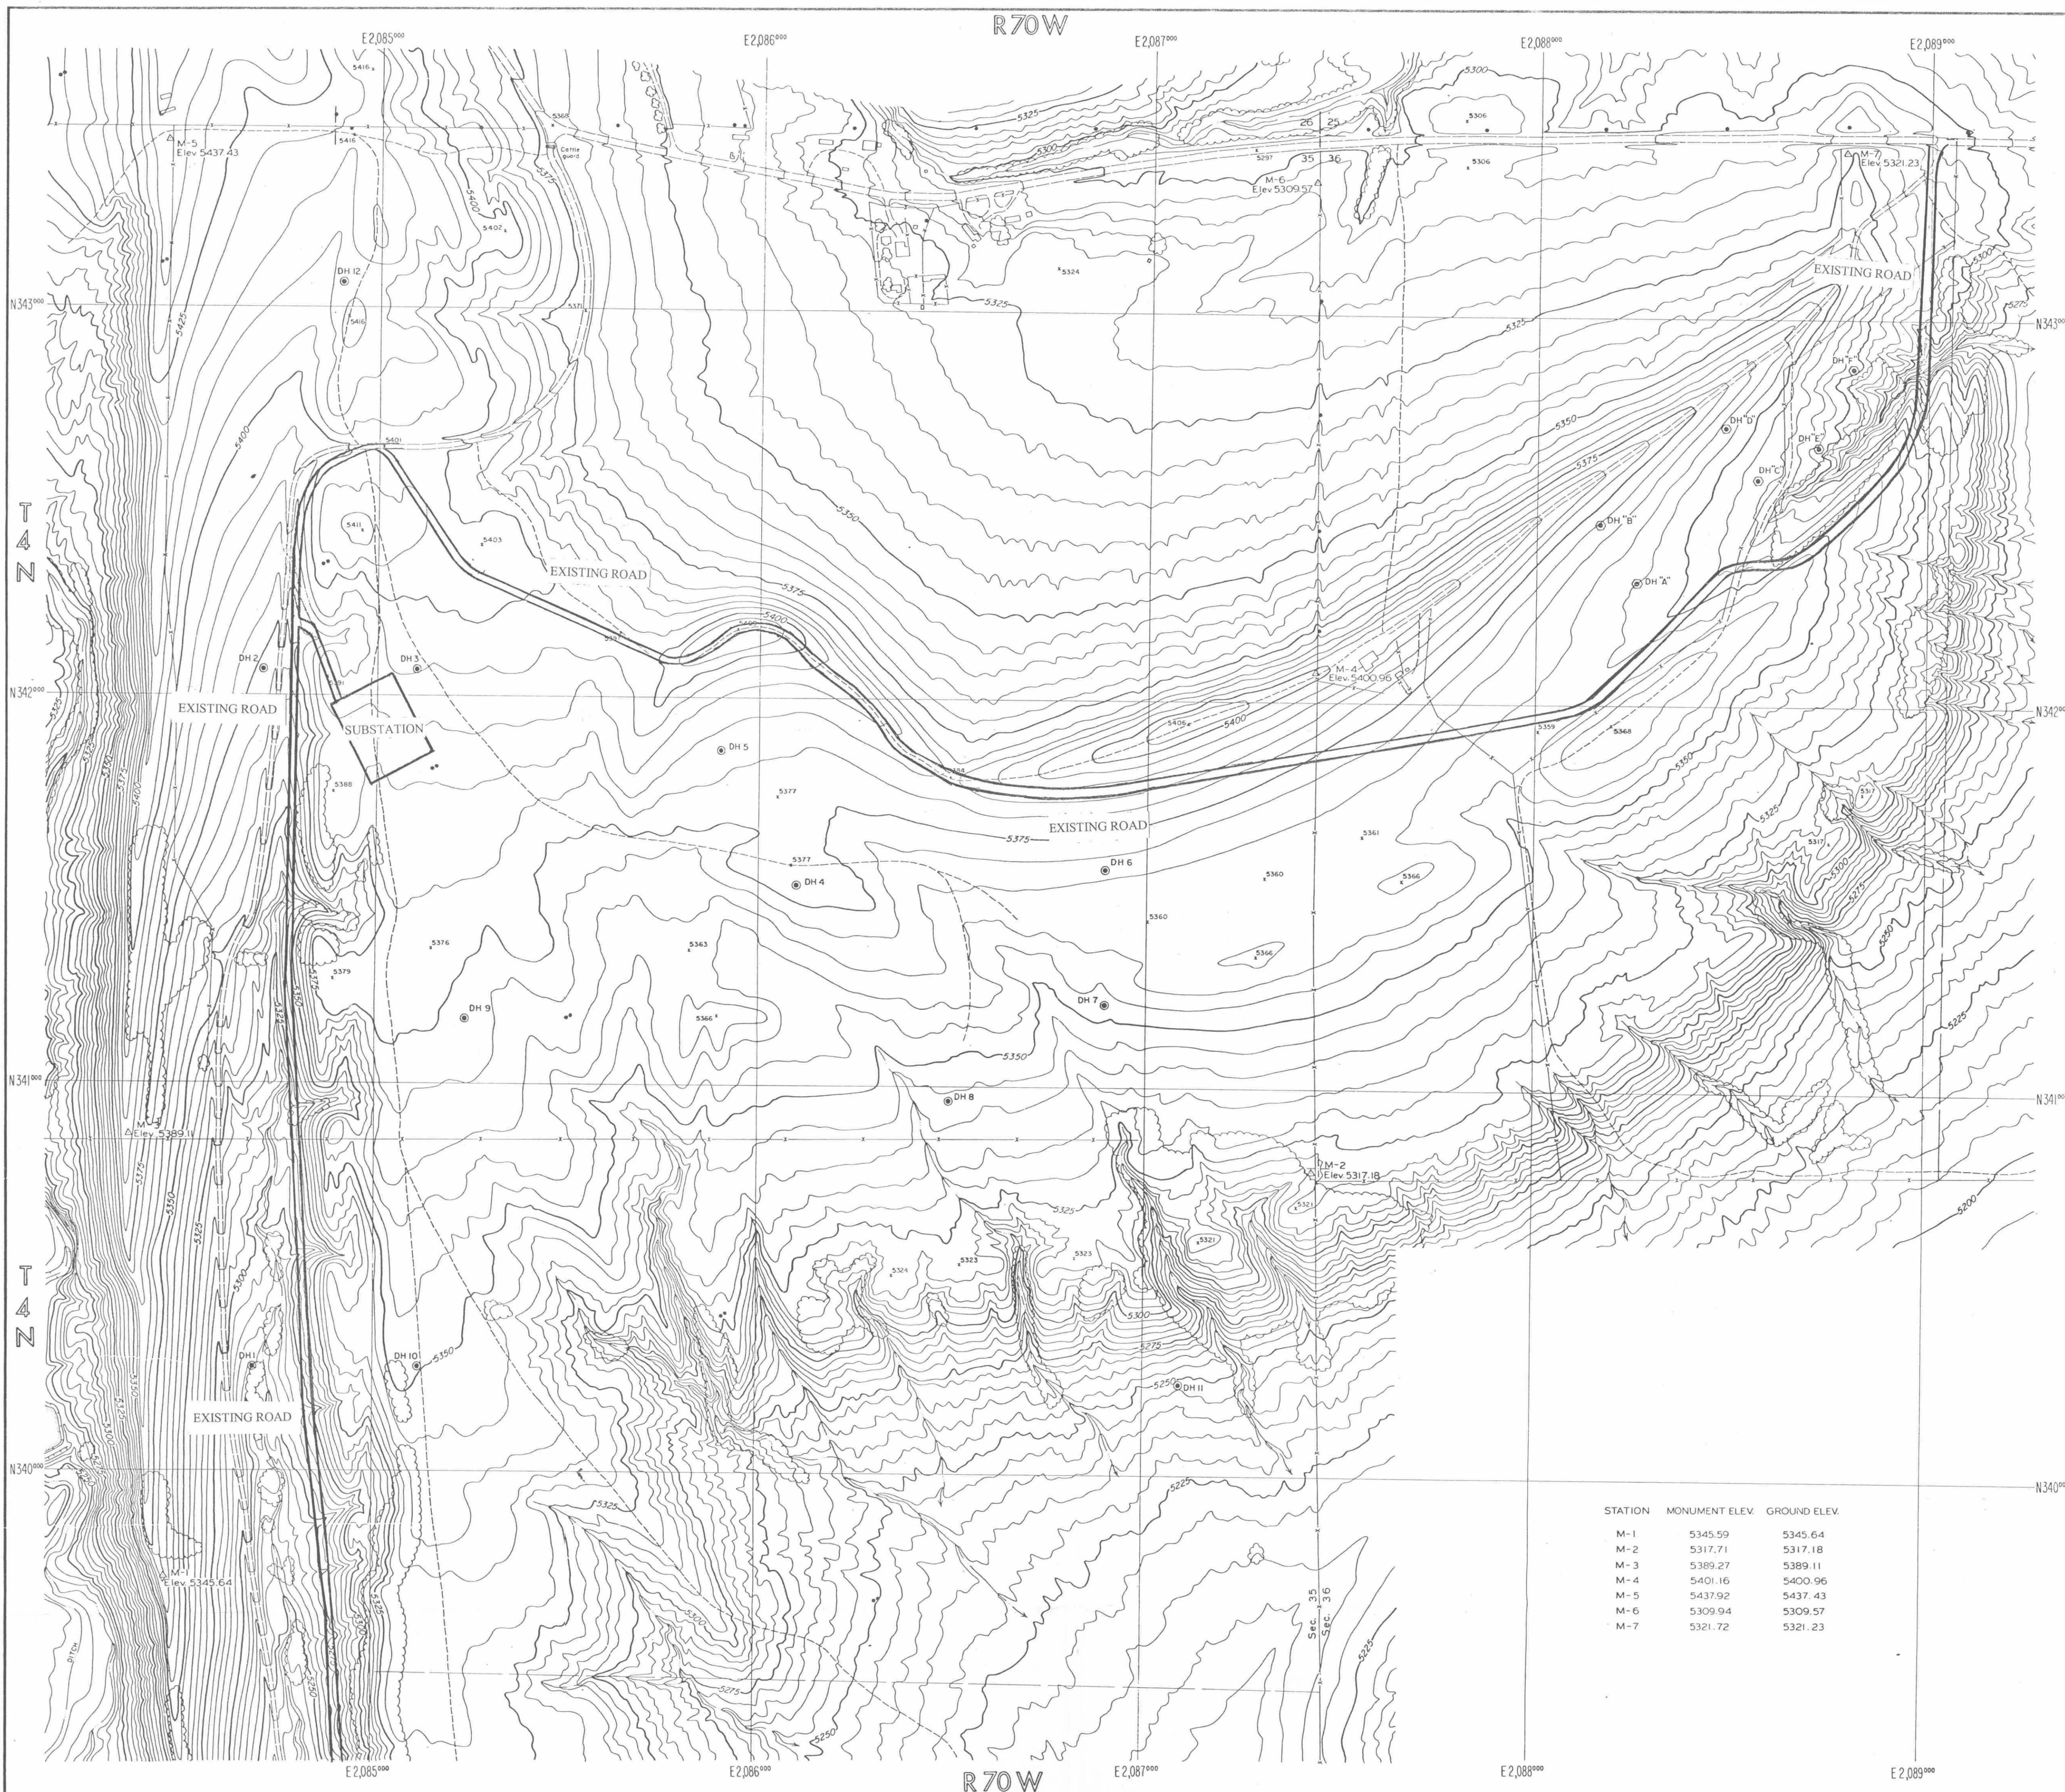


STATION	MONUMENT ELEV.	GROUND ELEV.
M-1	5345.59	5345.64
M-2	5317.71	5317.18
M-3	5389.27	5389.11
M-4	5401.16	5400.96
M-5	5437.92	5437.43
M-6	5309.94	5309.57
M-7	5321.72	5321.23

PREPARED BY
KNOX-BERGMAN-SHEARER CORP.
1600 OGDEN STREET, DENVER 80218

This map was photogrammetrically compiled from
1/12,000 (1"=1000') vertical aerial photography
dated Sept 28, 1972 by use of Kesh plotting equipment.

K-B-S Project 7296

SCALE: 1"=200'

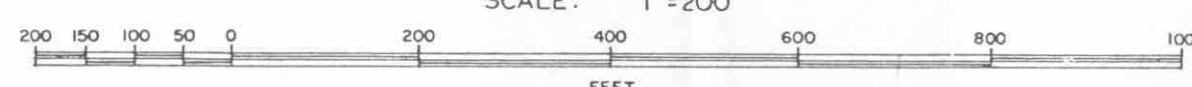

KEY
● DRILL HOLES
● CORE HOLES

TOPOGRAPHIC MAP
OF THE
LARIMER PIT
LARIMER COUNTY, COLORADO

PREPARED FOR
MARTIN MARIETTA CEMENT
(WESTERN DIVISION)
Date: October, 1972
Scale: 1/2400
Contour Interval: 5'
Sheet 1 of 1

Permit #: M-1977-341
Class: Revision
From: CEMEX, Inc.
Doc. Name: Topographic Map
Doc. Date (if no date stamp): 08/04/03

Confidential? N
Type-Seq: TR-1
To: DMG

RECEIVED
AUG 04 2003
Division of Minerals and Geology